Sua casa: luz, sol, calor e vento

Casa Maringá · relatório de simulação · Maringá, PR (lat -23,41, lon -51,93) · 16 de outubro de 2026
Clima: ano típico de BRA_PR_Maringa.868990_TMYx.2011-2025.epw · sol anual 1.882 kWh/m² · temperatura média 23,0 °C · vento médio 2,3 m/s

Como ler este relatório. Cada número vem com uma etiqueta colorida que diz se ele é bom ou ruim, em um **nível de 1 (péssimo) a 5 (excelente)**:

Excelente 5/5 Bom 4/5 Aceitável 3/5 Ruim 2/5 Péssimo 1/5

Cada etiqueta se baseia em uma **norma brasileira (ABNT)** quando existe, em um **padrão internacional** quando o Brasil não dá um número, ou em uma **regra prática** claramente identificada. Os quadros *O que conta como bom?* no fim de cada seção mostram a escala completa e a fonte. As paredes do modelo foram supostas como: *Bloco cerâmico furado de 8 furos 9x19x19 cm + 2 cm de reboco nos dois lados = parede de 13 cm (bloco padrão brasileiro)*; cobertura: *Telha cerâmica + sótão ventilado + laje de concreto de 12 cm*. Esses materiais e os tamanhos de janela (medidas comuns de catálogo por volta de 2012) são estimativas, não medições: use os resultados para comparar ambientes e opções, não como garantia.

1. Resumo

Cada ambiente é avaliado em até nove verificações, cada uma em um **nível de 1 (péssimo) a 5 (excelente)**; a coluna GERAL é o nível médio. As próximas páginas explicam cada verificação; a coluna de climatização mostra quanto um ar-condicionado custaria por ano:

Ambiente	Luz natural (NBR 15575)	Lâmpadas apagadas de dia	Sol na janela	Horas de conforto	Dia quente	Dia frio	Janela abrível	Custo de climatização	GERAL
Sala de estar + jantar	Intermediário 4/5	Frequentemente 4/5	Abaixo do mínimo 2/5	Bom 4/5	Intermediário 4/5	Superior 5/5	Atende ao mínimo 3/5	R$ 858/ano Baixa 4/5	Bom 3,8/5
Corredor	Sem exigência 3/5	Quase nunca 1/5	-	Excelente 5/5	-	-	-	-	Aceitável 3,0/5
Quarto 1	Superior 5/5	Quase sempre 5/5	Médio 4/5	Bom 4/5	Superior 5/5	Superior 5/5	Não atende 1/5	R$ 154/ano Baixa 4/5	Bom 4,0/5
Banheiro 1	Intermediário 4/5	Quase nunca 1/5	-	Bom 4/5	-	-	-	-	Aceitável 3,0/5
Quarto 2	Intermediário 4/5	Às vezes 3/5	Abaixo do mínimo 2/5	Bom 4/5	Superior 5/5	Superior 5/5	Não atende 1/5	R$ 112/ano Muito baixa 5/5	Bom 3,6/5
Banheiro 2	Intermediário 4/5	Quase nunca 1/5	-	Bom 4/5	-	-	-	-	Aceitável 3,0/5
Quarto 3	Intermediário 4/5	Frequentemente 4/5	Abaixo do mínimo 2/5	Bom 4/5	Superior 5/5	Superior 5/5	Não atende 1/5	R$ 109/ano Muito baixa 5/5	Bom 3,7/5
Cozinha	Superior 5/5	Quase sempre 5/5	Abaixo do mínimo 2/5	Aceitável 3/5	-	-	Atende ao mínimo 3/5	R$ 364/ano Moderada 3/5	Bom 3,7/5
Banheiro externo	-	Raramente 2/5	-	Aceitável 3/5	-	-	-	-	Aceitável 2,5/5
Depósito externo	-	Quase nunca 1/5	-	Aceitável 3/5	-	-	-	-	Ruim 2,0/5
Casa inteira								**R$ 1.597/ano**	Bom 3,5/5

O que funciona bem


- TV / jantar (fundos): 530 lux de luz natural no centro (nível superior da NBR 15575)
- Quarto 1: 524 lux de luz natural no centro (nível superior da NBR 15575)
- Cozinha: 191 lux de luz natural no centro (nível superior da NBR 15575)
- Ambiente mais confortável: Corredor (92% do ano na faixa de conforto; ao ar livre só 48%)
- Transmitância térmica U da parede externa: 2,52 W/m²K atende ao limite <= 3,7
- Capacidade térmica da parede externa: 134,0 kJ/m²K atende ao limite >= 130

O que merece atenção

- Quarto 2: lâmpadas necessárias em cerca de 52% das horas do dia
- Ambiente menos confortável: Banheiro externo (73%; 1539 h quente demais, 818 h frio demais)
- Quarto 1: área de janela abrível de só 4,7% do piso (a NBR 15575-4 pede 7%)
- Quarto 2: área de janela abrível de só 5,0% do piso (a NBR 15575-4 pede 7%)
- Quarto 3: área de janela abrível de só 5,1% do piso (a NBR 15575-4 pede 7%)
- Transmitância térmica U da cobertura (indicativa): 1,78 W/m²K contra o limite <= 1,5

PLANTA BAIXA - térreo

A casa é voltada para o NORTE (rua embaixo) - ambientes com nome, medidas e área; cor

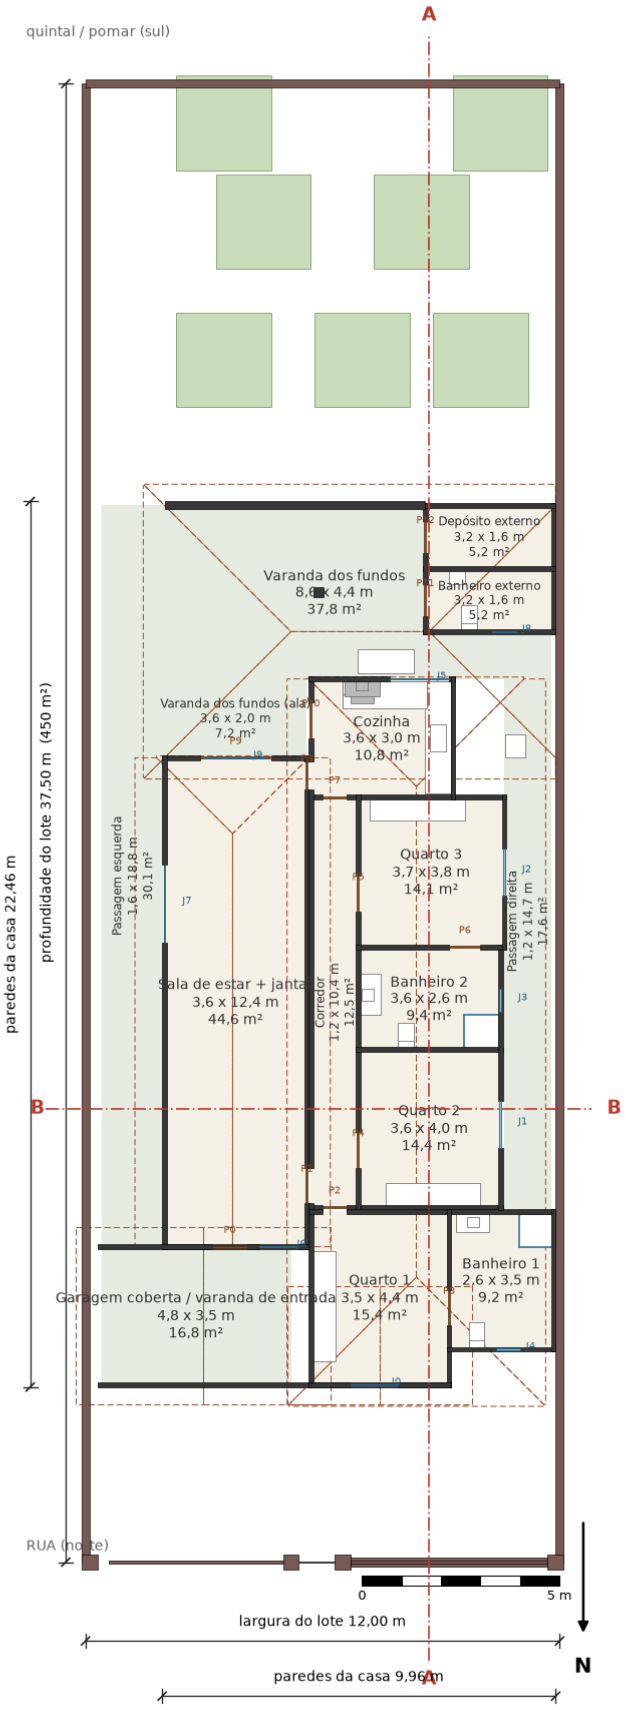

Escala 1:150 - medidas são estimativas de uma varredura em vídeo e do anúncio, não um levantamento

Planta do modelo (norte embaixo).

2. Luz natural

A luz natural economiza energia e deixa os ambientes agradáveis. A norma brasileira NBR 15575 pede pelo menos **60 lux** no centro de salas, dormitórios e cozinhas (lux = quanta luz chega a uma mesa). Para comparar: um dia claro e nublado ao ar livre tem milhares de lux.


2,1 Ensaio brasileiro: luz no centro do ambiente, lâmpadas apagadas

Ambiente	Lux no centro	Veredito
Sala de estar (frente)	93	Intermediário 4/5
TV / jantar (fundos)	530	Superior 5/5
Corredor	0	Sem exigência 3/5
Quarto 1	524	Superior 5/5
Banheiro 1	43	Intermediário 4/5
Quarto 2	93	Intermediário 4/5
Banheiro 2	30	Intermediário 4/5
Quarto 3	114	Intermediário 4/5
Cozinha	191	Superior 5/5
Banheiro externo	52	Não atende 1/5
Depósito externo	0	Não atende 1/5

2,2 Quanto do ambiente é claro, e quando preciso de lâmpada?

Ambiente	Meta (lux)	Piso que atinge a meta	Dia com lâmpadas apagadas	Sol forte (ASE)
Sala de estar (frente)	150	26% Abaixo da meta 2/5	51% Frequentemente 4/5	0% Muito baixa 5/5
TV / jantar (fundos)	150	100% Ambiente inteiro 5/5	97% Quase sempre 5/5	7% Aceitável 4/5
Corredor	-	-	0% Quase nunca 1/5	0% Muito baixa 5/5
Quarto 1	100	100% Ambiente inteiro 5/5	96% Quase sempre 5/5	10% Alta 2/5
Banheiro 1	-	-	2% Quase nunca 1/5	0% Muito baixa 5/5
Quarto 2	100	100% Ambiente inteiro 5/5	48% Às vezes 3/5	0% Muito baixa 5/5
Banheiro 2	-	-	0% Quase nunca 1/5	0% Muito baixa 5/5
Quarto 3	100	100% Ambiente inteiro 5/5	53% Frequentemente 4/5	0% Muito baixa 5/5
Cozinha	200	100% Ambiente inteiro 5/5	83% Quase sempre 5/5	0% Muito baixa 5/5
Banheiro externo	-	-	14% Raramente 2/5	0% Muito baixa 5/5
Depósito externo	-	-	0% Quase nunca 1/5	0% Muito baixa 5/5


Meta = o nível de luz natural que a EN 17037 (Anexo Nacional do Reino Unido para moradias) recomenda: 100 lux dormitório, 150 lux sala, 200 lux cozinha. “Lâmpadas apagadas” = parcela das horas entre 8h e 18h em que a média de luz natural já atinge o nível de luz geral da seção 3.

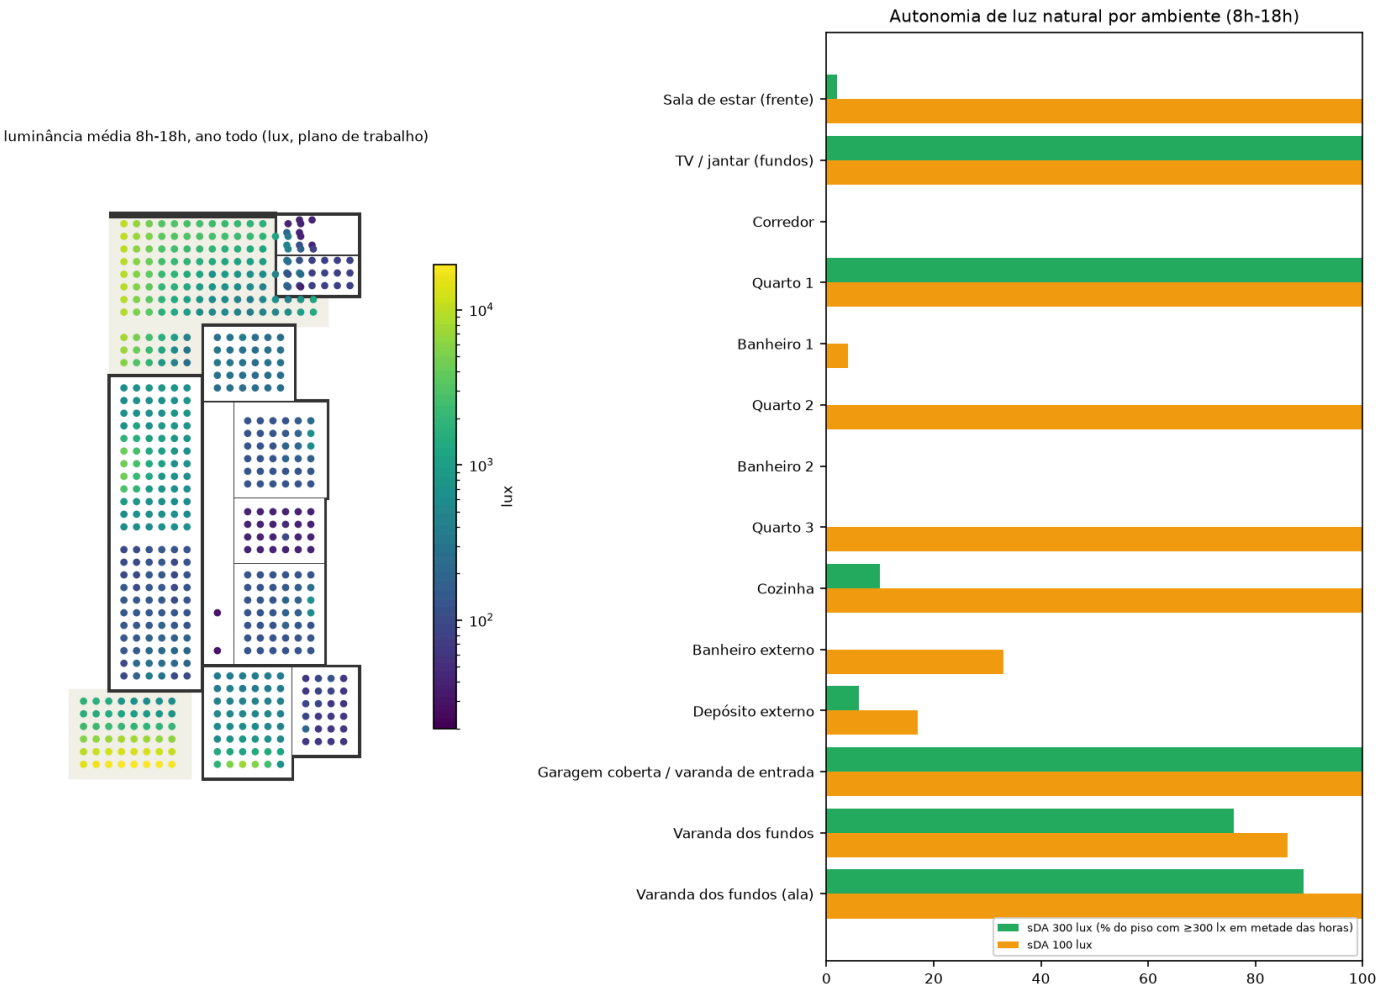

Esquerda: luz média no piso ao longo do ano. Direita: parcela de cada ambiente que atinge 100 e 300 lux.

2,3 Sol que chega às janelas

Ambiente	Sol na janela, horas/dia (início da primavera)	Veredito
Sala de estar (frente)	0,0	Abaixo do mínimo 2/5
TV / jantar (fundos)	0,6	Abaixo do mínimo 2/5
Quarto 1	3,8	Médio 4/5
Quarto 2	0,0	Abaixo do mínimo 2/5
Quarto 3	0,0	Abaixo do mínimo 2/5
Cozinha	0,0	Abaixo do mínimo 2/5

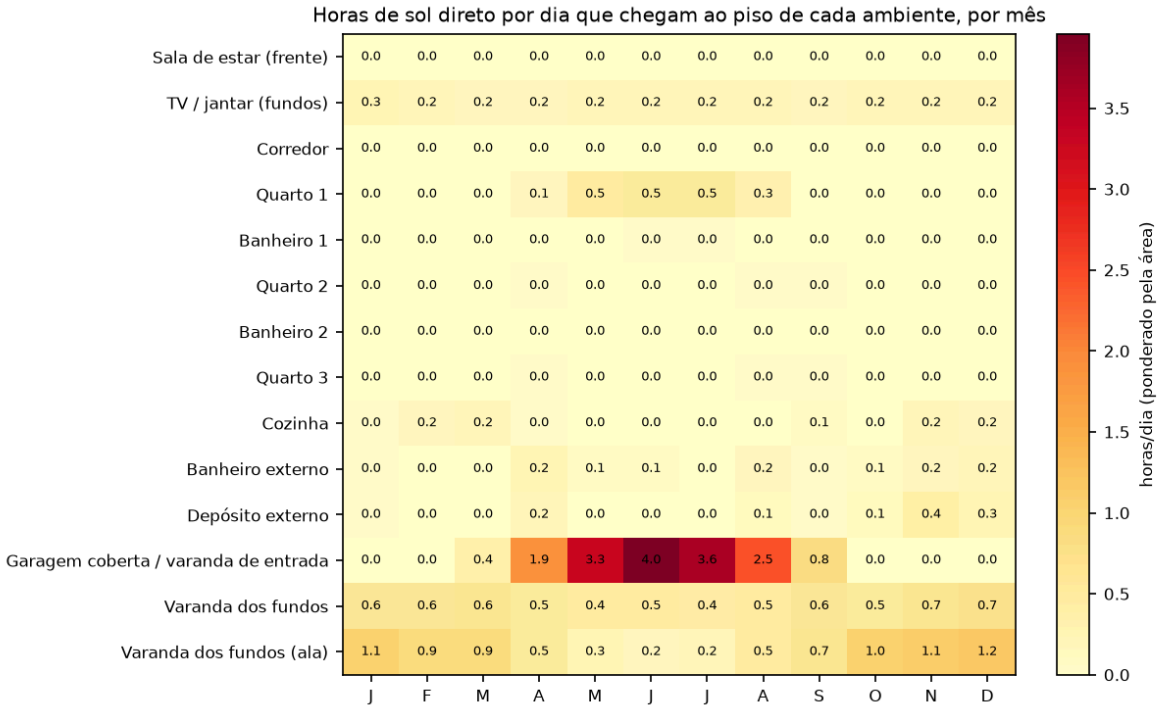

Horas por dia de sol direto que chegam ao piso de cada ambiente, por mês (J = janeiro).




Onde o sol bate no piso em quatro datas-chave.

2,4 O sol e suas sombras ao longo do dia no modelo 3D

Estas imagens vêm do mesmo modelo 3D e do mesmo cálculo do sol do visualizador interativo: três datas-chave, cinco horários. São desenhadas as sombras da casa, da cobertura, dos muros e das árvores; os pisos que recebem sol direto ficam amarelos/laranja. no inverno o sol baixo entra fundo nos ambientes voltados para ele, enquanto no verão o sol fica alto ao meio-dia e a cobertura sombreia a casa.

O sol e suas sombras ao longo do dia no modelo 3D (vista do noroeste: o lado norte está mais perto de você)

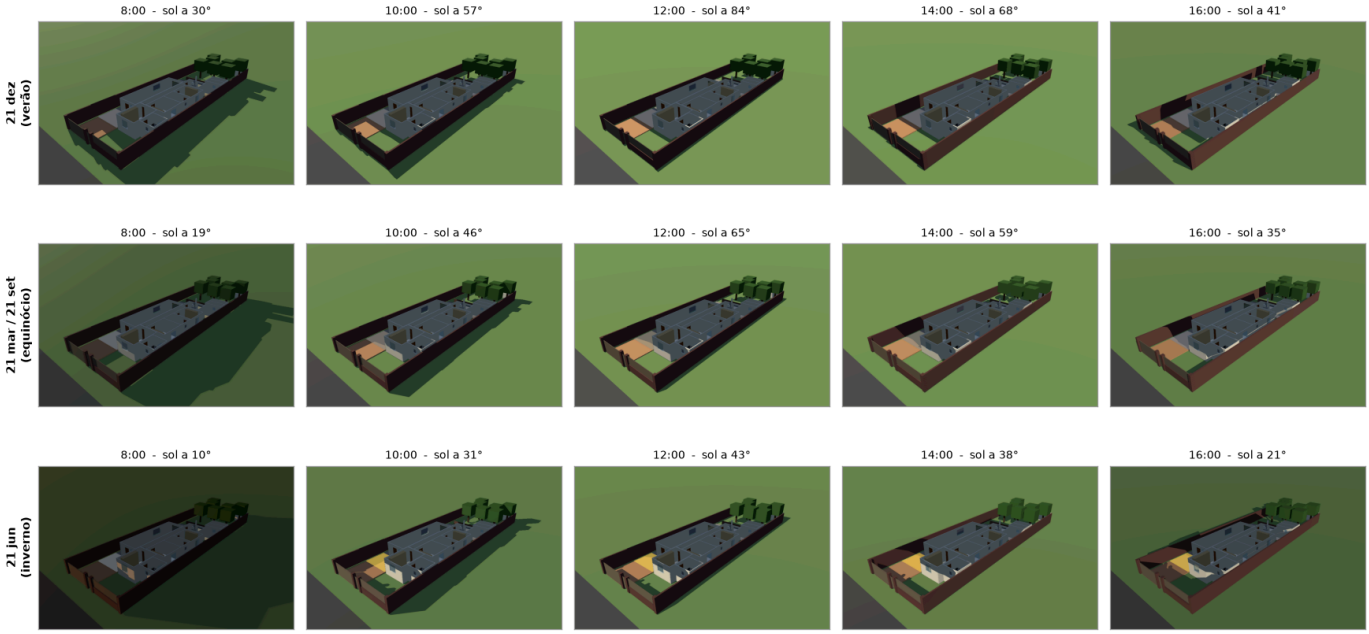

Bússola: o leste fica à esquerda de cada imagem e o oeste à direita, então o sol nasce à esquerda e se põe à direita. Piso amarelo = sol direto.

Sol e sombras ao longo do dia: vista 3D do noroeste (frente / rua mais perto).

O sol e suas sombras ao longo do dia, vistos de cima (norte verdadeiro embaixo)



Bússola: o leste fica à esquerda de cada imagem e o oeste à direita, então o sol nasce à esquerda e se põe à direita. Piso amarelo = sol direto.

Os mesmos momentos vistos de cima (rua / frente embaixo).

O que conta como bom? (luz)

Luz natural no centro do ambiente (ensaio da NBR 15575) Norma brasileira

Luz natural em um plano na altura de uma mesa (0,75 m), no meio do ambiente, em 23 de abril e 23 de outubro às 9h30 e às 15h30, com céu parcialmente nublado e lâmpadas apagadas. Vale a menor das quatro leituras. Aplica-se a salas, dormitórios, cozinhas e áreas de serviço.

Não atende 1/5	abaixo de 60 lux	Abaixo do mínimo de 60 lux: é preciso acender a luz até ao meio-dia.
Mínimo 3/5	60 a 90 lux	Atende ao mínimo exigido pela norma.
Intermediário 4/5	90 a 120 lux	Melhor que o mínimo.
Superior 5/5	120 ou mais lux	Nível máximo da norma.

Esta casa: Sala de estar (frente) 93 lux Intermediário 4/5 | TV / jantar (fundos) 530 lux Superior 5/5 | Quarto 1 524 lux Superior 5/5 | Quarto 2 93 lux Intermediário 4/5 | Quarto 3 114 lux Intermediário 4/5 | Cozinha 191 lux Superior 5/5

Fonte: ABNT NBR 15575-1:2013 (Edificações habitacionais — Desempenho), requisitos de iluminação natural e desempenho térmico. Nosso cálculo usa o clima típico da semana em torno dessas datas e só a luz do céu (sem sol direto), portanto fica a favor da segurança.

Luz natural no centro do ambiente (ensaio da NBR 15575): banheiros, corredores, escadas, garagens Norma brasileira

O mesmo ensaio, para ambientes onde as pessoas não ficam muito tempo.

Sem exigência 3/5	abaixo de 30 lux	A norma não exige luz natural aqui (nível mínimo: "não requerido").
Intermediário 4/5	30 a 45 lux	Atende ao nível intermediário.
Superior 5/5	45 ou mais lux	Atende ao nível superior.

Esta casa: Corredor 0 lux Sem exigência 3/5 | Banheiro 1 43 lux Intermediário 4/5 | Banheiro 2 30 lux Intermediário 4/5

Fonte: ABNT NBR 15575-1:2013 (Edificações habitacionais — Desempenho), requisitos de iluminação natural e desempenho térmico.

Parcela do piso que atinge a luz recomendada para moradias Padrão internacional

Porcentagem do piso do ambiente que recebe, só de luz natural, pelo menos a luz-meta (100 lux no dormitório, 150 lux na sala, 200 lux na cozinha) durante pelo menos metade das horas do dia (8h às 18h).

Abaixo da meta 2/5	abaixo de 50 % do piso	Menos da metade do ambiente atinge a meta: será preciso acender lâmpadas de dia.
Atende à meta 4/5	50 a 95 % do piso	Pelo menos metade do piso atinge a meta durante metade do dia.
Ambiente inteiro 5/5	95 ou mais % do piso	Praticamente todo o ambiente atinge a meta.

Esta casa: Sala de estar (frente) 26% Abaixo da meta 2/5 | TV / jantar (fundos) 100% Ambiente inteiro 5/5 | Quarto 1 100% Ambiente inteiro 5/5 | Quarto 2 100% Ambiente inteiro 5/5 | Quarto 3 100% Ambiente inteiro 5/5 | Cozinha 100% Ambiente inteiro 5/5

Fonte: EN 17037:2018 Iluminação natural em edifícios (Anexo Nacional do Reino Unido para moradias: 100/150/200 lx; insolação 1,5/3/4 h). A EN 17037 pede a luz-meta em pelo menos 50% da área durante metade das horas de luz do dia (mais um nível menor em 95% da área).

Autonomia espacial de luz natural sDA 300/50% (padrão para ambientes de trabalho) Padrão internacional

Porcentagem do piso com pelo menos 300 lux de luz natural durante pelo menos metade das horas de uso. 300 lux é um nível de luz de TRABALHO; portanto este é um teste rigoroso, útil para escritório em casa, cozinha ou estudo. Dormitórios e corredores não precisam chegar lá.

Abaixo do recomendado 2/5	abaixo de 55 % do piso	Menos de 55% do piso atinge 300 lux durante metade do dia.
Nominalmente aceitável 3/5	55 a 75 % do piso	Aceito pela IES / LEED (55% ou mais).
Preferível 5/5	75 ou mais % do piso	Nível preferível (75% ou mais).

Esta casa: Sala de estar (frente) 2% Abaixo do recomendado 2/5 | TV / jantar (fundos) 100% Preferível 5/5 | Corredor 0% Abaixo do recomendado 2/5 | Quarto 1 100% Preferível 5/5 | Banheiro 1 0% Abaixo do recomendado 2/5 | Quarto 2 0% Abaixo do recomendado 2/5 | Banheiro 2 0% Abaixo do recomendado 2/5 | Quarto 3 0% Abaixo do recomendado 2/5 | Cozinha 10% Abaixo do recomendado 2/5 | Banheiro externo 0% Abaixo do recomendado 2/5 | Depósito externo 6% Abaixo do recomendado 2/5

Fonte: IES LM-83-12 (sDA e ASE), como usado no LEED v4,1.

Exposição solar anual ASE (risco de ofuscamento e superaquecimento) Padrão internacional

Porcentagem do piso que recebe sol direto forte (acima de 1000 lux) por mais de 250 horas por ano. Valores altos significam ofuscamento, móveis desbotados e calor.

Muito baixa 5/5	abaixo de 3 % do piso	Quase nenhum sol direto forte.
Aceitável 4/5	3 a 10 % do piso	Dentro do limite de 10% usado pela IES / LEED.
Alta 2/5	10 a 20 % do piso	Acima do limite de 10%: considere cortinas, persianas ou um beiral.
Muito alta 1/5	20 ou mais % do piso	Grande área com sol forte por muito tempo: ofuscamento e calor prováveis.

Esta casa: Sala de estar (frente) 0% Muito baixa 5/5 | TV / jantar (fundos) 7% Aceitável 4/5 | Corredor 0% Muito baixa 5/5 | Quarto 1 10% Alta 2/5 | Banheiro 1 0% Muito baixa 5/5 | Quarto 2 0% Muito baixa 5/5 | Banheiro 2 0% Muito baixa 5/5 | Quarto 3 0% Muito baixa 5/5 | Cozinha 0% Muito baixa 5/5 | Banheiro externo 0% Muito baixa 5/5 | Depósito externo 0% Muito baixa 5/5

Fonte: IES LM-83-12 (sDA e ASE), como usado no LEED v4,1.

Horas do dia sem precisar de lâmpadas Regra prática

Parcela das horas do dia em que a luz natural média do ambiente já atinge o nível geral recomendado (veja a tabela de lâmpadas), e as luzes podem ficar apagadas.

Quase nunca 1/5	abaixo de 10 % das horas entre 8h e 18h	Você vai acender as luzes o dia todo.
Raramente 2/5	10 a 25 % das horas entre 8h e 18h	Lâmpadas necessárias na maior parte do dia.
Às vezes 3/5	25 a 50 % das horas entre 8h e 18h	Lâmpadas necessárias em dias nublados e de manhã / à tarde.
Frequentemente 4/5	50 a 75 % das horas entre 8h e 18h	Lâmpadas quase sempre apagadas de dia.
Quase sempre 5/5	75 ou mais % das horas entre 8h e 18h	Lâmpadas apagadas quase o dia inteiro.

Esta casa: Sala de estar (frente) 51% Frequentemente 4/5 | TV / jantar (fundos) 97% Quase sempre 5/5 | Corredor 0% Quase nunca 1/5 | Quarto 1 96% Quase sempre 5/5 | Banheiro 1 2% Quase nunca 1/5 | Quarto 2 48% Às vezes 3/5 | Banheiro 2 0% Quase nunca 1/5 | Quarto 3 53% Frequentemente 4/5 | Cozinha 83% Quase sempre 5/5 | Banheiro externo 14% Raramente 2/5 | Depósito externo 0% Quase nunca 1/5

Fonte: Regra prática deste estudo (nenhuma norma dá um número); ABNT NBR 5413:1992 (cancelada em 2013, mas ainda a referência brasileira mais usada para iluminação de RESIDÊNCIAS).

Sol direto na janela no início da primavera Padrão internacional

Horas de sol direto que chegam às janelas do ambiente em um dia típico do início da primavera: 1º de agosto a 21 de setembro no hemisfério sul, 1º de fevereiro a 21 de março no norte (as datas da EN 17037). Sol no inverno e no início da primavera faz bem à saúde e aquece.

Abaixo do mínimo 2/5	abaixo de 1,5 horas/dia	Menos de 1,5 h de sol: o ambiente parece sem sol.
Mínimo 3/5	1,5 a 3 horas/dia	Atende ao mínimo da EN 17037 (1,5 h).
Médio 4/5	3 a 4 horas/dia	Atende ao nível médio da EN 17037 (3 h).
Alto 5/5	4 ou mais horas/dia	Atende ao nível alto da EN 17037 (4 h).

Esta casa: Sala de estar (frente) 0,0 h Abaixo do mínimo 2/5 | TV / jantar (fundos) 0,6 h Abaixo do mínimo 2/5 | Quarto 1 3,8 h Médio 4/5 | Quarto 2 0,0 h Abaixo do mínimo 2/5 | Quarto 3 0,0 h Abaixo do mínimo 2/5 | Cozinha 0,0 h Abaixo do mínimo 2/5

Fonte: EN 17037:2018 Iluminação natural em edifícios (Anexo Nacional do Reino Unido para moradias: 100/150/200 lx; insolação 1,5/3/4 h). A EN 17037 pede isso para pelo menos um cômodo principal (de preferência a sala); banheiros e corredores são isentos.

3. Lâmpadas: quanta luz instalar (lumens)

Lux é a luz que chega a uma superfície; **lumens** é a luz que uma lâmpada emite. Para ter uma média de X lux em um piso de A m² você precisa de X × A ÷ (utilização × manutenção = 0,45 × 0,8 = 0,36) lumens. A coluna "mínimo" é só lux × m².

3,1 Níveis de luz recomendados em casa


Tipo de ambiente	Luz geral (lux): mín / recomendado / máx	Luz de tarefa (lux)	Fonte
Sala de estar / jantar	100 / 150 / 200	300 / 500 / 750 - leitura, escrita, costura	NBR 5413 (residências); EN 12464-1 / NBR 8995-1 para tarefas de leitura
Dormitório	100 / 150 / 200	200 / 300 / 500 - leitura na cama, penteadeira	NBR 5413 (residências)
Cozinha	100 / 150 / 200	200 / 300 / 500 - fogão, pia e bancada (a EN 12464-1 pede 500)	NBR 5413 (residências); EN 12464-1
Banheiro	100 / 150 / 200	200 / 300 / 500 - espelho (barba, maquiagem)	NBR 5413 (residências)
Corredor / circulação	75 / 100 / 150	-	NBR 5413 (residências)
Lavanderia / depósito / banheiro externo	100 / 150 / 200	200 / 300 / 500 - lavanderia e ferramentas	NBR 5413 (residências)
Varanda / garagem (área externa coberta)	50 / 75 / 100	-	NBR 5413 (garagens 50-75-100)

Leitura: ilumine o ambiente no nível geral (100-200 lux) e acrescente uma **luminária de leitura direcional de cerca de 450-800 lumens** (cerca de 4-8 W de LED) perto da página para chegar a **300-500 lux** nela (NBR ISO/CIE 8995-1 e EN 12464-1 para leitura e escrita; NBR 5413 para residências). Ler só com os 100-150 lux da luz geral cansa a vista. Para ter noção: 100 lm = luz noturna / lâmpada vela pequena; 450 lm = equivalente a uma lâmpada incandescente de 40 W; 800 lm = equivalente a uma lâmpada incandescente de 60 W; 1600 lm = equivalente a uma lâmpada incandescente de 100 W.

3,2 Lumens de lâmpada para cada ambiente desta casa

Ambiente	m²	Meta de luz geral	Luz de tarefa (leitura etc.)	Lumens das lâmpadas: mínimo - projeto	Watts de LED (projeto)
Sala de estar (frente)	21,2	150 lux	500 lux (leitura, escrita, costura)	3.186 - 8.850	88
TV / jantar (fundos)	23,4	150 lux	500 lux (leitura, escrita, costura)	3.510 - 9.750	98
Corredor	12,5	100 lux	-	1.248 - 3.467	35
Quarto 1	15,4	150 lux	300 lux (leitura na cama, penteadeira)	2.310 - 6.417	64
Banheiro 1	9,2	150 lux	300 lux (espelho (barba, maquiagem))	1.386 - 3.850	38
Quarto 2	14,4	150 lux	300 lux (leitura na cama, penteadeira)	2.160 - 6.000	60
Banheiro 2	9,4	150 lux	300 lux (espelho (barba, maquiagem))	1.404 - 3.900	39
Quarto 3	14,1	150 lux	300 lux (leitura na cama, penteadeira)	2.109 - 5.858	59
Cozinha	10,8	150 lux	300 lux (fogão, pia e bancada (a EN 12464-1 pede 500))	1.620 - 4.500	45
Banheiro externo	5,2	150 lux	300 lux (lavanderia e ferramentas)	778 - 2.160	22
Depósito externo	5,2	150 lux	300 lux (lavanderia e ferramentas)	778 - 2.160	22

Use o extremo inferior para paredes e tetos claros e boas luminárias; o superior para cores escuras ou spots embutidos. LED a 100 lm por watt. A luz natural já cobre parte do dia (seção 2,2).

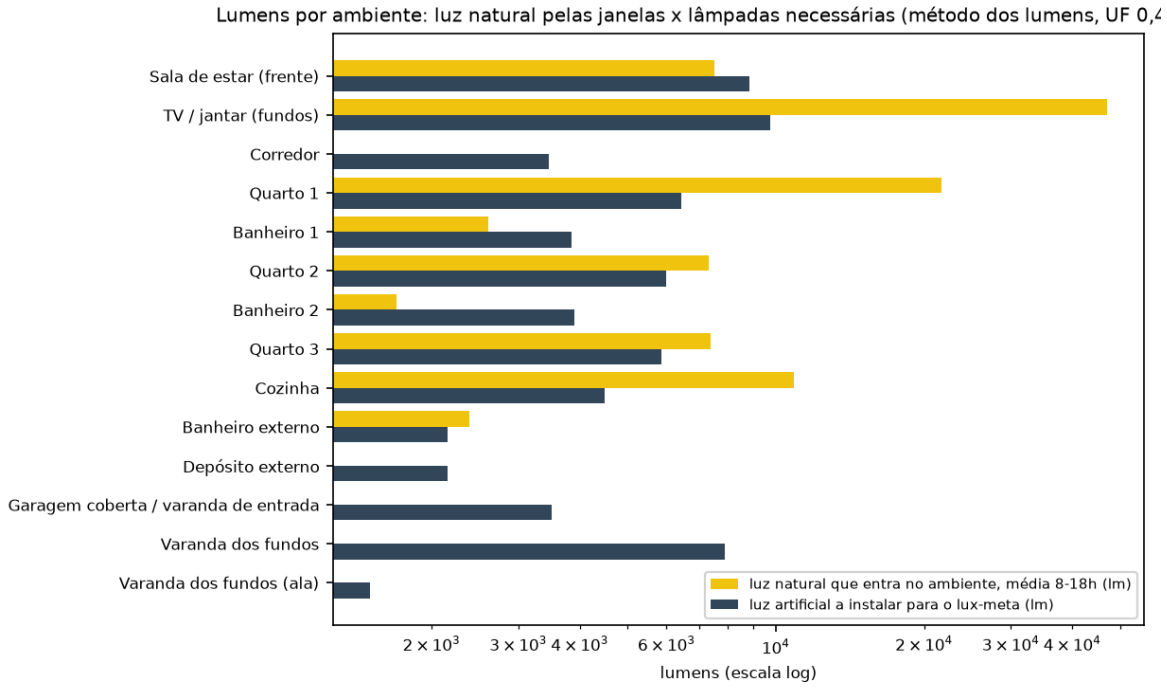

Luz natural que entra pelas janelas (amarelo) comparada com os lumens de lâmpada necessários para a luz-meta (escuro).

4. Janelas, ar fresco e vento

A NBR 15575-4 pede que a parte abrível das janelas seja de pelo menos **7% da área do piso** de cada sala e dormitório, e limita o vidro a 20% do piso, salvo se houver sombreamento. A NBR 15220-3 recomenda a ventilação cruzada pelo vento como principal estratégia de verão para este clima.


4,1 Tamanho das janelas

Ambiente	Piso m²	Vidro m²	Vidro / piso	Abrível / piso
Sala de estar + jantar	44,6	6,64	14,9% Pequena 3/5	7,4% Atende ao mínimo 3/5
Corredor	12,5	0,00	0,0%	0,0%
Quarto 1	15,4	1,44	9,4% Pequena 3/5	4,7% Não atende 1/5
Banheiro 1	9,2	0,36	3,9%	1,9%
Quarto 2	14,4	1,44	10,0% Pequena 3/5	5,0% Não atende 1/5
Banheiro 2	9,4	0,36	3,8%	1,9%
Quarto 3	14,1	1,44	10,2% Pequena 3/5	5,1% Não atende 1/5
Cozinha	10,8	1,80	16,7% Ideal 5/5	8,3% Atende ao mínimo 3/5
Banheiro externo	5,2	0,36	6,9%	3,5%
Depósito externo	5,2	0,00	0,0%	0,0%


Os tamanhos de janela do modelo são medidas comuns de catálogo por volta de 2012 (dormitórios 1,20 x 1,20 m, sala de estar e jantar 2,00 x 1,20 m, cozinha 1,50 x 1,20 m, banheiros 0,60 x 0,60 m), não medições; supõe-se que uma janela de correr abre metade da sua área. Se as janelas reais forem diferentes, altere-as e rode a análise de novo.

4,2 Ventilação cruzada

Ambiente	Horas com vento e corrente de ar atravessando
Sala de estar + jantar	100% Excelente 5/5
Corredor	100%
Quarto 1	100% Excelente 5/5
Banheiro 1	0%
Quarto 2	100% Excelente 5/5
Banheiro 2	0%
Quarto 3	100% Excelente 5/5
Cozinha	100% Excelente 5/5
Banheiro externo	0%
Depósito externo	0%

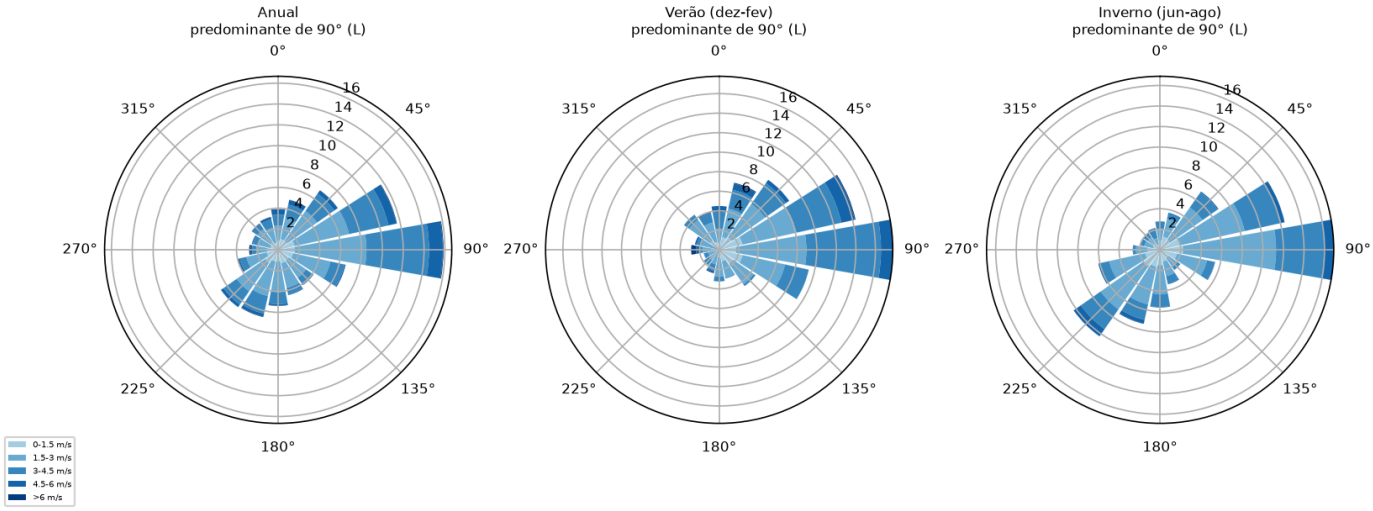

Rosas dos ventos: de onde o vento vem e com que força, ano todo, verão e inverno.

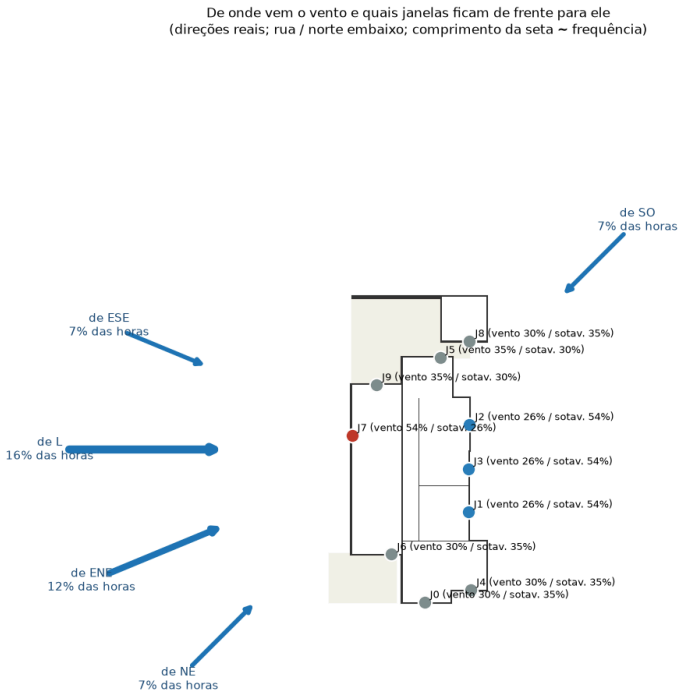

Direções do vento em relação às janelas da casa (janelas vermelhas de frente para o vento, azuis do lado protegido).

O que conta como bom? (janelas e vento)

Área de janela abrível para ventilação Norma brasileira

Área das janelas que realmente abre (descontados vidros, caixilhos e folhas fixas) dividida pela área do piso do ambiente. Nas zonas 1 a 7 é exigido pelo menos 7%.

Não atende 1/5	abaixo de 7 % da área do piso	Menos que os 7% mínimos da norma (a menos que o código de obras do município diga outra coisa).
Atende ao mínimo 3/5	7 a 10 % da área do piso	Atende ao mínimo de 7%.
Boa margem 5/5	10 ou mais % da área do piso	Mais que o mínimo: boas trocas de ar.

Esta casa: Sala de estar + jantar 7,4% Atende ao mínimo 3/5 | Quarto 1 4,7% Não atende 1/5 | Quarto 2 5,0% Não atende 1/5 | Quarto 3 5,1% Não atende 1/5 | Cozinha 8,3% Atende ao mínimo 3/5

Fonte: Projeto de emenda da ABNT NBR 15575-4:2021 (mar/2021): método simplificado para paredes, ventilação e áreas transparentes. Supomos que uma janela de correr abre cerca da metade da sua área; janelas de abrir ou basculantes abrem mais.

Área de vidro em relação ao piso Norma brasileira

Área da janela dividida pela área do piso. A NBR 15575-4 limita as áreas transparentes a 20% do piso (ambientes até 20 m²) a menos que haja sombreamento ou vidro de alto desempenho; a NBR 15220-3 recomenda aberturas de 15 a 25% na zona 3.

Muito pequena 2/5	abaixo de 7 % da área do piso	Janela pequena demais para luz e ar.
Pequena 3/5	7 a 15 % da área do piso	Funciona, mas um pouco escuro ou abafado.
Ideal 5/5	15 a 20 % da área do piso	Dentro do limite da NBR 15575-4 e da recomendação da NBR 15220-3.
Grande 4/5	20 a 25 % da área do piso	Recomendada pela NBR 15220-3 se sombreada; acima dos 20% da NBR 15575-4, exceto se sombreada.
Grande demais 2/5	25 ou mais % da área do piso	Mais calor do sol do que as normas aceitam sem sombreamento.

Esta casa: Sala de estar + jantar 14,9% Pequena 3/5 | Quarto 1 9,4% Pequena 3/5 | Quarto 2 10,0% Pequena 3/5 | Quarto 3 10,2% Pequena 3/5 | Cozinha 16,7% Ideal 5/5

Fonte: Projeto de emenda da ABNT NBR 15575-4:2021 (mar/2021): método simplificado para paredes, ventilação e áreas transparentes; ABNT NBR 15220-3: zoneamento bioclimático brasileiro e diretrizes construtivas (Maringá costuma ser listada na zona 3).

Ventilação cruzada possível Regra prática

Parcela das horas com vento em que o vento bate em uma janela de um lado dos ambientes conectados e outra janela do lado oposto deixa o ar sair (portas supostas abertas).

Quase nenhuma 1/5	abaixo de 5 % das horas com vento	O ar quase não atravessa o ambiente.
Fraca 2/5	5 a 20 % das horas com vento	A ventilação cruzada raramente acontece.
Alguma 3/5	20 a 40 % das horas com vento	Funciona em parte das horas com vento.
Boa 4/5	40 a 60 % das horas com vento	Funciona em muitas horas com vento.
Excelente 5/5	60 ou mais % das horas com vento	Uma corrente de ar atravessando a casa é possível quase sempre.

Esta casa: Sala de estar + jantar 100% Excelente 5/5 | Quarto 1 100% Excelente 5/5 | Quarto 2 100% Excelente 5/5 | Quarto 3 100% Excelente 5/5 | Cozinha 100% Excelente 5/5

Fonte: Regra prática deste estudo (nenhuma norma dá um número).

Velocidade média do vento externo Padrão internacional

Vento médio no local ao longo do ano (arquivo climático, terreno aberto a 10 m; na casa é menor).

Calmaria 2/5	abaixo de 1,0 m/s	Pouca ventilação natural só pelo vento.
Aragem 3/5	1,0 a 2,0 m/s	Suave; as aberturas ajudam, mas a ventilação cruzada é fraca.
Brisa leve a suave 5/5	2,0 a 5,0 m/s	Faixa ideal para ventilação natural.
Brisa moderada 4/5	5,0 a 8,0 m/s	Forte o bastante para exigir proteção contra o vento ao ar livre.
Brisa fresca ou mais 2/5	8,0 ou mais m/s	Risco de danos e desconforto pelo vento.

Esta casa: Maringá, PR, ano todo 2,3 m/s Brisa leve a suave 5/5


Fonte: Escala de vento Beaufort (OMM); Regra prática deste estudo (nenhuma norma dá um número). Beaufort 1 = 0,3–1,5 m/s, 2 = 1,6–3,3, 3 = 3,4–5,4, 4 = 5,5–7,9 m/s. Dentro de casa, a ASHRAE 55 aceita velocidades do ar de até cerca de 0,8 m/s.

5. Temperatura e conforto


Sem ar-condicionado, o conforto depende das paredes, da cobertura, das janelas, da sombra e da ventilação. A simulação calcula a temperatura interna de cada ambiente para cada uma das 8,760 horas de um ano típico. **Confortável** significa dentro da faixa de conforto adaptativo da ASHRAE 55 (ela acompanha o clima: as pessoas aceitam ambientes mais quentes quando faz mais calor lá fora).

5,1 Horas na faixa confortável

Ambiente	Horas confortáveis	Quente demais	Frio demais	Máxima	Mínima
Sala de estar + jantar	7.014 h = 80% Bom 4/5	867 h	879 h	33,8 °C Muito quente 2/5	12,8 °C Frio 2/5
Corredor	8.090 h = 92% Excelente 5/5	0 h	670 h	29,1 °C Morno 4/5	16,5 °C Fresco 3/5
Quarto 1	7.155 h = 82% Bom 4/5	886 h	719 h	33,5 °C Muito quente 2/5	13,0 °C Frio 2/5
Banheiro 1	6.609 h = 75% Bom 4/5	1.223 h	928 h	34,9 °C Muito quente 2/5	11,7 °C Perigoso 1/5
Quarto 2	7.545 h = 86% Bom 4/5	410 h	805 h	32,8 °C Muito quente 2/5	14,0 °C Frio 2/5
Banheiro 2	7.594 h = 87% Bom 4/5	452 h	714 h	32,5 °C Muito quente 2/5	14,4 °C Frio 2/5
Quarto 3	7.561 h = 86% Bom 4/5	391 h	808 h	32,7 °C Muito quente 2/5	14,0 °C Frio 2/5
Cozinha	6.558 h = 75% Aceitável 3/5	1.113 h	1.089 h	35,1 °C Extremo 1/5	11,5 °C Perigoso 1/5
Banheiro externo	6.403 h = 73% Aceitável 3/5	1.539 h	818 h	35,1 °C Extremo 1/5	11,5 °C Perigoso 1/5
Depósito externo	6.510 h = 74% Aceitável 3/5	1.238 h	1.012 h	35,0 °C Extremo 1/5	11,3 °C Perigoso 1/5
AO AR LIVRE (referência)	4.248 h = 48% Ruim 2/5	1.193 h	3.319 h	37,7 °C	4,2 °C

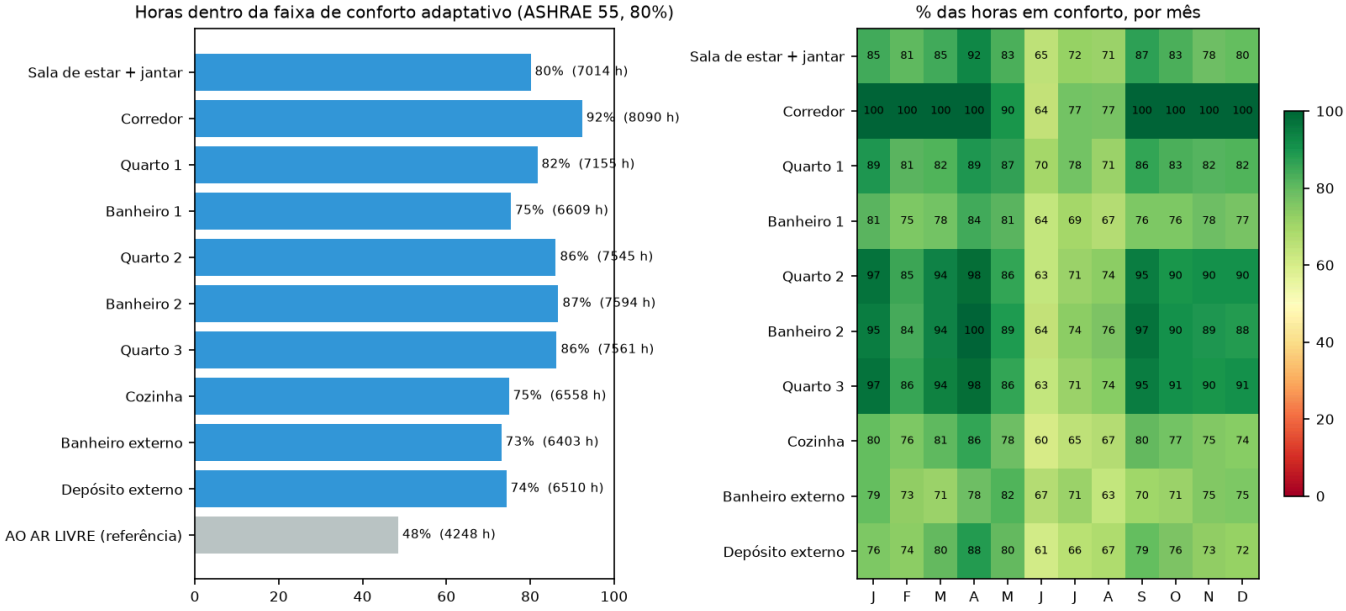

Esquerda: horas confortáveis por ambiente. Direita: parcela de horas confortáveis por mês (verde = bom, vermelho = ruim).

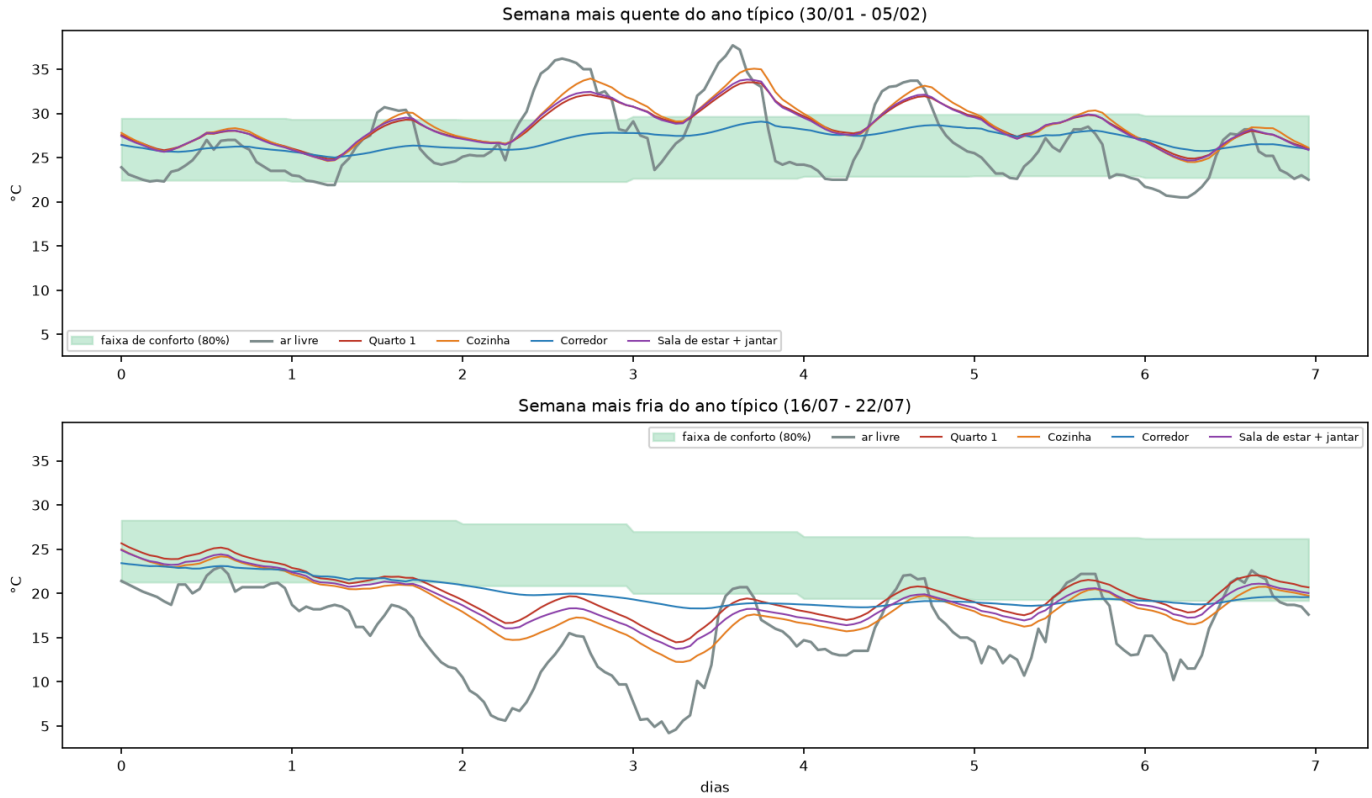

Uma semana quente e uma semana fria: temperaturas internas contra a faixa de conforto e a temperatura externa.

5,2 Verificação brasileira de dia de projeto (NBR 15575)

Dia mais quente do ano típico: **02 Fev** (37,7 °C lá fora). Dia mais frio: **19 Jul** (4,2 °C lá fora).


Ambiente	Dia mais quente: máxima interna	vs. externo	Veredito	Dia mais frio: mínima interna	vs. externo	Veredito
Sala de estar + jantar	34,0 °C	-3,7	Intermediário 4/5	13,5 °C	+9,3	Superior 5/5
Corredor *(não avaliado)*	29,0 °C	-8,7		18,3 °C	+14,1	
Quarto 1	33,6 °C	-4,1	Superior 5/5	14,3 °C	+10,1	Superior 5/5
Banheiro 1 *(não avaliado)*	35,0 °C	-2,7		12,4 °C	+8,2	
Quarto 2	32,8 °C	-4,9	Superior 5/5	14,9 °C	+10,7	Superior 5/5
Banheiro 2 *(não avaliado)*	32,5 °C	-5,2		15,6 °C	+11,4	
Quarto 3	32,8 °C	-4,9	Superior 5/5	15,0 °C	+10,8	Superior 5/5
Cozinha *(não avaliado)*	35,1 °C	-2,6		12,0 °C	+7,8	
Banheiro externo *(não avaliado)*	35,1 °C	-2,6		12,6 °C	+8,4	
Depósito externo *(não avaliado)*	35,0 °C	-2,7		12,0 °C	+7,8	

A edição mais nova (NBR 15575-1:2021) compara a casa com uma casa de referência ao longo do ano todo; isso exige uma segunda simulação, por isso este relatório usa os critérios absolutos clássicos de dia de projeto, que são mais fáceis de entender.

5,3 Quanto custa refrigerar os ambientes no verão

Se um ambiente esquenta demais, dá para refrigerá-lo com ar-condicionado. A simulação liga um split sempre que o ambiente passa de **26 °C** nas horas em que é usado (dormitórios: 21:00-08:00, sala: 14:00-23:00, cozinha: 08:00-21:00), com as janelas fechadas, e soma a eletricidade: calor retirado ÷ COP 3,0 (um modelo inverter faz melhor) × tarifa de **R$ 1,00 por kWh** (com todos os impostos; uma suposição baseada na tarifa residencial da Copel após o reajuste de +20% de junho de 2026; altere com *run_all.bat --tariff 0,95*).

Ambiente	Quando é climatizado	Horas com o ar ligado	Eletricidade kWh/ano	Custo R$/ano	Custo dez-fev	Pior mês	Pico de calor a retirar	Capacidade do ar	Nível
Sala de estar + jantar (44,6 m²)	14:00-23:00	1640	858	**R$ 858**	R$ 373	Dez (R$ 133)	5,8 kW	24.000 BTU/h	Baixa 4/5
Quarto 1 (15,4 m²)	21:00-08:00	975	154	**R$ 154**	R$ 66	Fev (R$ 25)	1,9 kW	9.000 BTU/h	Baixa 4/5
Quarto 2 (14,4 m²)	21:00-08:00	878	112	**R$ 112**	R$ 53	Fev (R$ 21)	1,6 kW	9.000 BTU/h	Muito baixa 5/5
Quarto 3 (14,1 m²)	21:00-08:00	874	109	**R$ 109**	R$ 51	Fev (R$ 20)	1,5 kW	9.000 BTU/h	Muito baixa 5/5
Cozinha (10,8 m²)	08:00-21:00	2161	364	**R$ 364**	R$ 160	Dez (R$ 57)	1,5 kW	9.000 BTU/h	Moderada 3/5
Total			**1.597**	**R$ 1.597**					

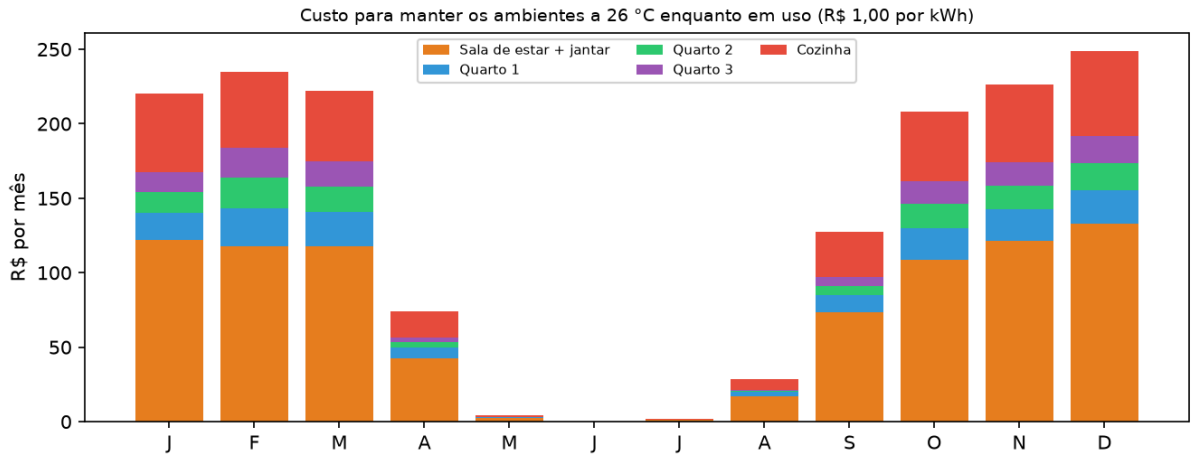

Custo mensal de climatização por ambiente.

"Pico de calor a retirar" é a potência de refrigeração necessária na hora mais quente; a capacidade do ar soma 10% e arredonda para um tamanho de catálogo (1 kW = 3,412 BTU/h). Só o calor sensível é contado (sem desumidificação), então as contas reais são um pouco maiores. Os ambientes com nível Alta ou Muito alta são onde sombra, uma cobertura melhor ou melhor isolamento se pagam mais rápido.

O que conta como bom? (temperatura, refrigeração e aquecimento)

Horas na faixa de temperatura confortável

Regra prática

Parcela das 8,760 horas do ano em que a temperatura do ambiente fica dentro da faixa de conforto adaptativo da ASHRAE 55 (ela acompanha o clima: com mais calor lá fora, aceita-se mais calor dentro). Ao ar livre, como referência, só cerca de metade das horas.

Péssimo 1/5	abaixo de 40 % do ano	Desconfortável na maior parte do ano.
Ruim 2/5	40 a 60 % do ano	Desconfortável em boa parte do ano.
Aceitável 3/5	60 a 75 % do ano	Confortável na maior parte do tempo, com algumas ondas de calor ou frio.
Bom 4/5	75 a 90 % do ano	Confortável na maior parte do ano.
Excelente 5/5	90 ou mais % do ano	Confortável quase o ano todo sem ar-condicionado nem aquecimento.

Esta casa: Sala de estar + jantar 80% Bom 4/5 | Corredor 92% Excelente 5/5 | Quarto 1 82% Bom 4/5 | Banheiro 1 75% Bom 4/5 | Quarto 2 86% Bom 4/5 | Banheiro 2 87% Bom 4/5 | Quarto 3 86% Bom 4/5 | Cozinha 75% Aceitável 3/5 | Banheiro externo 73% Aceitável 3/5 | Depósito externo 74% Aceitável 3/5 | AO AR LIVRE (referência) 48% Ruim 2/5

Fonte: ASHRAE 55, modelo de conforto adaptativo (aceitabilidade de 80% / 90%); Regra prática deste estudo (nenhuma norma dá um número). As normas avaliam o conforto térmico em relação a uma casa de referência ou em dias de projeto; esta escala em porcentagem é nossa.

Dia mais quente: máxima interna x máxima externa (NBR 15575)

Norma brasileira

No dia mais quente do ano típico, a maior temperatura do ar interno comparada com a maior temperatura externa. Negativo significa que a casa fica mais fresca que o lado de fora.

Superior 5/5	abaixo de -4 °C (máx. interna − máx. externa)	Máxima interna pelo menos 4 °C abaixo da externa.
Intermediário 4/5	-4 a -2 °C (máx. interna − máx. externa)	Máxima interna pelo menos 2 °C abaixo da externa.
Mínimo 3/5	-2 a 0,0001 °C (máx. interna − máx. externa)	Máxima interna não maior que a externa.
Não atende 1/5	0,0001 ou mais °C (máx. interna − máx. externa)	Máxima interna maior que a externa: a casa superaquece.

Esta casa: Sala de estar + jantar -3,7 °C Intermediário 4/5 | Quarto 1 -4,1 °C Superior 5/5 | Quarto 2 -4,9 °C Superior 5/5 | Quarto 3 -4,9 °C Superior 5/5

Fonte: ABNT NBR 15575-1:2013 (Edificações habitacionais — Desempenho), requisitos de iluminação natural e desempenho térmico. Vale para dormitórios e salas. Usamos o dia mais quente do arquivo climático, não o dia típico de projeto da norma.

Dia mais frio: mínima interna x mínima externa (NBR 15575)

Norma brasileira

No dia mais frio do ano típico, a menor temperatura do ar interno comparada com a menor temperatura externa. Positivo significa que a casa fica mais quente que o lado de fora.

Não atende 1/5	abaixo de 3 °C (mín. interna − mín. externa)	Menos de 3 °C mais quente que o lado de fora.
Mínimo 3/5	3 a 5 °C (mín. interna − mín. externa)	Pelo menos 3 °C mais quente que o lado de fora.
Intermediário 4/5	5 a 7 °C (mín. interna − mín. externa)	Pelo menos 5 °C mais quente que o lado de fora.
Superior 5/5	7 ou mais °C (mín. interna − mín. externa)	Pelo menos 7 °C mais quente que o lado de fora.

Esta casa: Sala de estar + jantar +9,3 °C Superior 5/5 | Quarto 1 +10,1 °C Superior 5/5 | Quarto 2 +10,7 °C Superior 5/5 | Quarto 3 +10,8 °C Superior 5/5

Fonte: ABNT NBR 15575-1:2013 (Edificações habitacionais — Desempenho), requisitos de iluminação natural e desempenho térmico. A verificação de inverno é exigida nas zonas bioclimáticas 1 a 5, o que inclui Maringá.

Hora mais quente do ano dentro de casa

Regra prática

Maior temperatura operativa (ar + superfícies das paredes) atingida no ambiente.

Confortável 5/5	abaixo de 28 °C	Nunca fica realmente quente.
Morno 4/5	28 a 30 °C	Quente nos dias mais quentes; um ventilador resolve.
Quente 3/5	30 a 32 °C	Períodos quentes; ventilador ajuda, o sono é afetado.
Muito quente 2/5	32 a 35 °C	Risco de estresse térmico para crianças e idosos.
Extremo 1/5	35 ou mais °C	Perigoso sem climatização.

Esta casa: Sala de estar + jantar 33,8 °C Muito quente 2/5 | Corredor 29,1 °C Morno 4/5 | Quarto 1 33,5 °C Muito quente 2/5 | Banheiro 1 34,9 °C Muito quente 2/5 | Quarto 2 32,8 °C Muito quente 2/5 | Banheiro 2 32,5 °C Muito quente 2/5 | Quarto 3 32,7 °C Muito quente 2/5 | Cozinha 35,1 °C Extremo 1/5 | Banheiro externo 35,1 °C Extremo 1/5 | Depósito externo 35,0 °C Extremo 1/5

Fonte: ASHRAE 55, modelo de conforto adaptativo (aceitabilidade de 80% / 90%); Regra prática deste estudo (nenhuma norma dá um número). O limite superior do conforto adaptativo em um mês quente é cerca de 29 °C (aceitabilidade de 80%).

Hora mais fria do ano dentro de casa Padrão internacional

Menor temperatura operativa atingida no ambiente.

Perigoso 1/5	abaixo de 12 °C	Estresse por frio; risco de problemas cardíacos e respiratórios.
Frio 2/5	12 a 16 °C	Abaixo de 16 °C o risco de problemas respiratórios aumenta.
Fresco 3/5	16 a 18 °C	Precisa de agasalho; abaixo dos 18 °C recomendados pela OMS.
Bom 4/5	18 a 20 °C	Atende à recomendação da OMS de pelo menos 18 °C.
Agradável 5/5	20 ou mais °C	Nunca fica desconfortavelmente frio.

Esta casa: Sala de estar + jantar 12,8 °C Frio 2/5 | Corredor 16,5 °C Fresco 3/5 | Quarto 1 13,0 °C Frio 2/5 | Banheiro 1 11,7 °C Perigoso 1/5 | Quarto 2 14,0 °C Frio 2/5 | Banheiro 2 14,4 °C Frio 2/5 | Quarto 3 14,0 °C Frio 2/5 | Cozinha 11,5 °C Perigoso 1/5 | Banheiro externo 11,5 °C Perigoso 1/5 | Depósito externo 11,3 °C Perigoso 1/5

Fonte: OMS, Diretrizes de Habitação e Saúde 2018 (temperatura interna de pelo menos 18 °C).

Eletricidade para manter o ambiente fresco com ar-condicionado Regra prática

Eletricidade que um split usaria em um ano para manter o ambiente a 26 °C (limite superior da zona de conforto de verão da NBR 16401-2) nas horas em que ele é usado (dormitórios 21h–8h, sala 14h–23h, cozinha 8h–21h). Um ambiente que superaquece no verão custa mais aqui. Custo = kWh × tarifa.

Muito baixa 5/5	abaixo de 10 kWh por m² por ano	Raramente precisa de refrigeração.
Baixa 4/5	10 a 25 kWh por m² por ano	Algumas semanas de refrigeração por ano.
Moderada 3/5	25 a 45 kWh por m² por ano	Refrigeração necessária na maior parte do verão.
Alta 2/5	45 a 70 kWh por m² por ano	Caro para manter fresco: o ambiente superaquece muito.
Muito alta 1/5	70 ou mais kWh por m² por ano	Muito caro: sombreamento, isolamento ou uma cobertura melhor valem mais que um ar-condicionado maior.

Esta casa: Sala de estar + jantar 19,2 kWh/m² Baixa 4/5 | Quarto 1 10,0 kWh/m² Baixa 4/5 | Quarto 2 7,8 kWh/m² Muito baixa 5/5 | Quarto 3 7,7 kWh/m² Muito baixa 5/5 | Cozinha 33,7 kWh/m² Moderada 3/5

Fonte: Regra prática deste estudo (nenhuma norma dá um número); ABNT NBR 16401-2 (ar-condicionado, conforto interno): verão cerca de 22,5–25,5 °C com 65% de UR e 23–26 °C com 35% de UR. Considera COP 3,0 (split classe A do Inmetro de cerca de 2012), janelas fechadas com o ar ligado e só calor sensível (sem desumidificação); portanto as contas reais são um pouco maiores. A tarifa é uma suposição; veja o relatório.


6. Sol por fora, paredes e cobertura

Nesta latitude o sol do meio-dia fica sempre na metade norte do céu, então as paredes voltadas para o norte recebem o sol de inverno (bom) e pouco sol de verão, enquanto as paredes leste e oeste recebem muito sol de verão (ruim).

6,1 Energia solar em cada superfície (kWh por m², sem sombra)

Superfície	Ano todo	Verão (dez-fev)	Inverno (jun-ago)
Parede norte	1066	155 Moderado 4/5	356 Alto 5/5
Parede leste	1004	287 Alto 3/5	204 Moderado 3/5
Parede sul	507	179 Moderado 4/5	86 Baixo 2/5
Parede oeste	982	279 Alto 3/5	191 Moderado 3/5
Cobertura (horizontal)	1865	536	351


Trajetória do sol - Maringá, PR (lat -23.4°): ao meio-dia o sol está sempre na metade norte do céu

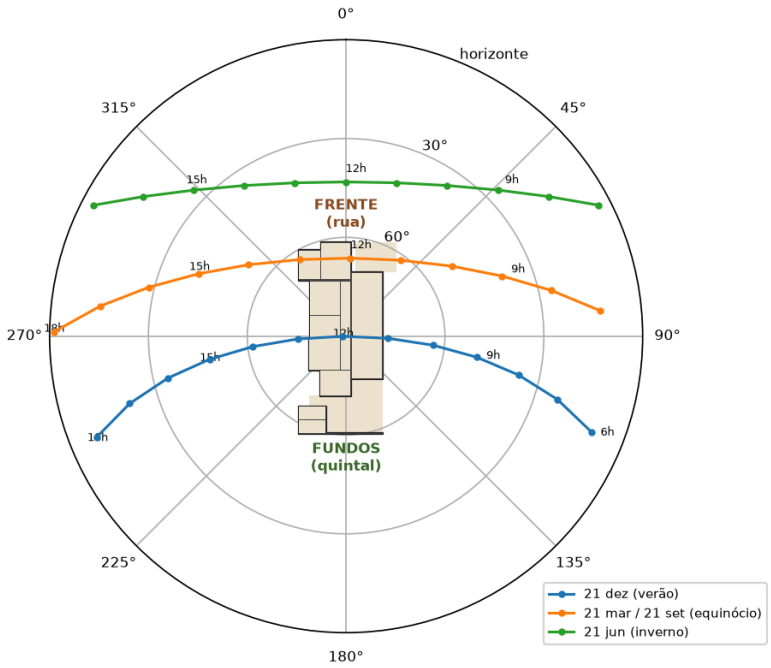

A planta da casa está desenhada no centro, na orientação real; o tamanho dela não está em escala com os ângulos do céu.

Trajetória do sol ao longo do ano com a casa desenhada no centro, na orientação real: a frente (rua) é voltada para o norte e os fundos para o sul.

Quais paredes recebem sol? Direções reais da bússola.

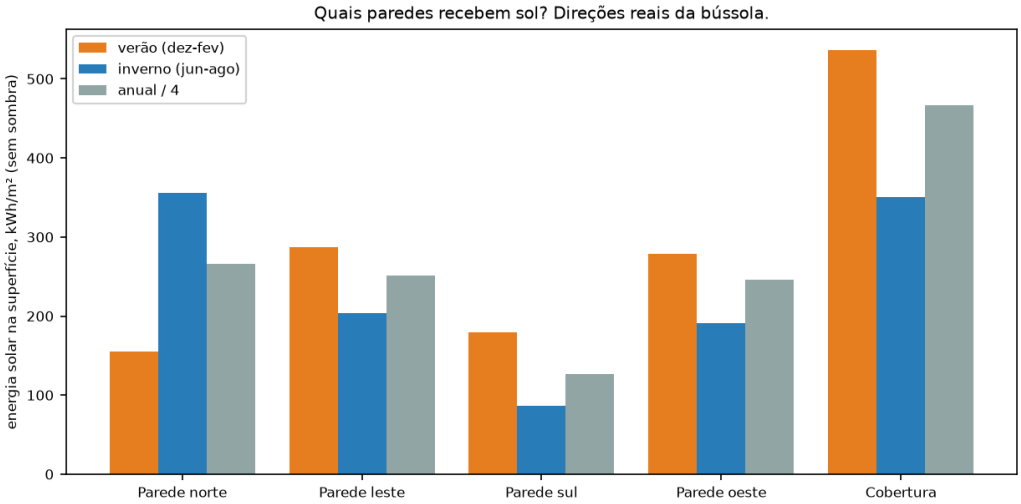

Energia solar em cada parede por estação.

6,2 As paredes e a cobertura atendem à NBR 15575?

Item	Esta casa	Limite (NBR 15575)	Resultado
Transmitância térmica U da parede externa Bloco cerâmico furado de 8 furos 9x19x19 cm + 2 cm de reboco nos dois lados = parede de 13 cm (bloco padrão brasileiro) (absortância da pintura / cobertura 0,45)	2,52 W/m²K	<= 3,7	atende
Capacidade térmica da parede externa Bloco cerâmico furado de 8 furos 9x19x19 cm + 2 cm de reboco nos dois lados = parede de 13 cm (bloco padrão brasileiro) (absortância da pintura / cobertura 0,45)	134 kJ/m²K	>= 130	atende
Transmitância térmica U da cobertura (indicativa) Telha cerâmica + sótão ventilado + laje de concreto de 12 cm (absortância da pintura / cobertura 0,7)	1,78 W/m²K	<= 1,5	não atende

6,3 E se os materiais mudarem?

Numa casa pronta é muito difícil trocar as paredes, mas a cobertura muitas vezes pode ser melhorada; por isso as duas são mostradas separadamente (cada uma com a outra parte mantida como é hoje). Melhorias de cobertura, como lã isolante, estão na seção 7.

Paredes


Cobertura mantida: Clay tile + ventilated attic + 12 cm concrete slab ceiling

Paredes	Média de horas confortáveis	Quente demais	Frio demais	Conta de resfriamento	vs. atual
Tijolo cerâmico furado de 14 cm + 2 cm de reboco nos dois lados = parede de 18 cm (mais espessa, "tijolo 6 furos em pé")	7.357 h = 84% Bom 4/5	628 h	775 h	R$ 1.372/ano	R$ -224/ano
Bloco de concreto de 14 cm + 1,5 cm de reboco nos dois lados = parede de 17 cm	7.284 h = 83% Bom 4/5	696 h	780 h	R$ 1.558/ano	R$ -38/ano
Bloco cerâmico furado de 8 furos 9x19x19 cm + 2 cm de reboco nos dois lados = parede de 13 cm (bloco padrão brasileiro) **(atual)**	7.104 h = 81% Bom 4/5	812 h	844 h	R$ 1.596/ano	-

Cobertura / forro

Paredes mantidas: Ceramic hollow brick 8-hole 9x19x19 cm + 2 cm plaster both sides = 13 cm wall (standard Brazilian block)

Cobertura / forro	Média de horas confortáveis	Quente demais	Frio demais	Conta de resfriamento	vs. atual
Telha cerâmica + sótão ventilado + laje de concreto de 12 cm **(atual)**	7.104 h = 81% Bom 4/5	812 h	844 h	R$ 1.596/ano	-
Telha de fibrocimento + sótão + forro de PVC (cobertura leve)	6.414 h = 73% Aceitável 3/5	1.182 h	1.165 h	R$ 1.813/ano	+R$ 217/ano
Telha cerâmica + sótão ventilado + forro de gesso	6.306 h = 72% Aceitável 3/5	1.303 h	1.151 h	R$ 1.973/ano	+R$ 377/ano

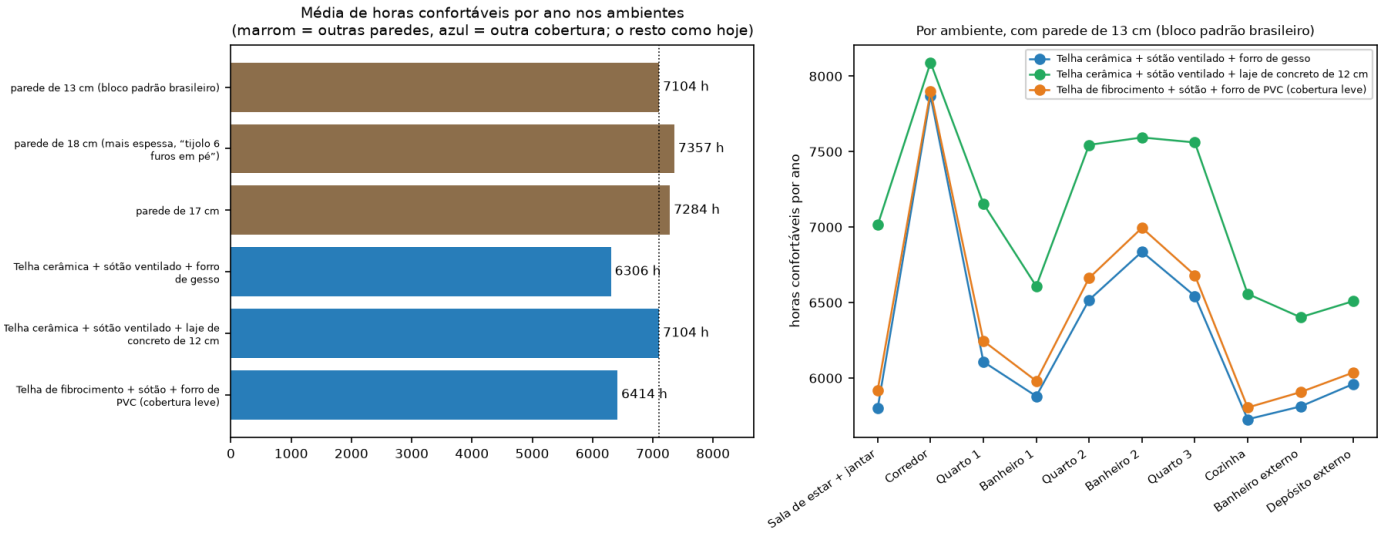

Horas confortáveis com paredes e coberturas diferentes.

O que conta como bom? (sol e construção)

Sol de verão na parede Regra prática

Energia solar em uma parede vertical sem sombra nos três meses de verão (dez–fev no sul, jun–ago no norte). Quanto menor, melhor: é calor que você não quer.

Baixo 5/5	abaixo de 150 kWh/m²	Pouco calor do sol no verão.
Moderado 4/5	150 a 225 kWh/m²	Algum calor; um beiral ou cor clara resolvem.
Alto 3/5	225 a 300 kWh/m²	Parede quente: precisa de sombra, cor clara ou isolamento.
Muito alto 2/5	300 ou mais kWh/m²	Parede muito quente.

Esta casa: Parede norte 155 Moderado 4/5 | Parede leste 287 Alto 3/5 | Parede sul 179 Moderado 4/5 | Parede oeste 279 Alto 3/5

Fonte: Regra prática deste estudo (nenhuma norma dá um número). Aproximadamente 1,7 / 2,5 / 3,3 kWh/m² por dia. A norma trata o calor das paredes por limites de transmitância térmica e cor da pintura.

Sol de inverno na parede Regra prática

Energia solar em uma parede vertical nos três meses de inverno (jun–ago no sul, dez–fev no norte). Quanto maior, melhor em um inverno fresco: calor de graça (a NBR 15220-3 recomenda aquecimento solar passivo no inverno para a zona 3).

Baixo 2/5	abaixo de 120 kWh/m²	Quase nenhum sol no inverno.
Moderado 3/5	120 a 220 kWh/m²	Algum sol no inverno.
Bom 4/5	220 a 320 kWh/m²	Bom sol no inverno.
Alto 5/5	320 ou mais kWh/m²	Muito calor grátis no inverno.

Esta casa: Parede norte 356 Alto 5/5 | Parede leste 204 Moderado 3/5 | Parede sul 86 Baixo 2/5 | Parede oeste 191 Moderado 3/5

Fonte: Regra prática deste estudo (nenhuma norma dá um número); ABNT NBR 15220-3: zoneamento bioclimático brasileiro e diretrizes construtivas (Maringá costuma ser listada na zona 3).

Transmitância térmica U da parede (NBR 15575-4) Norma brasileira

Com que rapidez o calor atravessa a parede (menor = mais isolada). Limite nas zonas 3 a 8: 3,7 se a pintura externa for clara (absortância solar até 0,6) e 2,5 se for mais escura.

Atende aos dois limites 5/5	abaixo de 2,5 W/m²K	Atende ao limite mesmo com pintura escura.
Só com pintura clara 4/5	2,5 a 3,7 W/m²K	Atende ao limite apenas com pintura de cor clara (absortância 0,6 ou menos).
Não atende 1/5	3,7 ou mais W/m²K	Acima do limite: o método simplificado não é atendido.

Esta casa: Transmitância térmica U da parede externa 2,52 (limite <= 3,7) Só com pintura clara 4/5

Fonte: Projeto de emenda da ABNT NBR 15575-4:2021 (mar/2021): método simplificado para paredes, ventilação e áreas transparentes.

Capacidade térmica da parede (NBR 15575-4) Norma brasileira

Quanto calor a parede armazena (maior = temperatura interna mais estável). Limite: pelo menos 130 nas zonas 1 a 7.

Não atende 1/5	abaixo de 130 kJ/m²K	Menos armazenamento de calor que o mínimo.
Atende 5/5	130 ou mais kJ/m²K	Atende ao mínimo de 130.

Esta casa: Capacidade térmica da parede externa 134 (limite >= 130) Atende 5/5

Fonte: Projeto de emenda da ABNT NBR 15575-4:2021 (mar/2021): método simplificado para paredes, ventilação e áreas transparentes.

Transmitância térmica U da cobertura (NBR 15575-5) Norma brasileira

Fluxo de calor pela cobertura + forro. Limite nas zonas 3 a 6: 2,3 se a cobertura for clara (absortância até 0,6) e 1,5 se for escura (por exemplo, telha cerâmica vermelha).

Atende aos dois limites 5/5	abaixo de 1,5 W/m²K	Atende ao limite mesmo para cobertura escura.
Só cobertura clara 4/5	1,5 a 2,3 W/m²K	Atende ao limite apenas se a superfície da cobertura for clara.
Não atende 1/5	2,3 ou mais W/m²K	Acima do limite.

Esta casa: Transmitância térmica U da cobertura (indicativa) 1,78 (limite <= 1,5) Só cobertura clara 4/5


Fonte: Projeto de emenda da ABNT NBR 15575-5:2021: método simplificado para coberturas. O U da nossa cobertura é indicativo: o cálculo padrão não modela um sótão ventilado.

7. Melhorias: isolamento, vedação, vidro e sombreamento

Cada melhoria abaixo é simulada no ano inteiro e comparada com a casa como ela é hoje. A **lã no telhado** fica sobre o forro (lado do sótão); a **vedação** são borrachas e escovas nas esquadrias e portas; o **vidro duplo** substitui o vidro simples; o **brise fixo** é uma projeção horizontal sobre cada janela; as **persianas móveis** fecham sozinhas no modelo quando o sol na janela é forte. A última linha combina as principais medidas.

7,1 Resultados por melhoria

Melhoria	O que é	Horas confortáveis	Horas quente demais	Hora mais quente	Resfriamento R$/ano	Variação na conta	Luz natural
Situação atual	Casa existente	83,9% Bom 4/5	553 h	32,3 °C	R$ 1.596	R$ 0/ano	100%
Lã de rocha 50 mm	Lã de rocha 50 mm	88,9% Bom 4/5	308 h	30,6 °C	R$ 966	R$ -630/ano	100%
Lã de vidro 50 mm	Lã de vidro 50 mm	89,1% Bom 4/5	303 h	30,5 °C	R$ 951	R$ -645/ano	100%
Lã de PET 50 mm	Lã de PET (garrafas recicladas) 50 mm	89,0% Bom 4/5	304 h	30,5 °C	R$ 950	R$ -646/ano	100%
Lã de ovelha 50 mm	Lã de ovelha 50 mm	89,0% Bom 4/5	304 h	30,5 °C	R$ 950	R$ -646/ano	100%
Lã de rocha 100 mm	Lã de rocha 100 mm	89,5% Bom 4/5	281 h	30,3 °C	R$ 868	R$ -728/ano	100%
Vedação das esquadrias	Borrachas e escovas de vedação nas esquadrias e portas	84,1% Bom 4/5	551 h	32,3 °C	R$ 1.586	R$ -10/ano	100%
Vidro duplo	Vidro duplo incolor	84,3% Bom 4/5	547 h	32,3 °C	R$ 1.544	R$ -52/ano	89%
Vidro duplo low-E	Vidro duplo low-E	84,5% Bom 4/5	517 h	32,1 °C	R$ 1.416	R$ -180/ano	80%
Brise fixo 0,6 m	Brise horizontal fixo 0,6 m	84,0% Bom 4/5	547 h	32,3 °C	R$ 1.586	R$ -10/ano	100%
Persianas móveis	Persianas / venezianas móveis (fechadas com sol forte)	83,9% Bom 4/5	546 h	32,3 °C	R$ 1.584	R$ -12/ano	100%
Tudo junto	Lã de rocha 50 mm; Borrachas e escovas de vedação nas esquadrias e portas; Vidro duplo low-E; Brise horizontal fixo 0,6 m; Persianas / venezianas móveis (fechadas com sol forte)	89,4% Bom 4/5	289 h	30,3 °C	R$ 764	R$ -832/ano	80%

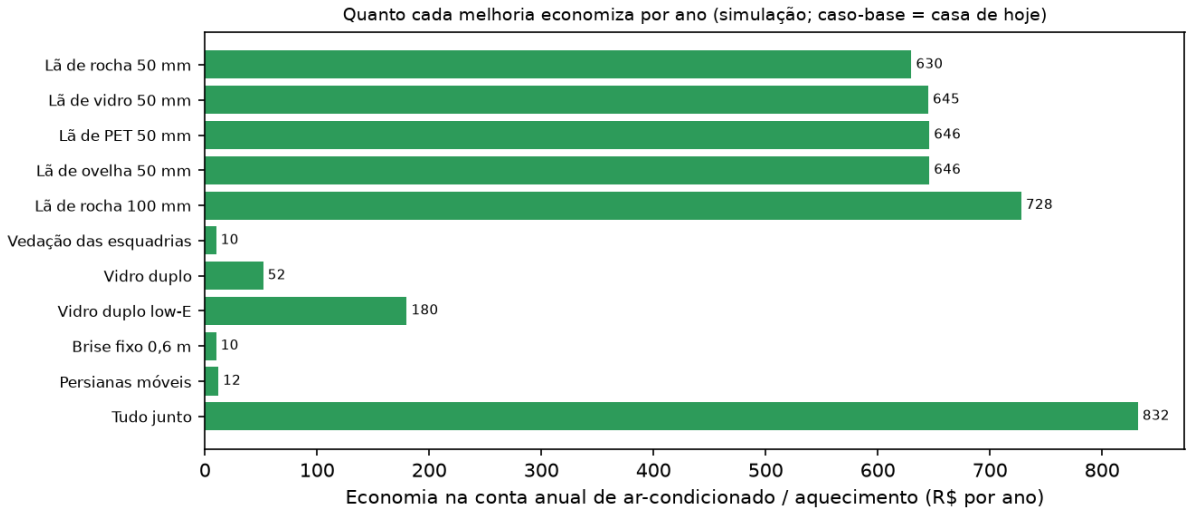

7,2 Qual lã e que espessura? (variação na conta anual e média de horas confortáveis)

Lã	25 mm	50 mm	75 mm	100 mm	150 mm
Lã de vidro λ 0,040 W/m·K	R$ -515 88,2%	R$ -645 89,1%	R$ -704 89,4%	R$ -738 89,6%	R$ -774 89,8%
Lã de rocha λ 0,044 W/m·K	R$ -495 88,0%	R$ -630 88,9%	R$ -692 89,3%	R$ -728 89,5%	R$ -765 89,6%
Lã de PET (garrafas recicladas) λ 0,040 W/m·K	R$ -515 88,2%	R$ -646 89,0%	R$ -704 89,4%	R$ -738 89,6%	R$ -773 89,7%
Lã de ovelha λ 0,040 W/m·K	R$ -515 88,2%	R$ -646 89,0%	R$ -704 89,4%	R$ -738 89,6%	R$ -772 89,7%

Negativo = economia por ano. Mais lã sempre ajuda, com retorno decrescente: os primeiros 50 mm dão a maior parte do benefício. As lãs diferem pouco na condutividade; a escolha costuma depender de preço, comportamento ao fogo, manuseio e umidade.

7,3 Valores usados e quão confiáveis são

Medida	Valor usado	Confiança no valor	Fonte
Lã de vidro	λ 0,040 W/m·K, ρ 15 kg/m³	típico	range 0,030-0,046 W/mK (Saint-Gobain, wool insulation comparison); mid-range value
Lã de rocha	λ 0,044 W/m·K, ρ 40 kg/m³	verificado	Rockwool datasheet (panel, 0,044 W/mK at 50 C, EN 12667)
Lã de PET (garrafas recicladas)	λ 0,040 W/m·K, ρ 30 kg/m³	suposição	typical manufacturer range 0,037-0,041 W/mK; check the product you buy
Lã de ovelha	λ 0,040 W/m·K, ρ 25 kg/m³	suposição	typical range 0,038-0,042 W/mK; check the product you buy
Vidro simples (existente)	U 5,8 W/m²K, g 0,85, VT 0,88	verificado	5,8 W/m2K is the single-glass limit of EN 673 / ISO 10077
Vidro duplo incolor	U 2,8 W/m²K, g 0,76, VT 0,78	típico	typical catalogue values for 4-12-4 clear double glazing (EN 673 / NFRC ranges)
Vidro duplo low-E	U 1,8 W/m²K, g 0,40, VT 0,70	típico	typical catalogue values for low-E (solar control) double glazing
Borrachas e escovas de vedação nas esquadrias e portas	trocas de ar com a casa fechada −25%	suposição	AIVC: weatherstripping alone cuts house air change 10-14,7%, a full retrofit up to 27,5%; 25% used for frames and doors
Brise horizontal fixo	profundidade definida por pacote	suposição	analytic profile-angle shading of the window (sun-path geometry, pvlib); depth in metres from project.json
Persianas / venezianas móveis (fechadas com sol forte)	ganho fechado x0,3	suposição	external blinds let through about 10-30% of solar gain when closed; closed when direct sun on the window exceeds 250 W/m2 (08-18 h)

Os preços das melhorias não estão incluídos: com um orçamento, divida-o pela economia anual para obter o tempo de retorno. Coluna de luz natural: parcela da luz natural que ainda entra (só a transmitância do vidro; persianas e brise não são aplicados à luz natural).

7,4 Conferência com um motor de referência (EnergyPlus)

Todos os pacotes acima foram recalculados com o **EnergyPlus** (Departamento de Energia dos EUA), motor de código aberto validado pela norma ASHRAE 140 e usado dentro do DesignBuilder e do OpenStudio. Ele resolve o balanço de calor de cada superfície com funções de transferência de condução, compartilha as paredes entre os ambientes, modela o forro ventilado acima de cada ambiente, sombreia as janelas com os beirais reais e usa ventilação por vento e empuxo térmico (janelas 50% abertas quando o ar externo está mais frio e acima de 18 °C). O ar-condicionado mantém o mesmo ponto de ajuste, horários e COP do motor rápido. Nenhum dos dois motores considera ganhos internos (pessoas, lâmpadas, aparelhos).

Pacote	Conforto % sem ar-cond. (EnergyPlus)	Ar-cond. kWh/ano rápido	Ar-cond. kWh/ano EnergyPlus	Economia/ano EnergyPlus
Situação atual	76,4	1.596	817	-
Lã de rocha 50 mm	82,4	966	389	R$ 428
Lã de vidro 50 mm	82,5	951	380	R$ 437
Lã de PET 50 mm	82,5	950	380	R$ 437
Lã de ovelha 50 mm	82,5	950	380	R$ 437
Lã de rocha 100 mm	82,8	868	335	R$ 482
Vedação das esquadrias	76,8	1.586	813	R$ 4
Vidro duplo	76,8	1.544	799	R$ 18
Vidro duplo low-E	76,9	1.416	752	R$ 65
Brise fixo 0,6 m	76,5	1.586	814	R$ 3
Persianas móveis	76,4	1.584	796	R$ 21
Tudo junto	82,1	764	309	R$ 508

Resultado com o EnergyPlus: caso base: 76,4% das horas na zona de conforto (motor rápido 81,1%), 651 horas de calor (rápido 814), 1420 horas de frio (rápido 845); ar-condicionado 817 kWh/ano (rápido 1.596). Os dois motores concordam na ordem: **isolar a cobertura é de longe a melhor medida**; vidro e sombreamento mudam pouco.

Diferenças entre os motores são esperadas: o EnergyPlus dá cerca de metade da energia de ar-condicionado do motor rápido e mais horas de frio (ele acopla o piso ao solo e perde calor pelo forro com mais liberdade). Para decisões, prefira os números do EnergyPlus; o motor rápido continua útil para simulações rápidas de hipóteses. Ainda não modelados: ganhos internos, abertura de portas, a inclinação do telhado (usa-se um telhado plano com o mesmo volume de forro) e a sombra dos vizinhos.

8. Classificação de luz natural para construção sustentável (LEED / IES LM-83)

O LEED é a certificação de construção sustentável mais usada no mundo. O crédito de luz natural (v4,1, Opção 1) é dado a partir do **sDA300/50%** simulado (parcela do piso de permanência que recebe 300 lux em pelo menos metade das horas de uso) e do **ASE1000,250** (parcela do piso com mais de 1,000 lux de sol direto por mais de 250 horas por ano, risco de ofuscamento e superaquecimento), ambos definidos na norma IES LM-83 (edição atual LM-83-23, fevereiro de 2023). Degraus: sDA médio de pelo menos 40% = 1 ponto, 55% = 2 pontos, 75% = 3 pontos; um ASE acima de 10% precisa ser justificado com uma estratégia contra ofuscamento.

Ambiente	Área m²	sDA300/50%	ASE1000,250	Degrau LEED isolado
Sala de estar (frente)	21,2	2% Sem pontos 2/5	0% Muito baixa 5/5	0 ponto(s)
TV / jantar (fundos)	23,4	100% 3 pontos 5/5	7% Aceitável 4/5	3 ponto(s)
Quarto 1	15,4	100% 3 pontos 5/5	10% Alta 2/5	3 ponto(s)
Quarto 2	14,4	0% Sem pontos 2/5	0% Muito baixa 5/5	0 ponto(s)
Quarto 3	14,1	0% Sem pontos 2/5	0% Muito baixa 5/5	0 ponto(s)
Cozinha	10,8	10% Sem pontos 2/5	0% Muito baixa 5/5	0 ponto(s)
Casa inteira (ponderada pela área)	99,3	41% 1 ponto 3/5	3% Aceitável 4/5	1 ponto(s)

Resultado: sDA300/50% ponderado pela área = 40,6% e ASE1000,250 = 3,2%: **1 de 3 ponto(s) de luz natural**. Ambientes abaixo de 40%: Sala de estar (frente), Quarto 2, Quarto 3, Cozinha.

Isto é uma pré-avaliação indicativa: o LEED exige avaliador certificado, modelagem de mobiliário e persianas, grade de 0,6 m e o procedimento completo da LM-83 (nossa grade é de 0,5 m, com 8h-18h como horas de uso e persianas abertas). O LEED v4,1 cita formalmente a edição de 2012 da LM-83; a edição de 2023 mantém as mesmas duas métricas (não conseguimos verificar as mudanças detalhadas). Residências costumam ser certificadas pelo LEED for Homes, cujas regras de luz natural são diferentes.

Luz natural LEED (sDA300/50%, média ponderada pela área dos ambientes de permanência) Padrão internacional

Autonomia espacial de luz natural média de salas, dormitórios e cozinhas (ponderada pela área do piso): parcela do piso que recebe 300 lux em pelo menos metade das horas de uso. O LEED v4,1 dá 1 ponto a partir de 40%, 2 pontos a partir de 55% e 3 pontos a partir de 75%. Apenas pré-avaliação indicativa: um crédito LEED de verdade exige avaliador certificado e o método completo da LM-83.

Sem pontos 2/5	abaixo de 40 % do piso	Abaixo dos 40% necessários para o primeiro ponto.
1 ponto 3/5	40 a 55 % do piso	Atende ao primeiro degrau de luz natural do LEED.
2 pontos 4/5	55 a 75 % do piso	Atende ao segundo degrau de luz natural do LEED.
3 pontos 5/5	75 ou mais % do piso	Atende ao degrau máximo de luz natural do LEED.

Esta casa: Casa inteira 41% 1 ponto 3/5

Fonte: USGBC LEED v4,1, crédito de Luz natural, Opção 1 (simulação): média de sDA300/50% de 40% / 55% / 75% = 1 / 2 / 3 pontos; ASE1000,250 acima de 10% exige estratégia contra ofuscamento (limites lidos na página do crédito v4,1 no LEEDuser); ANSI/IES LM-83-23 (publicada em fev/2023): autonomia espacial de luz natural (sDA) e exposição solar anual (ASE); o LEED v4,1 ainda cita a edição de 2012, com as mesmas duas métricas. Também é exigido ASE1000,250 de no máximo 10% (senão é preciso explicar a estratégia contra ofuscamento). Banheiros, corredores e áreas externas não são de "permanência".

8,1 Conferência com um motor de referência (Radiance)

Os números acima vêm do nosso motor rápido (sol por traçado de raios + estimativa de fluxo dividido com céu uniforme). Para testá-los, os mesmos ambientes e pontos de medição foram recalculados com o **Radiance** (Lawrence Berkeley National Laboratory), motor de código aberto validado pela CIE 171 e usado pelo ClimateStudio e pelo Honeybee: céu de Perez do mesmo arquivo climático, 4 reflexões de luz, método anual de coeficientes de luz natural e a regra da LM-83 que fecha as persianas quando o sol direto atinge mais de 2% do ambiente (transmitância da persiana 5%). Um sensor acima do telhado reproduz a iluminância do arquivo climático com diferença de 2%, então o céu está calibrado.

Ambiente	Área m²	sDA300/50% rápido	sDA300/50% Radiance	ASE Radiance	Lux médio rápido → Radiance
Sala de estar (frente)	21,2	2%	5% Sem pontos 2/5	0%	150 → 197
TV / jantar (fundos)	23,4	100%	12% Sem pontos 2/5	10%	1.044 → 597
Quarto 1	15,4	100%	12% Sem pontos 2/5	10%	1.009 → 716
Quarto 2	14,4	0%	0% Sem pontos 2/5	0%	164 → 65
Quarto 3	14,1	0%	0% Sem pontos 2/5	0%	174 → 76
Cozinha	10,8	10%	0% Sem pontos 2/5	0%	276 → 136

Resultado com o Radiance: sDA300/50% ponderado pela área = 5,8% (motor rápido: 40,6%), ASE1000,250 = 3,9%: **0 de 3 ponto(s) de luz natural**. O motor rápido é otimista no fundo dos ambientes; prefira os números do Radiance para decisões.

Ainda não modelados na rodada do Radiance: mobiliário, caixilhos e montantes (usa-se transmitância 0,80 para toda a abertura), a treliça da porta de vidro, os prédios vizinhos e a sombra de árvores. As persianas seguem a regra simplificada da LM-83 por ambiente. Janelas e brise como no caso base.

9. Como foi calculado e quanto confiar

Esta seção conta como os números foram produzidos, para você julgar quanto confiar neles. Todos os cálculos são feitos por código Python aberto escrito para este projeto (não é um pacote comercial); os submodelos são padrão em física das edificações, mas simplificados. Nada aqui foi medido no edifício real.

> Situação da validação: o código é verificado por testes de regressão (o caso-base não pode mudar ao acrescentar um recurso) e por conferências da geometria solar e do balanço de energia; NÃO foi validado contra medições nem contra casos de referência do EnergyPlus / ISO 52016. Para licença, certificação ou decisão de investimento, confirme com uma simulação feita por profissional qualificado (por exemplo EnergyPlus, Radiance).

Software utilizado

Python 3,11,9 · NumPy 2,4,6 · pandas 3,0,6 · pvlib 0,16,1 · trimesh 5,1,1 · Embree (embreex) 4,4,0 · IfcOpenShell 0,9,0 · Shapely 2,2,0 · Numba 0,68,0 · Matplotlib 3,11,2 · SciPy 1,17,1

Etapas de cálculo e a confiança em cada uma

Etapa	Como é calculado	Confiabilidade
Modelo 3D e orientação	O edifício é lido de um arquivo IFC (IfcOpenShell). Os ambientes são os volumes IfcSpace; paredes, lajes, telhados, janelas e portas viram malhas de triângulos. O modelo é girado para que o norte verdadeiro venha do Norte Verdadeiro do IFC (mais uma correção opcional). Por quê: Tão exato quanto o modelo: tamanhos, posição das janelas e materiais são estimativas, a menos que o modelo venha de um levantamento.	Alta
Posição do sol e sombras	Posição solar para cada uma das 8,760 horas com o pvlib (algoritmo baseado no NREL SPA). A partir de uma grade de pontos sensores (0,5 m, a 0,76 m de altura) em cada ambiente, traça-se um raio em direção ao sol contra todos os elementos opacos com o Embree (biblioteca de traçado de raios): bloqueado = sombra; um raio que passa por uma janela é atenuado pela transmitância dela. Por quê: A geometria do sol é determinística; o resultado só é tão bom quanto a geometria (vizinhos e árvores só contam se estiverem no modelo).	Alta
Clima	Um ano meteorológico típico com dados horários (.epw do EnergyPlus, como o TMYx do climate.onebuilding.org, ou um ano típico do PVGIS): temperatura, umidade, radiação direta/difusa/global, velocidade e direção do vento. Por quê: Um ano típico não é uma previsão: anos reais são mais quentes ou mais frios. Os dados de vento são de terreno aberto a 10 m.	Média
Luz natural (lux e lumens)	Iluminância no plano de trabalho = sol direto (traçado de raios) + luz do céu (céu isotrópico, fator de visão do céu por traçado de raios) + componente inter-refletida (método do fluxo dividido, refletância média 0,55). A radiação é convertida em lux com eficácias luminosas de 100 lm/W (direta) e 115 lm/W (difusa). Os lumens das lâmpadas usam o método dos lumens: lux x área / (utilização 0,45 x manutenção 0,8). Métricas: lux no centro do ambiente da NBR 15575, sDA300/50% e ASE1000,250 (IES LM-83), horas de sol da EN 17037. Por quê: O céu isotrópico ignora o céu mais claro perto do sol; os resultados podem diferir de ferramentas tipo Radiance em dezenas de porcento. Bom para comparar ambientes e opções.	Média
Temperatura interna (modelo térmico)	Cada ambiente é um modelo de balanço térmico concentrado resolvido hora a hora (Python, compilado com Numba): camadas de parede, forro e piso como nós de armazenamento de calor (resistências e capacidades a partir da condutividade, densidade, calor específico e espessura, no estilo ISO 6946 / NBR 15220-2), temperatura sol-ar nas superfícies externas, sótão ventilado, janelas (U e ganho solar), ventilação (infiltração com tudo fechado, ventilação cruzada pelo vento com janelas abertas, ambientes ligados por portas) e massa térmica. Temperatura operativa = média da temperatura do ar e das superfícies. O conforto usa o modelo adaptativo da ASHRAE 55 (aceitabilidade de 80% e 90%) e as verificações de dia mais quente/frio da NBR 15575. Por quê: Um modelo simplificado de uma zona por ambiente, não calibrado com medições e não validado contra o EnergyPlus (ISO 52016) neste projeto: use-o para comparar ambientes e melhorias, não como previsão exata.	Média
Energia e custo de ar-condicionado / aquecimento	Quando o ambiente fica acima da temperatura de refrigeração (ou abaixo da de aquecimento) no seu horário de uso, o modelo soma o fluxo de calor necessário para manter a temperatura; eletricidade = calor / COP (refrigeração) ou combustível = calor / eficiência (aquecimento), custo = energia x tarifa. As janelas ficam fechadas com o equipamento ligado. Só calor sensível; sem calor de pessoas, aparelhos ou iluminação. Por quê: As contas reais diferem: carga latente, hábitos dos moradores, eficiência do equipamento e a tarifa (uma suposição) importam. Trate o custo como ordem de grandeza e como forma de comparar opções.	Baixa
Vento e ventilação cruzada	Rosas dos ventos do arquivo climático; cada janela é classificada como a barlavento / sotavento / lateral a cada hora; ambientes cujas janelas conectadas ficam de frente para o vento e para o lado oposto recebem mais trocas de ar. Sem CFD. Por quê: Uma estimativa por regras: o vento na casa é menor e mais turbulento que na estação; não há cálculo de escoamento por pressão.	Baixa
Cenários de melhoria	Cada melhoria altera o modelo-base e o ano inteiro é simulado de novo: o isolamento do telhado soma uma camada de condução (espessura / condutividade) no lado do sótão do forro; a vedação reduz a taxa de trocas de ar com a casa fechada; o vidro altera o U da janela, o fator de ganho solar e a transmitância visível; o brise fixo corta o sol direto pela profundidade da sombra = beiral x tan(ângulo de perfil); persianas móveis multiplicam o ganho solar por 0,3 sempre que o sol na janela passa de 250 W/m2 durante o dia. Por quê: Bom para ordenar opções (as diferenças entre cenários são mais confiáveis que os valores absolutos). As propriedades dos materiais são valores de catálogo; a confiança de cada valor aparece ao lado dele. O sombreamento é analítico, não por traçado de raios.	Média
Avaliações e pré-avaliação LEED	Os números são comparados com normas da ABNT quando existem (NBR 15575, NBR 15220, NBR 5413, NBR 16401), com padrões internacionais nos demais casos (EN 17037, IES LM-83, ASHRAE 55, OMS) e com algumas regras práticas identificadas como tal. Os pontos de luz natural do LEED v4,1 seguem a Opção 1 (sDA300/50% e ASE1000,250). Por quê: Vários valores de norma foram lidos de resumos públicos ou projetos de emenda, não dos textos completos da ABNT; o resultado LEED é uma pré-avaliação indicativa, não uma certificação.	Média

Referências

- pvlib python: a Python package for modeling solar energy systems (Holmgren, Hansen, Mikofski, JOSS 2018) - https://joss.theoj.org/papers/10.21105/joss.00884
- PVGIS typical meteorological year (European Commission JRC) - https://re.jrc.ec.europa.eu/pvg_tools/en/
- Climate.OneBuilding.Org: TMYx weather files - https://climate.onebuilding.org
- Embree ray-tracing kernels (Intel) - https://github.com/embree/embree
- IfcOpenShell: open-source IFC toolkit - https://ifcopenshell.org
- Numba: JIT compiler for Python - https://numba.pydata.org
- ASHRAE Standard 55: thermal environmental conditions for human occupancy (adaptive comfort model) - https://www.ashrae.org/technical-resources/standards-and-guidelines
- ABNT NBR 15575 (Residential buildings - performance) and NBR 15220 (Thermal performance of buildings) - https://www.abntcatalogo.com.br
- EN 17037: Daylight in buildings - https://standards.cencenelec.eu
- ANSI/IES LM-83-23: sDA and ASE - https://webstore.ansi.org/standards/iesna/ansiieslm8323
- USGBC LEED v4,1 Daylight credit (Option 1: simulation) - https://leeduser.buildinggreen.com/credit/CI-v4,1/EQc7
- AIVC: air infiltration reduction by weatherstripping retrofits - https://www.aivc.org/resource/reduction-air-infiltration-due-window-and-door-retrofits-older-home
- WHO Housing and Health Guidelines (2018) - https://www.who.int/publications/i/item/9789241550376

10. Premissas, limites e fontes

- As **dimensões** vêm do modelo 3D fornecido: uma varredura em vídeo mais o anúncio; isto não é um levantamento topográfico.
- Os **materiais**: o bloco cerâmico padrão brasileiro de 8 furos com reboco e uma cobertura de telha cerâmica com forro de laje de concreto, não confirmados para esta casa. Prédios vizinhos, árvores da rua e cortinas não são modelados, a menos que estejam no modelo.
- As **portas** são supostas abertas para luz e ar. Móveis, pessoas, eletrodomésticos e calor da iluminação não estão incluídos (casa vazia).
- O modelo de conforto é um balanço térmico horário simplificado, não calibrado com medições: use-o para comparar ambientes e opções. O EnergyPlus seria o próximo nível de rigor.
- Os dados de **vento** são de terreno aberto a 10 m; dentro de um lote com muros e vizinhos as velocidades são menores. Não foi feita CFD.
- A **luz natural** usa um céu isotrópico; céus reais parcialmente nublados são mais claros perto do sol.
- As escalas marcadas *Regra prática* são nossas; as marcadas como norma vêm dos documentos listados abaixo. Vários valores de norma foram lidos de resumos públicos e projetos de emenda: confirme-os nos textos completos da ABNT antes de usá-los em decisão legal, contratual ou de financiamento.

Fontes

- ABNT NBR 15575-1:2013 (Edificações habitacionais — Desempenho), requisitos de iluminação natural e desempenho térmico
- ABNT NBR 15575-1:2021 + emenda (desempenho térmico por simulação, comparado a uma casa de referência)
- Projeto de emenda da ABNT NBR 15575-4:2021 (mar/2021): método simplificado para paredes, ventilação e áreas transparentes
- Projeto de emenda da ABNT NBR 15575-5:2021: método simplificado para coberturas
- ABNT NBR 15220-3: zoneamento bioclimático brasileiro e diretrizes construtivas (Maringá costuma ser listada na zona 3)
- ABNT NBR 5413:1992 (cancelada em 2013, mas ainda a referência brasileira mais usada para iluminação de RESIDÊNCIAS)
- ABNT NBR ISO/CIE 8995-1:2013 (iluminação de ambientes de trabalho; leitura e escrita 300–500 lx)
- EN 17037:2018 Iluminação natural em edifícios (Anexo Nacional do Reino Unido para moradias: 100/150/200 lx; insolação 1,5/3/4 h)
- IES LM-83-12 (sDA e ASE), como usado no LEED v4,1
- ASHRAE 55, modelo de conforto adaptativo (aceitabilidade de 80% / 90%)
- ABNT NBR 16401-2 (ar-condicionado, conforto interno): verão cerca de 22,5–25,5 °C com 65% de UR e 23–26 °C com 35% de UR
- Passive House Institute, critério: demanda de aquecimento de no máximo 15 kWh por m² por ano
- USGBC LEED v4,1, crédito de Luz natural, Opção 1 (simulação): média de sDA300/50% de 40% / 55% / 75% = 1 / 2 / 3 pontos; ASE1000,250 acima de 10% exige estratégia contra ofuscamento (limites lidos na página do crédito v4,1 no LEEDuser)
- ANSI/IES LM-83-23 (publicada em fev/2023): autonomia espacial de luz natural (sDA) e exposição solar anual (ASE); o LEED v4,1 ainda cita a edição de 2012, com as mesmas duas métricas
- OMS, Diretrizes de Habitação e Saúde 2018 (temperatura interna de pelo menos 18 °C)
- Escala de vento Beaufort (OMM)
- Regra prática deste estudo (nenhuma norma dá um número)

Rode de novo depois de mudar o modelo

Edite o modelo 3D (house.ifc) e dê dois cliques em **run_all.bat** na pasta House3D. Ele refaz a simulação, este PDF e os dados do visualizador 3D (viewer / open_viewer.bat).