Sua casa: luz, sol, calor e vento

Casa Maringá · relatório de simulação · Maringá, PR (lat -23,41, lon -51,93) · 19 de outubro de 2026
Clima: ano típico de BRA_PR_Maringa.868990_TMYx.2011-2025.epw · sol anual 1.882 kWh/m² · temperatura média 23,0 °C · vento médio 2,3 m/s

Como ler este relatório. Cada número vem com uma etiqueta colorida que diz se ele é bom ou ruim, em um **nível de 1 (péssimo) a 5 (excelente)**:

Excelente 5/5 Bom 4/5 Aceitável 3/5 Ruim 2/5 Péssimo 1/5

Cada etiqueta se baseia em uma **norma brasileira (ABNT)** quando existe, em um **padrão internacional** quando o Brasil não dá um número, ou em uma **regra prática** claramente identificada. Os quadros *O que conta como bom?* no fim de cada seção mostram a escala completa e a fonte. As paredes do modelo foram supostas como: *Bloco cerâmico furado de 8 furos 9x19x19 cm + 2 cm de reboco nos dois lados = parede de 13 cm (bloco padrão brasileiro)*; cobertura: *Telha cerâmica + sótão + laje de concreto de 12 cm*. Ventilação do sótão (desvão do telhado) adotada: **5,0 trocas de ar por hora** (comum). Não foi encontrada medição para telhado cerâmico sobre laje no Brasil, então este valor é uma premissa; a tabela mostra o quanto ela pesa.

Trocas de ar do sótão/h	Horas quentes demais (cômodo médio)	Ar-condicionado kWh/ano
1	1.354	1.782
5	1.210	1.657
10	1.089	1.546

Esses materiais e os tamanhos de janela (medidas comuns de catálogo por volta de 2012) são estimativas, não medições: use os resultados para comparar ambientes e opções, não como garantia.

1. Resumo

Cada ambiente é avaliado em até nove verificações, cada uma em um **nível de 1 (péssimo) a 5 (excelente)**; a coluna GERAL é o nível médio. As próximas páginas explicam cada verificação; a coluna de climatização mostra quanto um ar-condicionado custaria por ano:

Ambiente	Luz natural (NBR 15575)	Lâmpadas apagadas de dia	Sol na janela	Horas de conforto	Dia quente	Dia frio	Janela abrível	Custo de climatização	GERAL
Quarto 1	Superior 5/5	Quase sempre 5/5	Alto 5/5	Aceitável 3/5	Intermediário 4/5	Superior 5/5	Atende ao mínimo 3/5	R$ 219/ano Baixa 4/5	Bom 4,3/5
Banheiro 1	Superior 5/5	Quase sempre 5/5	-	Aceitável 3/5	-	-	-	-	Bom 4,3/5
Sala de estar	Superior 5/5	Quase sempre 5/5	Abaixo do mínimo 2/5	Bom 4/5	Intermediário 4/5	Superior 5/5	Atende ao mínimo 3/5	R$ 325/ano Baixa 4/5	Bom 4,1/5
Sala de TV	Superior 5/5	Quase sempre 5/5	Abaixo do mínimo 2/5	Bom 4/5	Intermediário 4/5	Superior 5/5	Atende ao mínimo 3/5	R$ 375/ano Baixa 4/5	Bom 4,1/5
Corredor	Sem exigência 3/5	Quase nunca 1/5	-	Excelente 5/5	-	-	-	-	Aceitável 3,0/5
Quarto 2	Superior 5/5	Quase sempre 5/5	Mínimo 3/5	Bom 4/5	Intermediário 4/5	Superior 5/5	Boa margem 5/5	R$ 146/ano Baixa 4/5	Bom 4,3/5
Banheiro 2	Superior 5/5	Frequentemente 4/5	-	Bom 4/5	-	-	-	-	Bom 4,3/5
Quarto 3	Superior 5/5	Quase sempre 5/5	Mínimo 3/5	Bom 4/5	Intermediário 4/5	Superior 5/5	Boa margem 5/5	R$ 142/ano Baixa 4/5	Bom 4,3/5
Cozinha	Superior 5/5	Quase sempre 5/5	Abaixo do mínimo 2/5	Aceitável 3/5	-	-	Atende ao mínimo 3/5	R$ 450/ano Moderada 3/5	Bom 3,7/5
Banheiro externo	-	Quase sempre 5/5	-	Aceitável 3/5	-	-	-	-	Bom 4,0/5
Depósito externo	-	Quase sempre 5/5	-	Aceitável 3/5	-	-	-	-	Bom 4,0/5
Casa inteira								**R$ 1.657/ano**	Bom 4,1/5

O que funciona bem


- Quarto 1: 907 lux de luz natural no centro (nível superior da NBR 15575)
- Sala de estar: 236 lux de luz natural no centro (nível superior da NBR 15575)
- Sala de TV: 549 lux de luz natural no centro (nível superior da NBR 15575)
- Quarto 2: 486 lux de luz natural no centro (nível superior da NBR 15575)
- Quarto 3: 352 lux de luz natural no centro (nível superior da NBR 15575)
- Cozinha: 208 lux de luz natural no centro (nível superior da NBR 15575)
- Ambiente mais confortável: Corredor (93% do ano na faixa de conforto; ao ar livre só 48%)
- Transmitância térmica U da parede externa: 2,52 W/m²K atende ao limite <= 3,7
- Capacidade térmica da parede externa: 134,0 kJ/m²K atende ao limite >= 130

O que merece atenção

- Ambiente menos confortável: Banheiro externo (68%; 1968 h quente demais, 808 h frio demais)
- Transmitância térmica U da cobertura (indicativa): 1,78 W/m²K contra o limite <= 1,5

PLANTA BAIXA - térreo

A casa é voltada para o NORTE (rua embaixo) - ambientes com nome, medidas e área; cor

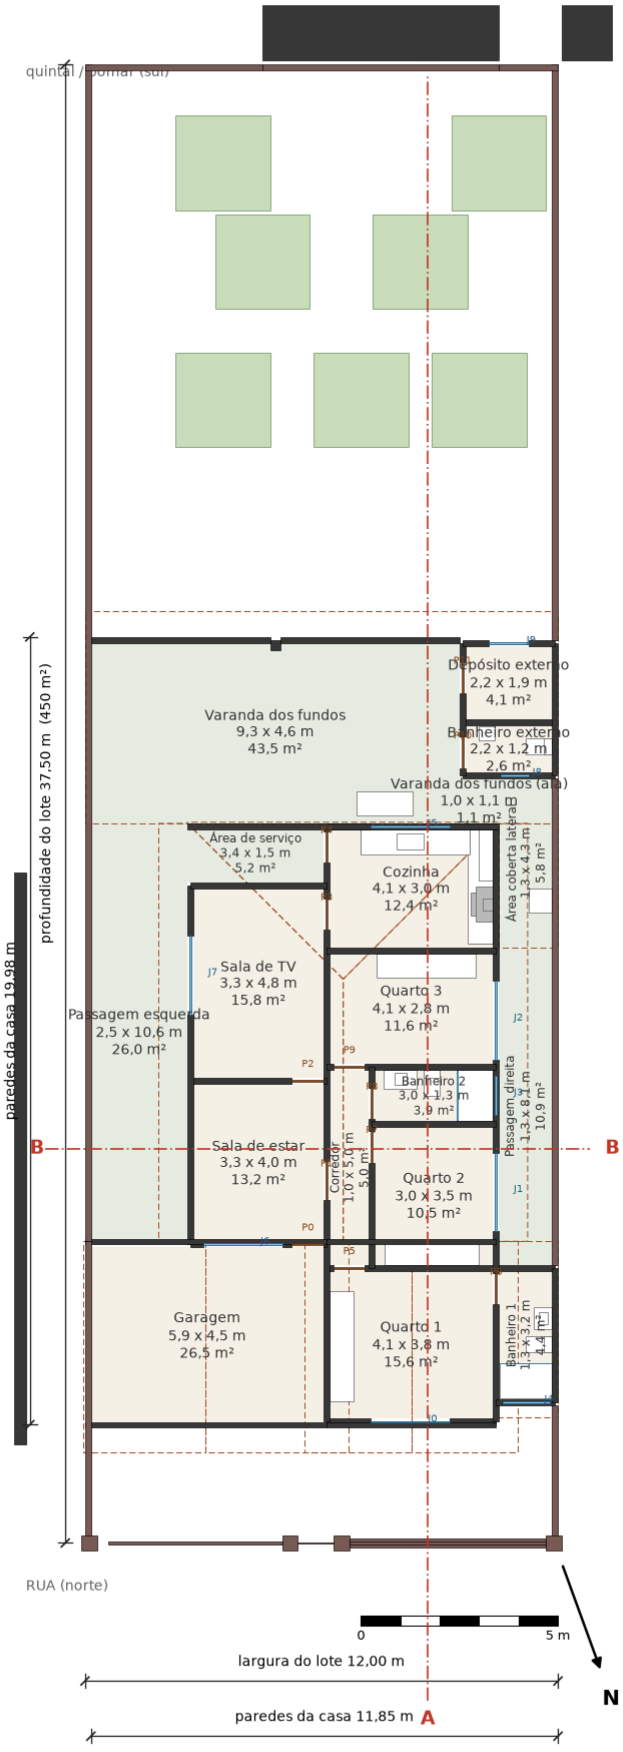

s plantas aprovadas na prefeitura (casa 2008, ampliação 2012), não um levantamento da casa como construída

Planta do modelo (norte embaixo).

2. Luz natural

A luz natural economiza energia e deixa os ambientes agradáveis. A norma brasileira NBR 15575 pede pelo menos **60 lux** no centro de salas, dormitórios e cozinhas (lux = quanta luz chega a uma mesa). Para comparar: um dia claro e nublado ao ar livre tem milhares de lux.

2,1 Ensaio brasileiro: luz no centro do ambiente, lâmpadas apagadas

Ambiente	Lux no centro	Veredito
Quarto 1	907	Superior 5/5
Banheiro 1	271	Superior 5/5
Sala de estar	236	Superior 5/5
Sala de TV	549	Superior 5/5
Corredor	0	Sem exigência 3/5
Quarto 2	486	Superior 5/5
Banheiro 2	126	Superior 5/5
Quarto 3	352	Superior 5/5
Cozinha	208	Superior 5/5
Banheiro externo	351	Superior 5/5
Depósito externo	511	Superior 5/5


Calculado com: **Motor rápido (Python, deste projeto)** · detalhes e confiabilidade na seção 10

2,2 Quanto do ambiente é claro, e quando preciso de lâmpada?

Ambiente	Meta (lux)	Piso que atinge a meta	Dia com lâmpadas apagadas	Sol forte (ASE)
Quarto 1	100	100% Ambiente inteiro 5/5	98% Quase sempre 5/5	33% Muito alta 1/5
Banheiro 1	-	-	88% Quase sempre 5/5	0% Muito baixa 5/5
Sala de estar	150	100% Ambiente inteiro 5/5	87% Quase sempre 5/5	0% Muito baixa 5/5
Sala de TV	150	100% Ambiente inteiro 5/5	97% Quase sempre 5/5	7% Aceitável 4/5
Corredor	-	-	1% Quase nunca 1/5	0% Muito baixa 5/5
Quarto 2	100	100% Ambiente inteiro 5/5	97% Quase sempre 5/5	21% Muito alta 1/5
Banheiro 2	-	-	71% Frequentemente 4/5	0% Muito baixa 5/5
Quarto 3	100	100% Ambiente inteiro 5/5	96% Quase sempre 5/5	19% Alta 2/5
Cozinha	200	100% Ambiente inteiro 5/5	88% Quase sempre 5/5	0% Muito baixa 5/5
Banheiro externo	-	-	94% Quase sempre 5/5	0% Muito baixa 5/5
Depósito externo	-	-	98% Quase sempre 5/5	0% Muito baixa 5/5

Calculado com: **Motor rápido (Python, deste projeto)** · detalhes e confiabilidade na seção 10

Meta = o nível de luz natural que a EN 17037 (Anexo Nacional do Reino Unido para moradias) recomenda: 100 lux dormitório, 150 lux sala, 200 lux cozinha. “Lâmpadas apagadas” = parcela das horas entre 8h e 18h em que a média de luz natural já atinge o nível de luz geral da seção 3.

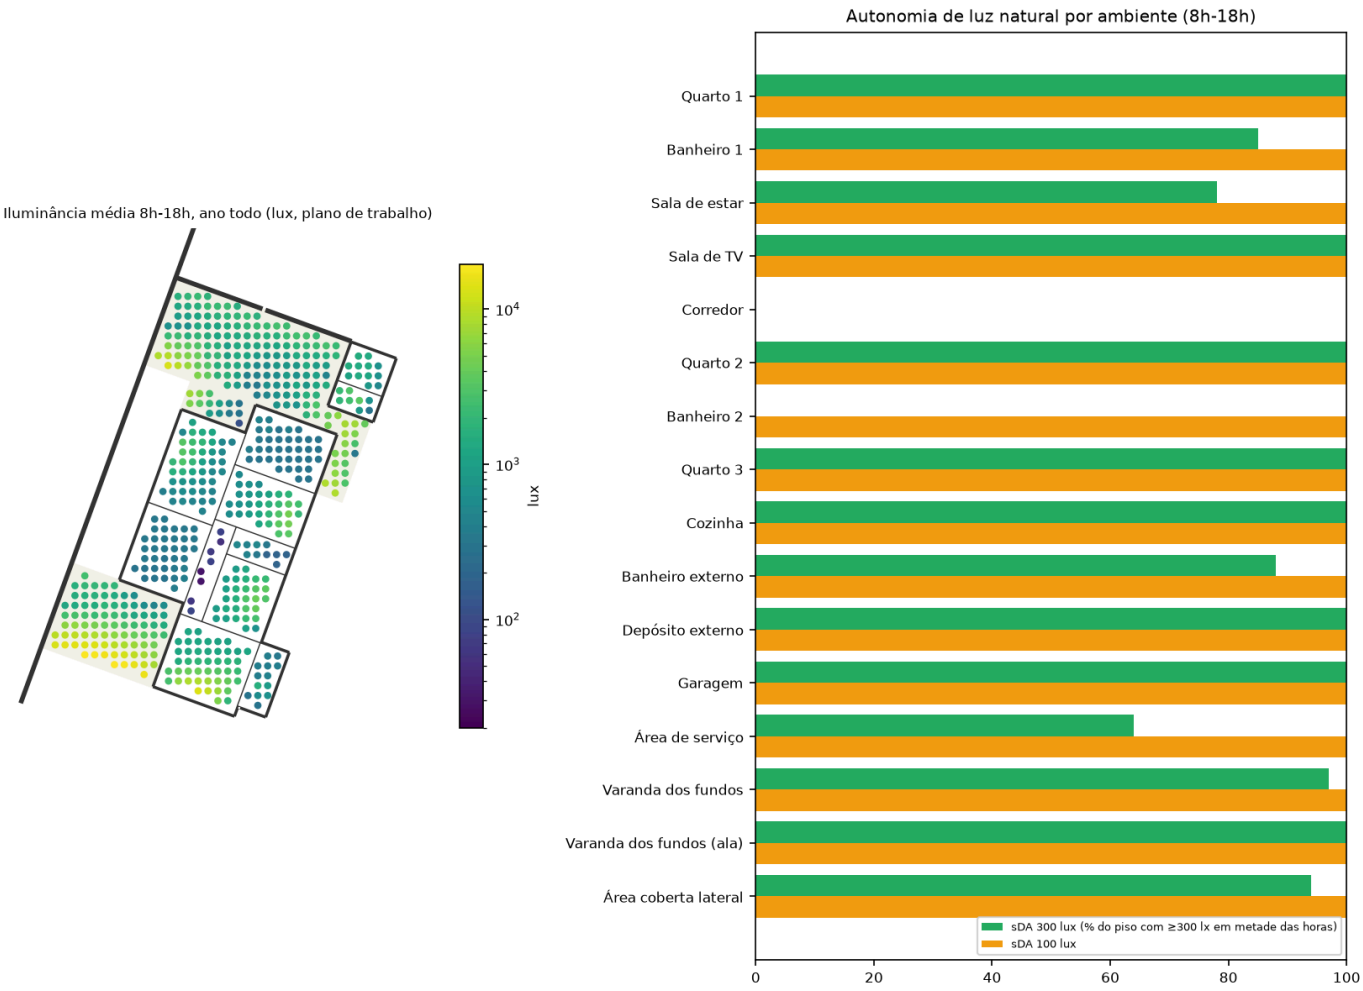


Esquerda: luz média no piso ao longo do ano. Direita: parcela de cada ambiente que atinge 100 e 300 lux.


2,3 Sol que chega às janelas

Ambiente	Sol na janela, horas/dia (início da primavera)	Veredito
Quarto 1	7,0	Alto 5/5
Sala de estar	0,0	Abaixo do mínimo 2/5
Sala de TV	1,0	Abaixo do mínimo 2/5
Quarto 2	1,7	Mínimo 3/5
Quarto 3	1,7	Mínimo 3/5
Cozinha	0,5	Abaixo do mínimo 2/5

Calculado com: **Motor rápido (Python, deste projeto)** · detalhes e confiabilidade na seção 10

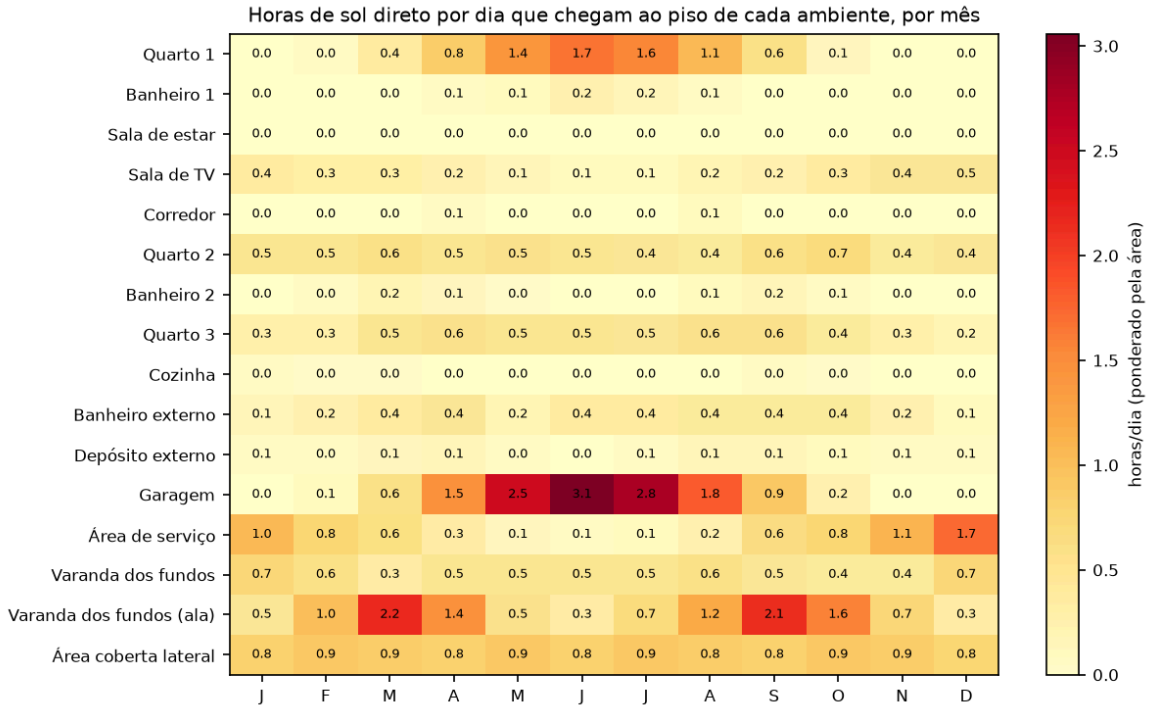

Horas por dia de sol direto que chegam ao piso de cada ambiente, por mês (J = janeiro).

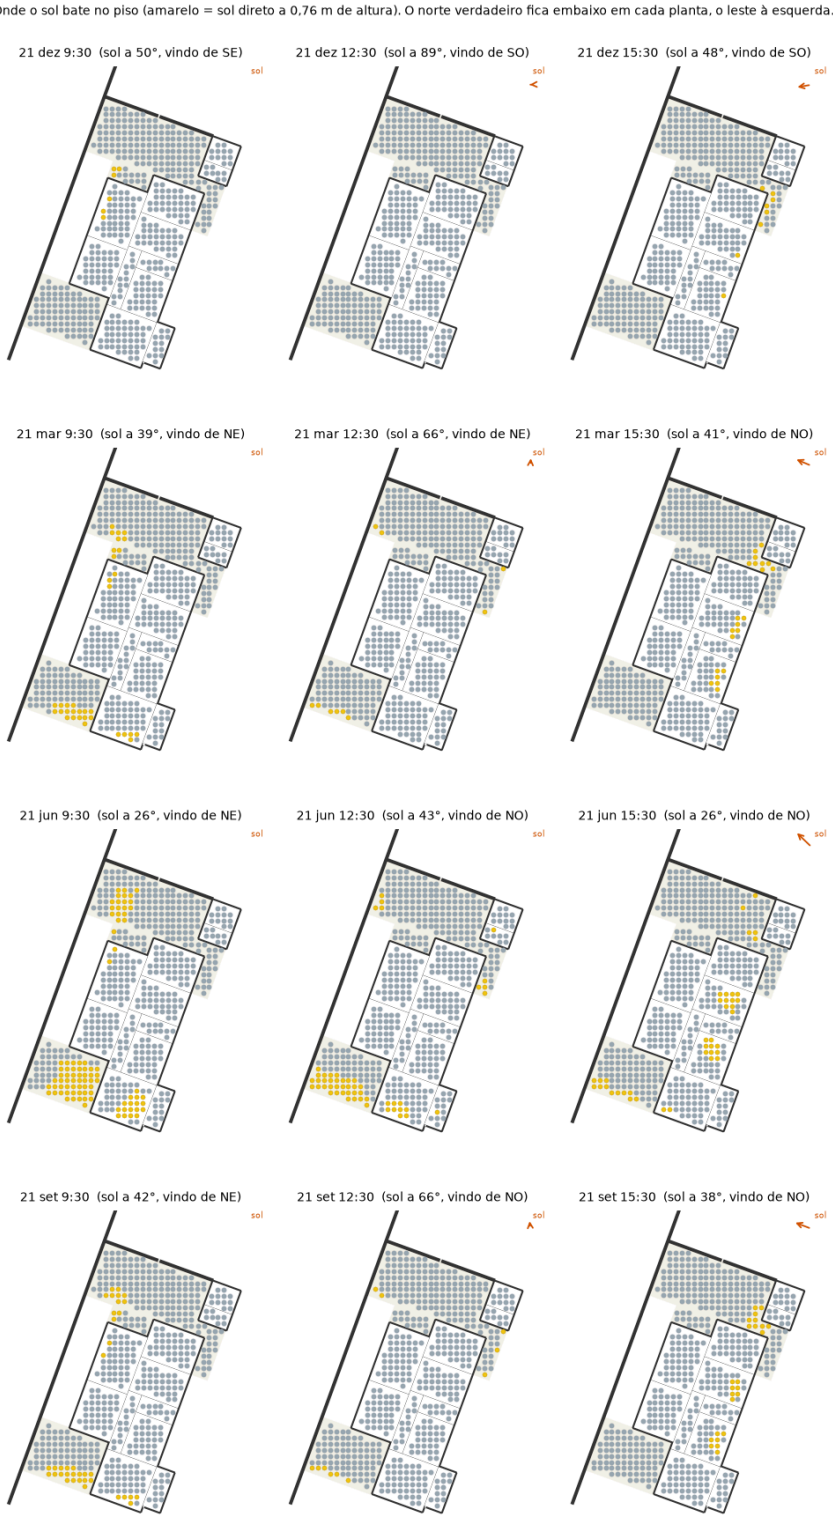


Onde o sol bate no piso em quatro datas-chave.

2,4 O sol e suas sombras ao longo do dia no modelo 3D

Calculado com: **Motor rápido (Python, deste projeto)** · detalhes e confiabilidade na seção 10

Estas imagens vêm do mesmo modelo 3D e do mesmo cálculo do sol do visualizador interativo: três datas-chave, cinco horários. São desenhadas as sombras da casa, da cobertura, dos muros e das árvores; os pisos que recebem sol direto ficam amarelos/laranja. no inverno o sol baixo entra fundo nos ambientes voltados para ele, enquanto no verão o sol fica alto ao meio-dia e a cobertura sombreia a casa.

O sol e suas sombras ao longo do dia no modelo 3D (vista do noroeste: o lado norte está mais perto de você)

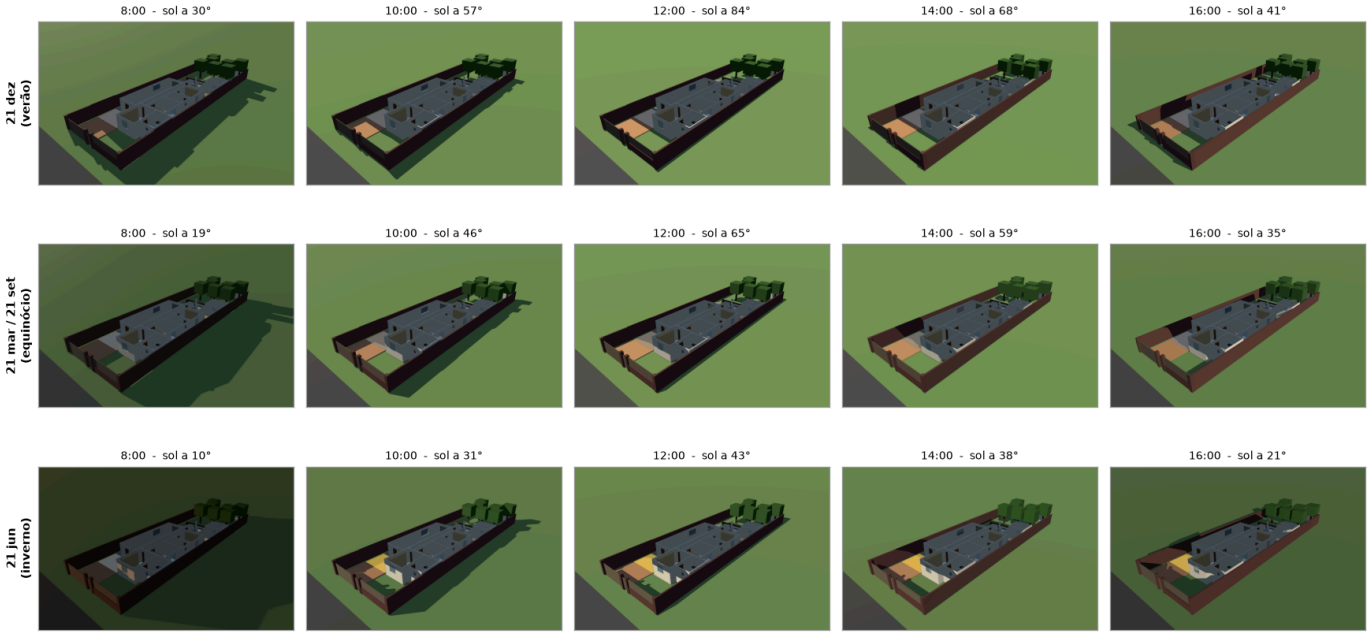

Bússola: o leste fica à esquerda de cada imagem e o oeste à direita, então o sol nasce à esquerda e se põe à direita. Piso amarelo = sol direto.

Sol e sombras ao longo do dia: vista 3D do noroeste (frente / rua mais perto).

O sol e suas sombras ao longo do dia, vistos de cima (norte verdadeiro embaixo)



Bússola: o leste fica à esquerda de cada imagem e o oeste à direita, então o sol nasce à esquerda e se põe à direita. Piso amarelo = sol direto.

Os mesmos momentos vistos de cima (rua / frente embaixo).

O que conta como bom? (luz)

Luz natural no centro do ambiente (ensaio da NBR 15575) Norma brasileira

Luz natural em um plano na altura de uma mesa (0,75 m), no meio do ambiente, em 23 de abril e 23 de outubro às 9h30 e às 15h30, com céu parcialmente nublado e lâmpadas apagadas. Vale a menor das quatro leituras. Aplica-se a salas, dormitórios, cozinhas e áreas de serviço.

Não atende 1/5	abaixo de 60 lux	Abaixo do mínimo de 60 lux: é preciso acender a luz até ao meio-dia.
Mínimo 3/5	60 a 90 lux	Atende ao mínimo exigido pela norma.
Intermediário 4/5	90 a 120 lux	Melhor que o mínimo.
Superior 5/5	120 ou mais lux	Nível máximo da norma.

Esta casa: Quarto 1 907 lux Superior 5/5 | Sala de estar 236 lux Superior 5/5 | Sala de TV 549 lux Superior 5/5 | Quarto 2 486 lux Superior 5/5 | Quarto 3 352 lux Superior 5/5 | Cozinha 208 lux Superior 5/5

Fonte: ABNT NBR 15575-1:2013 (Edificações habitacionais — Desempenho), requisitos de iluminação natural e desempenho térmico. Nosso cálculo usa o clima típico da semana em torno dessas datas e só a luz do céu (sem sol direto), portanto fica a favor da segurança.

Luz natural no centro do ambiente (ensaio da NBR 15575): banheiros, corredores, escadas, garagens Norma brasileira

O mesmo ensaio, para ambientes onde as pessoas não ficam muito tempo.

Sem exigência 3/5	abaixo de 30 lux	A norma não exige luz natural aqui (nível mínimo: "não requerido").
Intermediário 4/5	30 a 45 lux	Atende ao nível intermediário.
Superior 5/5	45 ou mais lux	Atende ao nível superior.

Esta casa: Banheiro 1 271 lux Superior 5/5 | Corredor 0 lux Sem exigência 3/5 | Banheiro 2 126 lux Superior 5/5

Fonte: ABNT NBR 15575-1:2013 (Edificações habitacionais — Desempenho), requisitos de iluminação natural e desempenho térmico.

Parcela do piso que atinge a luz recomendada para moradias Padrão internacional

Porcentagem do piso do ambiente que recebe, só de luz natural, pelo menos a luz-meta (100 lux no dormitório, 150 lux na sala, 200 lux na cozinha) durante pelo menos metade das horas do dia (8h às 18h).

Abaixo da meta 2/5	abaixo de 50 % do piso	Menos da metade do ambiente atinge a meta: será preciso acender lâmpadas de dia.
Atende à meta 4/5	50 a 95 % do piso	Pelo menos metade do piso atinge a meta durante metade do dia.
Ambiente inteiro 5/5	95 ou mais % do piso	Praticamente todo o ambiente atinge a meta.

Esta casa: Quarto 1 100% Ambiente inteiro 5/5 | Sala de estar 100% Ambiente inteiro 5/5 | Sala de TV 100% Ambiente inteiro 5/5 | Quarto 2 100% Ambiente inteiro 5/5 | Quarto 3 100% Ambiente inteiro 5/5 | Cozinha 100% Ambiente inteiro 5/5

Fonte: EN 17037:2018 Iluminação natural em edifícios (Anexo Nacional do Reino Unido para moradias: 100/150/200 lx; insolação 1,5/3/4 h). A EN 17037 pede a luz-meta em pelo menos 50% da área durante metade das horas de luz do dia (mais um nível menor em 95% da área).

Autonomia espacial de luz natural sDA 300/50% (padrão para ambientes de trabalho) Padrão internacional

Porcentagem do piso com pelo menos 300 lux de luz natural durante pelo menos metade das horas de uso. 300 lux é um nível de luz de TRABALHO; portanto este é um teste rigoroso, útil para escritório em casa, cozinha ou estudo. Dormitórios e corredores não precisam chegar lá.

Abaixo do recomendado 2/5	abaixo de 55 % do piso	Menos de 55% do piso atinge 300 lux durante metade do dia.
Nominalmente aceitável 3/5	55 a 75 % do piso	Aceito pela IES / LEED (55% ou mais).
Preferível 5/5	75 ou mais % do piso	Nível preferível (75% ou mais).

Esta casa: Quarto 1 100% Preferível 5/5 | Banheiro 1 85% Preferível 5/5 | Sala de estar 78% Preferível 5/5 | Sala de TV 100% Preferível 5/5 | Corredor 0% Abaixo do recomendado 2/5 | Quarto 2 100% Preferível 5/5 | Banheiro 2 0% Abaixo do recomendado 2/5 | Quarto 3 100% Preferível 5/5 | Cozinha 100% Preferível 5/5 | Banheiro externo 88% Preferível 5/5 | Depósito externo 100% Preferível 5/5

Fonte: IES LM-83-12 (sDA e ASE), como usado no LEED v4,1.

Exposição solar anual ASE (risco de ofuscamento e superaquecimento) Padrão internacional

Porcentagem do piso que recebe sol direto forte (acima de 1000 lux) por mais de 250 horas por ano. Valores altos significam ofuscamento, móveis desbotados e calor.

Muito baixa 5/5	abaixo de 3 % do piso	Quase nenhum sol direto forte.
Aceitável 4/5	3 a 10 % do piso	Dentro do limite de 10% usado pela IES / LEED.
Alta 2/5	10 a 20 % do piso	Acima do limite de 10%: considere cortinas, persianas ou um beiral.
Muito alta 1/5	20 ou mais % do piso	Grande área com sol forte por muito tempo: ofuscamento e calor prováveis.

Esta casa: Quarto 1 33% Muito alta 1/5 | Banheiro 1 0% Muito baixa 5/5 | Sala de estar 0% Muito baixa 5/5 | Sala de TV 7% Aceitável 4/5 | Corredor 0% Muito baixa 5/5 | Quarto 2 21% Muito alta 1/5 | Banheiro 2 0% Muito baixa 5/5 | Quarto 3 19% Alta 2/5 | Cozinha 0% Muito baixa 5/5 | Banheiro externo 0% Muito baixa 5/5 | Depósito externo 0% Muito baixa 5/5

Fonte: IES LM-83-12 (sDA e ASE), como usado no LEED v4,1.

Horas do dia sem precisar de lâmpadas Regra prática

Parcela das horas do dia em que a luz natural média do ambiente já atinge o nível geral recomendado (veja a tabela de lâmpadas), e as luzes podem ficar apagadas.

Quase nunca 1/5	abaixo de 10 % das horas entre 8h e 18h	Você vai acender as luzes o dia todo.
Raramente 2/5	10 a 25 % das horas entre 8h e 18h	Lâmpadas necessárias na maior parte do dia.
Às vezes 3/5	25 a 50 % das horas entre 8h e 18h	Lâmpadas necessárias em dias nublados e de manhã / à tarde.
Frequentemente 4/5	50 a 75 % das horas entre 8h e 18h	Lâmpadas quase sempre apagadas de dia.
Quase sempre 5/5	75 ou mais % das horas entre 8h e 18h	Lâmpadas apagadas quase o dia inteiro.

Esta casa: Quarto 1 98% Quase sempre 5/5 | Banheiro 1 88% Quase sempre 5/5 | Sala de estar 87% Quase sempre 5/5 | Sala de TV 97% Quase sempre 5/5 | Corredor 1% Quase nunca 1/5 | Quarto 2 97% Quase sempre 5/5 | Banheiro 2 71% Frequentemente 4/5 | Quarto 3 96% Quase sempre 5/5 | Cozinha 88% Quase sempre 5/5 | Banheiro externo 94% Quase sempre 5/5 | Depósito externo 98% Quase sempre 5/5

Fonte: Regra prática deste estudo (nenhuma norma dá um número); ABNT NBR 5413:1992 (cancelada em 2013, mas ainda a referência brasileira mais usada para iluminação de RESIDÊNCIAS).

Sol direto na janela no início da primavera Padrão internacional

Horas de sol direto que chegam às janelas do ambiente em um dia típico do início da primavera: 1º de agosto a 21 de setembro no hemisfério sul, 1º de fevereiro a 21 de março no norte (as datas da EN 17037). Sol no inverno e no início da primavera faz bem à saúde e aquece.

Abaixo do mínimo 2/5	abaixo de 1,5 horas/dia	Menos de 1,5 h de sol: o ambiente parece sem sol.
Mínimo 3/5	1,5 a 3 horas/dia	Atende ao mínimo da EN 17037 (1,5 h).
Médio 4/5	3 a 4 horas/dia	Atende ao nível médio da EN 17037 (3 h).
Alto 5/5	4 ou mais horas/dia	Atende ao nível alto da EN 17037 (4 h).

Esta casa: Quarto 1 7,0 h Alto 5/5 | Sala de estar 0,0 h Abaixo do mínimo 2/5 | Sala de TV 1,0 h Abaixo do mínimo 2/5 | Quarto 2 1,7 h Mínimo 3/5 | Quarto 3 1,7 h Mínimo 3/5 | Cozinha 0,5 h Abaixo do mínimo 2/5

Fonte: EN 17037:2018 Iluminação natural em edifícios (Anexo Nacional do Reino Unido para moradias: 100/150/200 lx; insolação 1,5/3/4 h). A EN 17037 pede isso para pelo menos um cômodo principal (de preferência a sala); banheiros e corredores são isentos.

3. Lâmpadas: quanta luz instalar (lumens)

Lux é a luz que chega a uma superfície; **lumens** é a luz que uma lâmpada emite. Para ter uma média de X lux em um piso de A m² você precisa de X × A ÷ (utilização × manutenção = 0,45 × 0,8 = 0,36) lumens. A coluna "mínimo" é só lux × m².

3,1 Níveis de luz recomendados em casa

Tipo de ambiente	Luz geral (lux): mín / recomendado / máx	Luz de tarefa (lux)	Fonte
Sala de estar / jantar	100 / 150 / 200	300 / 500 / 750 - leitura, escrita, costura	NBR 5413 (residências); EN 12464-1 / NBR 8995-1 para tarefas de leitura
Dormitório	100 / 150 / 200	200 / 300 / 500 - leitura na cama, penteadeira	NBR 5413 (residências)
Cozinha	100 / 150 / 200	200 / 300 / 500 - fogão, pia e bancada (a EN 12464-1 pede 500)	NBR 5413 (residências); EN 12464-1
Banheiro	100 / 150 / 200	200 / 300 / 500 - espelho (barba, maquiagem)	NBR 5413 (residências)
Corredor / circulação	75 / 100 / 150	-	NBR 5413 (residências)
Lavanderia / depósito / banheiro externo	100 / 150 / 200	200 / 300 / 500 - lavanderia e ferramentas	NBR 5413 (residências)
Varanda / garagem (área externa coberta)	50 / 75 / 100	-	NBR 5413 (garagens 50-75-100)

Calculado com: **Modelo 3D (IFC) e tabelas** · tabelas de norma, sem cálculo · detalhes e confiabilidade na seção 10


Leitura: ilumine o ambiente no nível geral (100-200 lux) e acrescente uma **luminária de leitura direcional de cerca de 450-800 lumens** (cerca de 4-8 W de LED) perto da página para chegar a **300-500 lux** nela (NBR ISO/CIE 8995-1 e EN 12464-1 para leitura e escrita; NBR 5413 para residências). Ler só com os 100-150 lux da luz geral cansa a vista. Para ter noção: 100 lm = luz noturna / lâmpada vela pequena; 450 lm = equivalente a uma lâmpada incandescente de 40 W; 800 lm = equivalente a uma lâmpada incandescente de 60 W; 1600 lm = equivalente a uma lâmpada incandescente de 100 W.

3,2 Lumens de lâmpada para cada ambiente desta casa

Ambiente	m²	Meta de luz geral	Luz de tarefa (leitura etc.)	Lumens das lâmpadas: mínimo - projeto	Watts de LED (projeto)
Quarto 1	15,6	150 lux	300 lux (leitura na cama, penteadeira)	2.334 - 6.484	65
Banheiro 1	4,4	150 lux	300 lux (espelho (barba, maquiagem))	658 - 1.828	18
Sala de estar	13,2	150 lux	500 lux (leitura, escrita, costura)	1.980 - 5.500	55
Sala de TV	15,8	150 lux	500 lux (leitura, escrita, costura)	2.376 - 6.600	66
Corredor	5,0	100 lux	-	495 - 1.375	14
Quarto 2	10,5	150 lux	300 lux (leitura na cama, penteadeira)	1.575 - 4.375	44
Banheiro 2	3,9	150 lux	300 lux (espelho (barba, maquiagem))	585 - 1.625	16
Quarto 3	11,6	150 lux	300 lux (leitura na cama, penteadeira)	1.743 - 4.842	48
Cozinha	12,5	150 lux	300 lux (fogão, pia e bancada (a EN 12464-1 pede 500))	1.868 - 5.188	52
Banheiro externo	2,6	150 lux	300 lux (lavanderia e ferramentas)	389 - 1.082	11
Depósito externo	4,1	150 lux	300 lux (lavanderia e ferramentas)	617 - 1.714	17

Calculado com: **Motor rápido (Python, deste projeto)** · detalhes e confiabilidade na seção 10

Use o extremo inferior para paredes e tetos claros e boas luminárias; o superior para cores escuras ou spots embutidos. LED a 100 lm por watt. A luz natural já cobre parte do dia (seção 2,2).

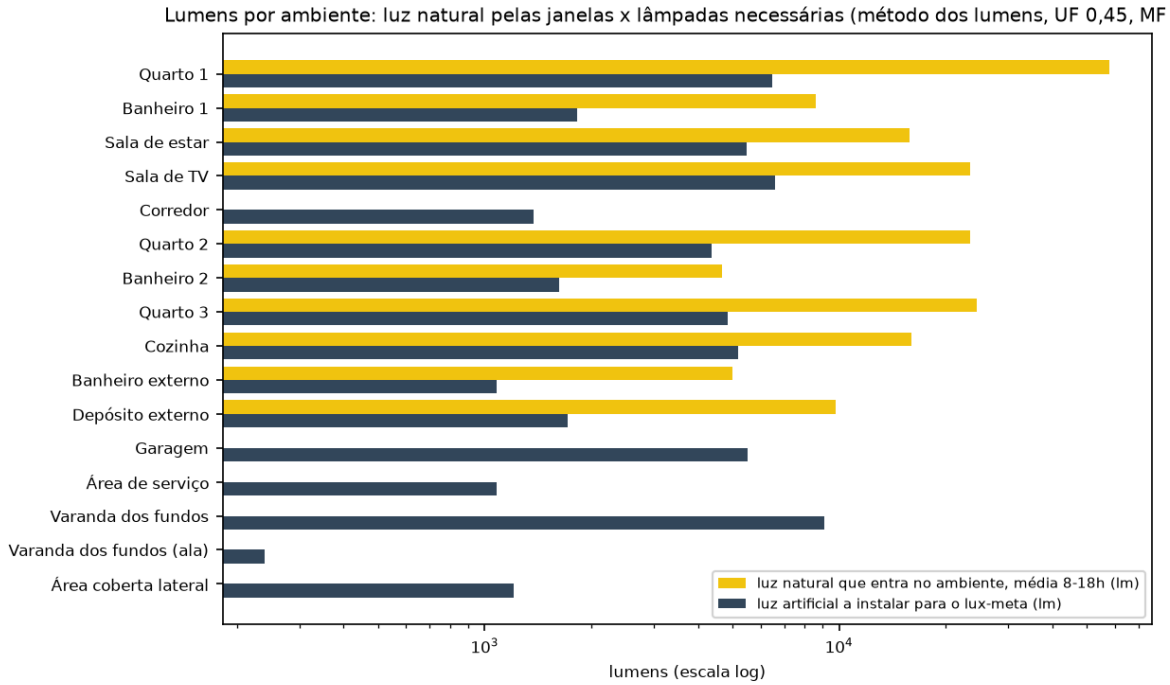

Luz natural que entra pelas janelas (amarelo) comparada com os lumens de lâmpada necessários para a luz-meta (escuro).

4. Janelas, ar fresco e vento

A NBR 15575-4 pede que a parte abrível das janelas seja de pelo menos **7% da área do piso** de cada sala e dormitório, e limita o vidro a 20% do piso, salvo se houver sombreamento. A NBR 15220-3 recomenda a ventilação cruzada pelo vento como principal estratégia de verão para este clima.

4,1 Tamanho das janelas

Ambiente	Piso m²	Vidro m²	Vidro / piso	Abrível / piso
Quarto 1	15,6	3,00	19,3% Ideal 5/5	9,6% Atende ao mínimo 3/5
Banheiro 1	4,4	0,72	16,4%	8,2%
Sala de estar	13,2	2,40	18,2% Ideal 5/5	9,1% Atende ao mínimo 3/5
Sala de TV	15,8	2,40	15,2% Ideal 5/5	7,6% Atende ao mínimo 3/5
Corredor	5,0	0,00	0,0%	0,0%
Quarto 2	10,5	2,40	22,9% Grande 4/5	11,4% Boa margem 5/5
Banheiro 2	3,9	0,60	15,4%	7,7%
Quarto 3	11,6	2,40	20,7% Grande 4/5	10,3% Boa margem 5/5
Cozinha	12,5	2,40	19,3% Ideal 5/5	9,6% Atende ao mínimo 3/5
Banheiro externo	2,6	0,49	18,9%	9,4%
Depósito externo	4,1	1,00	24,3%	12,2%


Calculado com: **Modelo 3D (IFC) e tabelas** · tamanhos lidos do modelo IFC · detalhes e confiabilidade na seção 10

Os tamanhos e alturas das janelas são os das plantas aprovadas (quartos, salas e cozinha 2,00 x 1,20 m com peitoril de 1,20 m, suíte 2,00 x 1,50 m com peitoril de 0,90 m, banheiros 1,00 x 0,60 e 1,20 x 0,60 m; anexo de 2012 1,00 x 1,00 e 0,70 x 0,70 m); supõe-se que uma janela de correr abre metade da sua área. Se as janelas construídas forem diferentes, altere-as e rode a análise de novo.


4,2 Ventilação cruzada

Ambiente	Horas com vento e corrente de ar atravessando
Quarto 1	36% Alguma 3/5
Banheiro 1	0%
Sala de estar	100% Excelente 5/5
Sala de TV	77% Excelente 5/5
Corredor	76%
Quarto 2	36% Alguma 3/5
Banheiro 2	36%
Quarto 3	36% Alguma 3/5
Cozinha	77% Excelente 5/5
Banheiro externo	0%
Depósito externo	0%

Calculado com: **Motor rápido (Python, deste projeto)** · regra de horas de vento do arquivo climático; sem cálculo de pressão (a ventilação por pressão está na seção 6,4) · detalhes e confiabilidade na seção 10

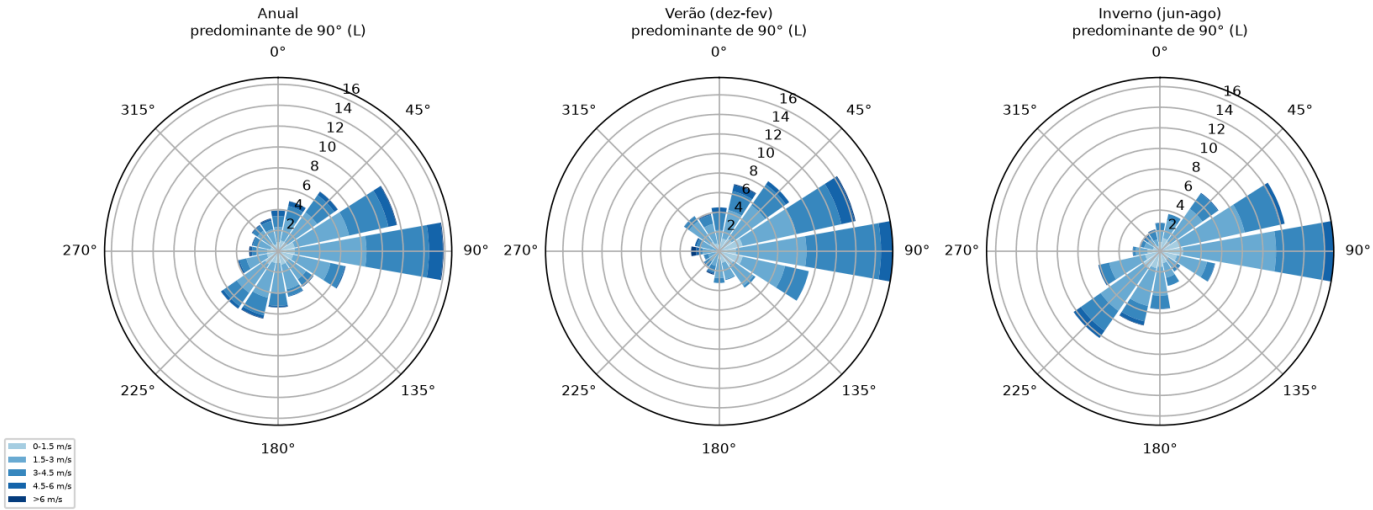

Rosas dos ventos: de onde o vento vem e com que força, ano todo, verão e inverno.

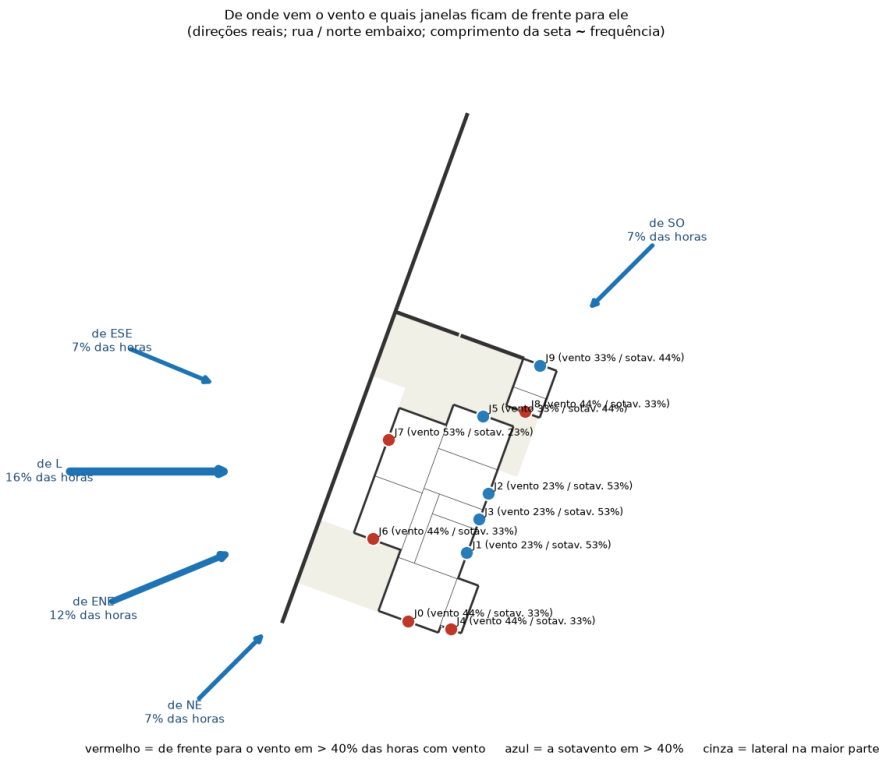

Direções do vento em relação às janelas da casa (janelas vermelhas de frente para o vento, azuis do lado protegido).

O que conta como bom? (janelas e vento)

Área de janela abrível para ventilação Norma brasileira

Área das janelas que realmente abre (descontados vidros, caixilhos e folhas fixas) dividida pela área do piso do ambiente. Nas zonas 1 a 7 é exigido pelo menos 7%.

Não atende 1/5	abaixo de 7 % da área do piso	Menos que os 7% mínimos da norma (a menos que o código de obras do município diga outra coisa).
Atende ao mínimo 3/5	7 a 10 % da área do piso	Atende ao mínimo de 7%.
Boa margem 5/5	10 ou mais % da área do piso	Mais que o mínimo: boas trocas de ar.

Esta casa: Quarto 1 9,6% Atende ao mínimo 3/5 | Sala de estar 9,1% Atende ao mínimo 3/5 | Sala de TV 7,6% Atende ao mínimo 3/5 | Quarto 2 11,4% Boa margem 5/5 | Quarto 3 10,3% Boa margem 5/5 | Cozinha 9,6% Atende ao mínimo 3/5

Fonte: Projeto de emenda da ABNT NBR 15575-4:2021 (mar/2021): método simplificado para paredes, ventilação e áreas transparentes. Supomos que uma janela de correr abre cerca da metade da sua área; janelas de abrir ou basculantes abrem mais.

Área de vidro em relação ao piso Norma brasileira

Área da janela dividida pela área do piso. A NBR 15575-4 limita as áreas transparentes a 20% do piso (ambientes até 20 m²) a menos que haja sombreamento ou vidro de alto desempenho; a NBR 15220-3 recomenda aberturas de 15 a 25% na zona 3.

Muito pequena 2/5	abaixo de 7 % da área do piso	Janela pequena demais para luz e ar.
Pequena 3/5	7 a 15 % da área do piso	Funciona, mas um pouco escuro ou abafado.
Ideal 5/5	15 a 20 % da área do piso	Dentro do limite da NBR 15575-4 e da recomendação da NBR 15220-3.
Grande 4/5	20 a 25 % da área do piso	Recomendada pela NBR 15220-3 se sombreada; acima dos 20% da NBR 15575-4, exceto se sombreada.
Grande demais 2/5	25 ou mais % da área do piso	Mais calor do sol do que as normas aceitam sem sombreamento.

Esta casa: Quarto 1 19,3% Ideal 5/5 | Sala de estar 18,2% Ideal 5/5 | Sala de TV 15,2% Ideal 5/5 | Quarto 2 22,9% Grande 4/5 | Quarto 3 20,7% Grande 4/5 | Cozinha 19,3% Ideal 5/5

Fonte: Projeto de emenda da ABNT NBR 15575-4:2021 (mar/2021): método simplificado para paredes, ventilação e áreas transparentes; ABNT NBR 15220-3: zoneamento bioclimático brasileiro e diretrizes construtivas (Maringá costuma ser listada na zona 3).

Ventilação cruzada possível Regra prática

Parcela das horas com vento em que o vento bate em uma janela de um lado dos ambientes conectados e outra janela do lado oposto deixa o ar sair (portas supostas abertas).

Quase nenhuma 1/5	abaixo de 5 % das horas com vento	O ar quase não atravessa o ambiente.
Fraca 2/5	5 a 20 % das horas com vento	A ventilação cruzada raramente acontece.
Alguma 3/5	20 a 40 % das horas com vento	Funciona em parte das horas com vento.
Boa 4/5	40 a 60 % das horas com vento	Funciona em muitas horas com vento.
Excelente 5/5	60 ou mais % das horas com vento	Uma corrente de ar atravessando a casa é possível quase sempre.

Esta casa: Quarto 1 36% Alguma 3/5 | Sala de estar 100% Excelente 5/5 | Sala de TV 77% Excelente 5/5 | Quarto 2 36% Alguma 3/5 | Quarto 3 36% Alguma 3/5 | Cozinha 77% Excelente 5/5

Fonte: Regra prática deste estudo (nenhuma norma dá um número).

Velocidade média do vento externo Padrão internacional

Vento médio no local ao longo do ano (arquivo climático, terreno aberto a 10 m; na casa é menor).

Calmaria 2/5	abaixo de 1,0 m/s	Pouca ventilação natural só pelo vento.
Aragem 3/5	1,0 a 2,0 m/s	Suave; as aberturas ajudam, mas a ventilação cruzada é fraca.
Brisa leve a suave 5/5	2,0 a 5,0 m/s	Faixa ideal para ventilação natural.
Brisa moderada 4/5	5,0 a 8,0 m/s	Forte o bastante para exigir proteção contra o vento ao ar livre.
Brisa fresca ou mais 2/5	8,0 ou mais m/s	Risco de danos e desconforto pelo vento.

Esta casa: Maringá, PR, ano todo 2,3 m/s Brisa leve a suave 5/5

Fonte: Escala de vento Beaufort (OMM); Regra prática deste estudo (nenhuma norma dá um número). Beaufort 1 = 0,3–1,5 m/s, 2 = 1,6–3,3, 3 = 3,4–5,4, 4 = 5,5–7,9 m/s. Dentro de casa, a ASHRAE 55 aceita velocidades do ar de até cerca de 0,8 m/s.


5. Temperatura e conforto

Sem ar-condicionado, o conforto depende das paredes, da cobertura, das janelas, da sombra e da ventilação. A simulação calcula a temperatura interna de cada ambiente para cada uma das 8,760 horas de um ano típico. **Confortável** significa dentro da faixa de conforto adaptativo da ASHRAE 55 (ela acompanha o clima: as pessoas aceitam ambientes mais quentes quando faz mais calor lá fora).


5,1 Horas na faixa confortável

Ambiente	Horas confortáveis	Quente demais	Frio demais	Máxima	Mínima
Quarto 1	6.487 h = 74% Aceitável 3/5	1.717 h	556 h	34,4 °C Muito quente 2/5	13,0 °C Frio 2/5
Banheiro 1	6.177 h = 70% Aceitável 3/5	1.757 h	826 h	36,2 °C Extremo 1/5	11,3 °C Perigoso 1/5
Sala de estar	6.925 h = 79% Bom 4/5	1.009 h	826 h	34,0 °C Muito quente 2/5	12,7 °C Frio 2/5
Sala de TV	6.854 h = 78% Bom 4/5	1.042 h	864 h	34,3 °C Muito quente 2/5	12,8 °C Frio 2/5
Corredor	8.174 h = 93% Excelente 5/5	0 h	586 h	29,0 °C Morno 4/5	17,1 °C Fresco 3/5
Quarto 2	6.905 h = 79% Bom 4/5	1.164 h	691 h	34,6 °C Muito quente 2/5	13,7 °C Frio 2/5
Banheiro 2	7.381 h = 84% Bom 4/5	724 h	655 h	32,7 °C Muito quente 2/5	14,6 °C Frio 2/5
Quarto 3	7.160 h = 82% Bom 4/5	947 h	653 h	33,9 °C Muito quente 2/5	14,2 °C Frio 2/5
Cozinha	6.480 h = 74% Aceitável 3/5	1.239 h	1.041 h	35,5 °C Extremo 1/5	11,6 °C Perigoso 1/5
Banheiro externo	5.984 h = 68% Aceitável 3/5	1.968 h	808 h	35,9 °C Extremo 1/5	11,0 °C Perigoso 1/5
Depósito externo	5.998 h = 68% Aceitável 3/5	1.744 h	1.018 h	36,7 °C Extremo 1/5	10,8 °C Perigoso 1/5
AO AR LIVRE (referência)	4.248 h = 48% Ruim 2/5	1.193 h	3.319 h	37,7 °C	4,2 °C

Calculado com: **Motor rápido (Python, deste projeto)** · detalhes e confiabilidade na seção 10

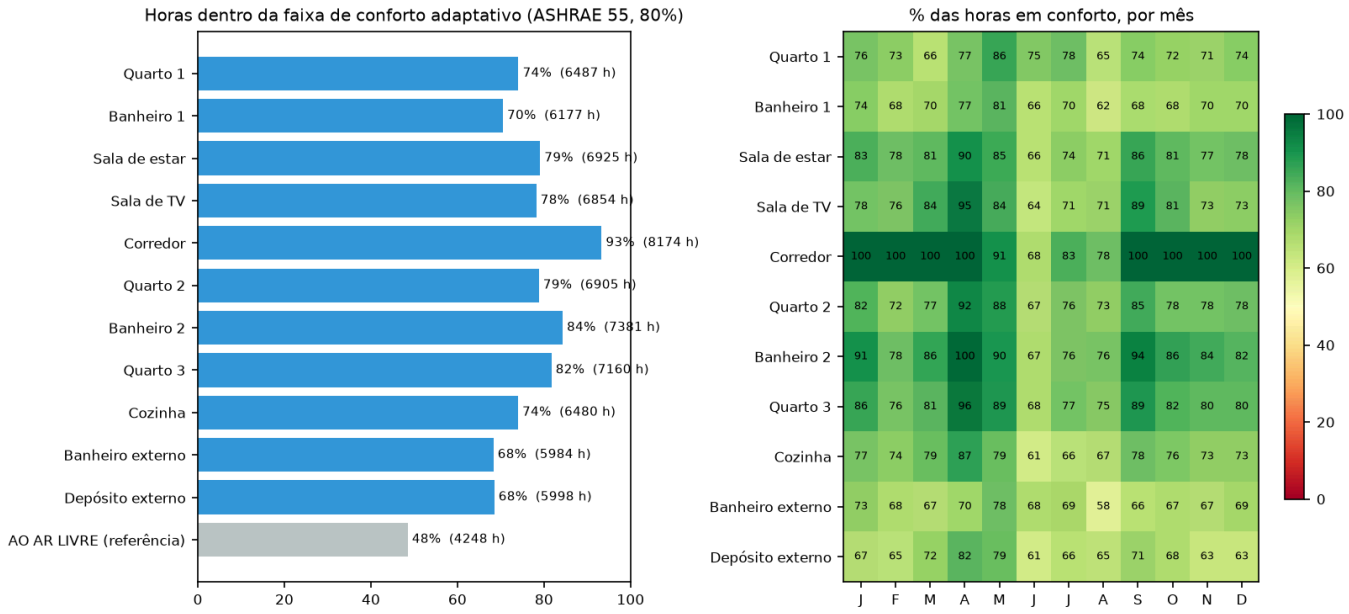

Esquerda: horas confortáveis por ambiente. Direita: parcela de horas confortáveis por mês (verde = bom, vermelho = ruim).

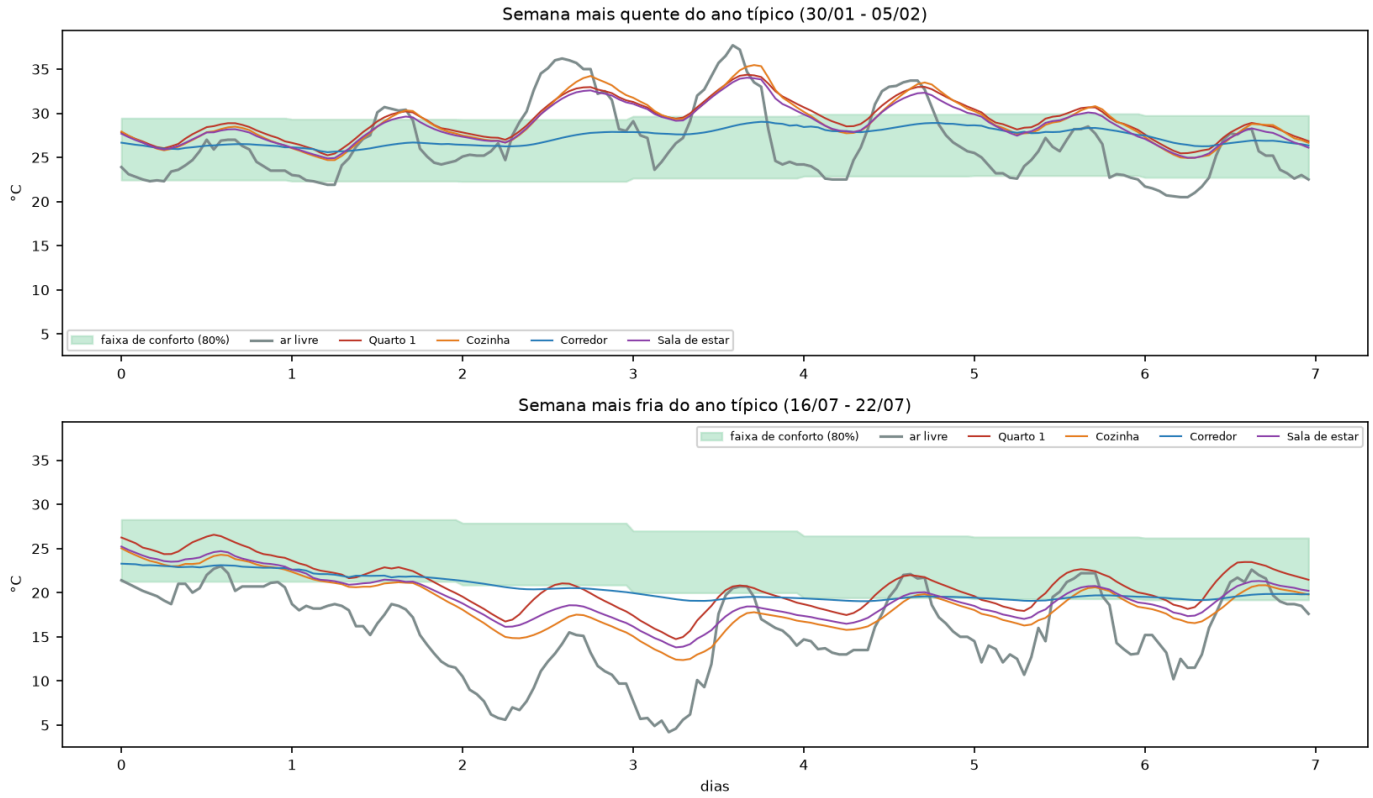

Uma semana quente e uma semana fria: temperaturas internas contra a faixa de conforto e a temperatura externa.

5,2 Verificação brasileira de dia de projeto (NBR 15575)

Dia mais quente do ano típico: **02 Fev** (37,7 °C lá fora). Dia mais frio: **19 Jul** (4,2 °C lá fora).

Ambiente	Dia mais quente: máxima interna	vs. externo	Veredito	Dia mais frio: mínima interna	vs. externo	Veredito
Quarto 1	34,5 °C	-3,2	Intermediário 4/5	14,5 °C	+10,3	Superior 5/5
Banheiro 1 *(não avaliado)*	36,3 °C	-1,4		12,3 °C	+8,1	
Sala de estar	34,1 °C	-3,6	Intermediário 4/5	13,6 °C	+9,4	Superior 5/5
Sala de TV	34,4 °C	-3,3	Intermediário 4/5	13,5 °C	+9,3	Superior 5/5
Corredor *(não avaliado)*	29,0 °C	-8,7		19,1 °C	+14,9	
Quarto 2	34,9 °C	-2,8	Intermediário 4/5	15,0 °C	+10,8	Superior 5/5
Banheiro 2 *(não avaliado)*	32,9 °C	-4,8		16,3 °C	+12,1	
Quarto 3	34,2 °C	-3,5	Intermediário 4/5	15,7 °C	+11,5	Superior 5/5
Cozinha *(não avaliado)*	35,5 °C	-2,2		12,2 °C	+8,0	
Banheiro externo *(não avaliado)*	35,9 °C	-1,8		12,1 °C	+7,9	
Depósito externo *(não avaliado)*	36,8 °C	-0,9		11,4 °C	+7,2	

Calculado com: **Motor rápido (Python, deste projeto)** · detalhes e confiabilidade na seção 10


A edição mais nova (NBR 15575-1:2021) compara a casa com uma casa de referência ao longo do ano todo; isso exige uma segunda simulação, por isso este relatório usa os critérios absolutos clássicos de dia de projeto, que são mais fáceis de entender.

5,3 Quanto custa refrigerar os ambientes no verão

Se um ambiente esquenta demais, dá para refrigerá-lo com ar-condicionado. A simulação liga um split sempre que o ambiente passa de **26 °C** nas horas em que é usado (dormitórios: 21:00-08:00, sala: 14:00-23:00, cozinha: 08:00-21:00), com as janelas fechadas, e soma a eletricidade: calor retirado ÷ COP 3,0 (um modelo inverter faz melhor) × tarifa de **R$ 1,00 por kWh** (com todos os impostos; uma suposição baseada na tarifa residencial da Copel após o reajuste de +20% de junho de 2026; altere com *run_all.bat --tariff 0,95*).

Calculado com: **Motor rápido (Python, deste projeto)** · detalhes e confiabilidade na seção 10

Ambiente	Quando é climatizado	Horas com o ar ligado	Eletricidade kWh/ano	Custo R$/ano	Custo dez-fev	Pior mês	Pico de calor a retirar	Capacidade do ar	Nível
Quarto 1 (15,6 m²)	21:00-08:00	1235	219	**R$ 219**	R$ 89	Mar (R$ 34)	2,2 kW	9.000 BTU/h	Baixa 4/5
Sala de estar (13,2 m²)	14:00-23:00	1690	325	**R$ 325**	R$ 137	Dez (R$ 48)	2,1 kW	9.000 BTU/h	Baixa 4/5
Sala de TV (15,8 m²)	14:00-23:00	1653	375	**R$ 375**	R$ 174	Dez (R$ 62)	2,5 kW	12.000 BTU/h	Baixa 4/5
Quarto 2 (10,5 m²)	21:00-08:00	1208	146	**R$ 146**	R$ 64	Fev (R$ 24)	1,6 kW	9.000 BTU/h	Baixa 4/5
Quarto 3 (11,6 m²)	21:00-08:00	1174	142	**R$ 142**	R$ 64	Fev (R$ 23)	1,6 kW	9.000 BTU/h	Baixa 4/5
Cozinha (12,5 m²)	08:00-21:00	2216	450	**R$ 450**	R$ 198	Dez (R$ 70)	1,8 kW	9.000 BTU/h	Moderada 3/5
Total			**1.657**	**R$ 1.657**					

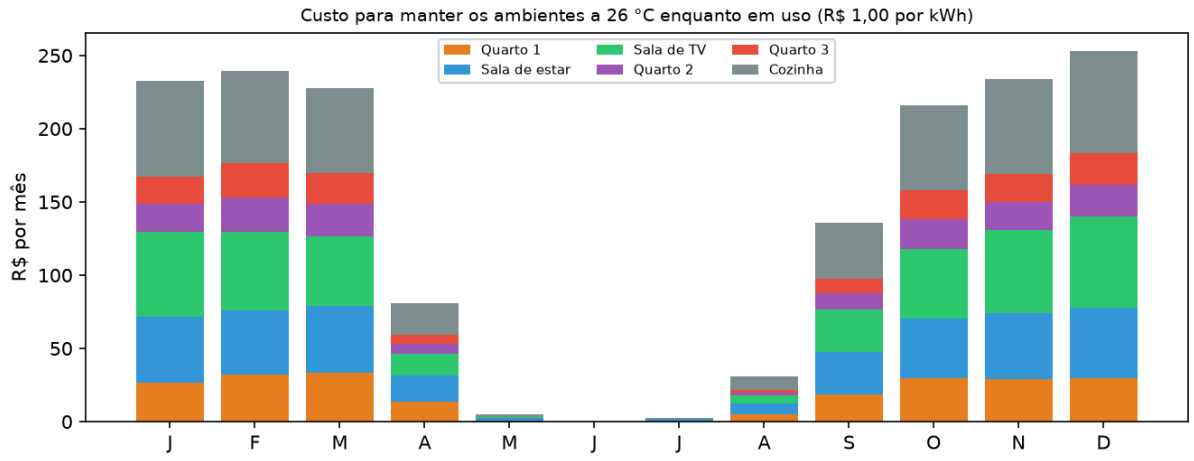

Custo mensal de climatização por ambiente.

"Pico de calor a retirar" é a potência de refrigeração necessária na hora mais quente; a capacidade do ar soma 10% e arredonda para um tamanho de catálogo (1 kW = 3,412 BTU/h). Só o calor sensível é contado (sem desumidificação), então as contas reais são um pouco maiores. Os ambientes com nível Alta ou Muito alta são onde sombra, uma cobertura melhor ou melhor isolamento se pagam mais rápido.

O que conta como bom? (temperatura, refrigeração e aquecimento)

Horas na faixa de temperatura confortável Regra prática

Parcela das 8,760 horas do ano em que a temperatura do ambiente fica dentro da faixa de conforto adaptativo da ASHRAE 55 (ela acompanha o clima: com mais calor lá fora, aceita-se mais calor dentro). Ao ar livre, como referência, só cerca de metade das horas.

Péssimo 1/5	abaixo de 40 % do ano	Desconfortável na maior parte do ano.
Ruim 2/5	40 a 60 % do ano	Desconfortável em boa parte do ano.
Aceitável 3/5	60 a 75 % do ano	Confortável na maior parte do tempo, com algumas ondas de calor ou frio.
Bom 4/5	75 a 90 % do ano	Confortável na maior parte do ano.
Excelente 5/5	90 ou mais % do ano	Confortável quase o ano todo sem ar-condicionado nem aquecimento.

Esta casa: Quarto 1 74% Aceitável 3/5 | Banheiro 1 70% Aceitável 3/5 | Sala de estar 79% Bom 4/5 | Sala de TV 78% Bom 4/5 | Corredor 93% Excelente 5/5 | Quarto 2 79% Bom 4/5 | Banheiro 2 84% Bom 4/5 | Quarto 3 82% Bom 4/5 | Cozinha 74% Aceitável 3/5 | Banheiro externo 68% Aceitável 3/5 | Depósito externo 68% Aceitável 3/5 | AO AR LIVRE (referência) 48% Ruim 2/5

Fonte: ASHRAE 55, modelo de conforto adaptativo (aceitabilidade de 80% / 90%); Regra prática deste estudo (nenhuma norma dá um número). As normas avaliam o conforto térmico em relação a uma casa de referência ou em dias de projeto; esta escala em porcentagem é nossa.

Dia mais quente: máxima interna x máxima externa (NBR 15575) Norma brasileira

No dia mais quente do ano típico, a maior temperatura do ar interno comparada com a maior temperatura externa. Negativo significa que a casa fica mais fresca que o lado de fora.

Superior 5/5	abaixo de -4 °C (máx. interna − máx. externa)	Máxima interna pelo menos 4 °C abaixo da externa.
Intermediário 4/5	-4 a -2 °C (máx. interna − máx. externa)	Máxima interna pelo menos 2 °C abaixo da externa.
Mínimo 3/5	-2 a 0,0001 °C (máx. interna − máx. externa)	Máxima interna não maior que a externa.
Não atende 1/5	0,0001 ou mais °C (máx. interna − máx. externa)	Máxima interna maior que a externa: a casa superaquece.

Esta casa: Quarto 1 -3,2 °C Intermediário 4/5 | Sala de estar -3,6 °C Intermediário 4/5 | Sala de TV -3,3 °C Intermediário 4/5 | Quarto 2 -2,8 °C Intermediário 4/5 | Quarto 3 -3,5 °C Intermediário 4/5

Fonte: ABNT NBR 15575-1:2013 (Edificações habitacionais — Desempenho), requisitos de iluminação natural e desempenho térmico. Vale para dormitórios e salas. Usamos o dia mais quente do arquivo climático, não o dia típico de projeto da norma.

Dia mais frio: mínima interna x mínima externa (NBR 15575) Norma brasileira

No dia mais frio do ano típico, a menor temperatura do ar interno comparada com a menor temperatura externa. Positivo significa que a casa fica mais quente que o lado de fora.

Não atende 1/5	abaixo de 3 °C (mín. interna − mín. externa)	Menos de 3 °C mais quente que o lado de fora.
Mínimo 3/5	3 a 5 °C (mín. interna − mín. externa)	Pelo menos 3 °C mais quente que o lado de fora.
Intermediário 4/5	5 a 7 °C (mín. interna − mín. externa)	Pelo menos 5 °C mais quente que o lado de fora.
Superior 5/5	7 ou mais °C (mín. interna − mín. externa)	Pelo menos 7 °C mais quente que o lado de fora.

Esta casa: Quarto 1 +10,3 °C Superior 5/5 | Sala de estar +9,4 °C Superior 5/5 | Sala de TV +9,3 °C Superior 5/5 | Quarto 2 +10,8 °C Superior 5/5 | Quarto 3 +11,5 °C Superior 5/5

Fonte: ABNT NBR 15575-1:2013 (Edificações habitacionais — Desempenho), requisitos de iluminação natural e desempenho térmico. A verificação de inverno é exigida nas zonas bioclimáticas 1 a 5, o que inclui Maringá.

Hora mais quente do ano dentro de casa Regra prática

Maior temperatura operativa (ar + superfícies das paredes) atingida no ambiente.

Confortável 5/5	abaixo de 28 °C	Nunca fica realmente quente.
Morno 4/5	28 a 30 °C	Quente nos dias mais quentes; um ventilador resolve.
Quente 3/5	30 a 32 °C	Períodos quentes; ventilador ajuda, o sono é afetado.
Muito quente 2/5	32 a 35 °C	Risco de estresse térmico para crianças e idosos.
Extremo 1/5	35 ou mais °C	Perigoso sem climatização.

Esta casa: Quarto 1 34,4 °C Muito quente 2/5 | Banheiro 1 36,2 °C Extremo 1/5 | Sala de estar 34,0 °C Muito quente 2/5 | Sala de TV 34,3 °C Muito quente 2/5 | Corredor 29,0 °C Morno 4/5 | Quarto 2 34,6 °C Muito quente 2/5 | Banheiro 2 32,7 °C Muito quente 2/5 | Quarto 3 33,9 °C Muito quente 2/5 | Cozinha 35,5 °C Extremo 1/5 | Banheiro externo 35,9 °C Extremo 1/5 | Depósito externo 36,7 °C Extremo 1/5

Fonte: ASHRAE 55, modelo de conforto adaptativo (aceitabilidade de 80% / 90%); Regra prática deste estudo (nenhuma norma dá um número). O limite superior do conforto adaptativo em um mês quente é cerca de 29 °C (aceitabilidade de 80%).

Hora mais fria do ano dentro de casa Padrão internacional

Menor temperatura operativa atingida no ambiente.

Perigoso 1/5	abaixo de 12 °C	Estresse por frio; risco de problemas cardíacos e respiratórios.
Frio 2/5	12 a 16 °C	Abaixo de 16 °C o risco de problemas respiratórios aumenta.
Fresco 3/5	16 a 18 °C	Precisa de agasalho; abaixo dos 18 °C recomendados pela OMS.
Bom 4/5	18 a 20 °C	Atende à recomendação da OMS de pelo menos 18 °C.
Agradável 5/5	20 ou mais °C	Nunca fica desconfortavelmente frio.

Esta casa: Quarto 1 13,0 °C Frio 2/5 | Banheiro 1 11,3 °C Perigoso 1/5 | Sala de estar 12,7 °C Frio 2/5 | Sala de TV 12,8 °C Frio 2/5 | Corredor 17,1 °C Fresco 3/5 | Quarto 2 13,7 °C Frio 2/5 | Banheiro 2 14,6 °C Frio 2/5 | Quarto 3 14,2 °C Frio 2/5 | Cozinha 11,6 °C Perigoso 1/5 | Banheiro externo 11,0 °C Perigoso 1/5 | Depósito externo 10,8 °C Perigoso 1/5

Fonte: OMS, Diretrizes de Habitação e Saúde 2018 (temperatura interna de pelo menos 18 °C).

Eletricidade para manter o ambiente fresco com ar-condicionado Regra prática

Eletricidade que um split usaria em um ano para manter o ambiente a 26 °C (limite superior da zona de conforto de verão da NBR 16401-2) nas horas em que ele é usado (dormitórios 21h–8h, sala 14h–23h, cozinha 8h–21h). Um ambiente que superaquece no verão custa mais aqui. Custo = kWh × tarifa.

Muito baixa 5/5	abaixo de 10 kWh por m² por ano	Raramente precisa de refrigeração.
Baixa 4/5	10 a 25 kWh por m² por ano	Algumas semanas de refrigeração por ano.
Moderada 3/5	25 a 45 kWh por m² por ano	Refrigeração necessária na maior parte do verão.
Alta 2/5	45 a 70 kWh por m² por ano	Caro para manter fresco: o ambiente superaquece muito.
Muito alta 1/5	70 ou mais kWh por m² por ano	Muito caro: sombreamento, isolamento ou uma cobertura melhor valem mais que um ar-condicionado maior.

Esta casa: Quarto 1 14,1 kWh/m² Baixa 4/5 | Sala de estar 24,6 kWh/m² Baixa 4/5 | Sala de TV 23,7 kWh/m² Baixa 4/5 | Quarto 2 13,9 kWh/m² Baixa 4/5 | Quarto 3 12,2 kWh/m² Baixa 4/5 | Cozinha 36,1 kWh/m² Moderada 3/5

Fonte: Regra prática deste estudo (nenhuma norma dá um número); ABNT NBR 16401-2 (ar-condicionado, conforto interno): verão cerca de 22,5–25,5 °C com 65% de UR e 23–26 °C com 35% de UR. Considera COP 3,0 (split classe A do Inmetro de cerca de 2012), janelas fechadas com o ar ligado e só calor sensível (sem desumidificação); portanto as contas reais são um pouco maiores. A tarifa é uma suposição; veja o relatório.


6. Sol por fora, paredes e cobertura

Nesta latitude o sol do meio-dia fica sempre na metade norte do céu, então as paredes voltadas para o norte recebem o sol de inverno (bom) e pouco sol de verão, enquanto as paredes leste e oeste recebem muito sol de verão (ruim).

6,1 Energia solar em cada superfície (kWh por m², sem sombra)


Superfície	Ano todo	Verão (dez-fev)	Inverno (jun-ago)
Parede norte	1066	155 Moderado 4/5	356 Alto 5/5
Parede leste	1004	287 Alto 3/5	204 Moderado 3/5
Parede sul	507	179 Moderado 4/5	86 Baixo 2/5
Parede oeste	982	279 Alto 3/5	191 Moderado 3/5
Cobertura (horizontal)	1865	536	351

Calculado com: **Motor rápido (Python, deste projeto)** · detalhes e confiabilidade na seção 10

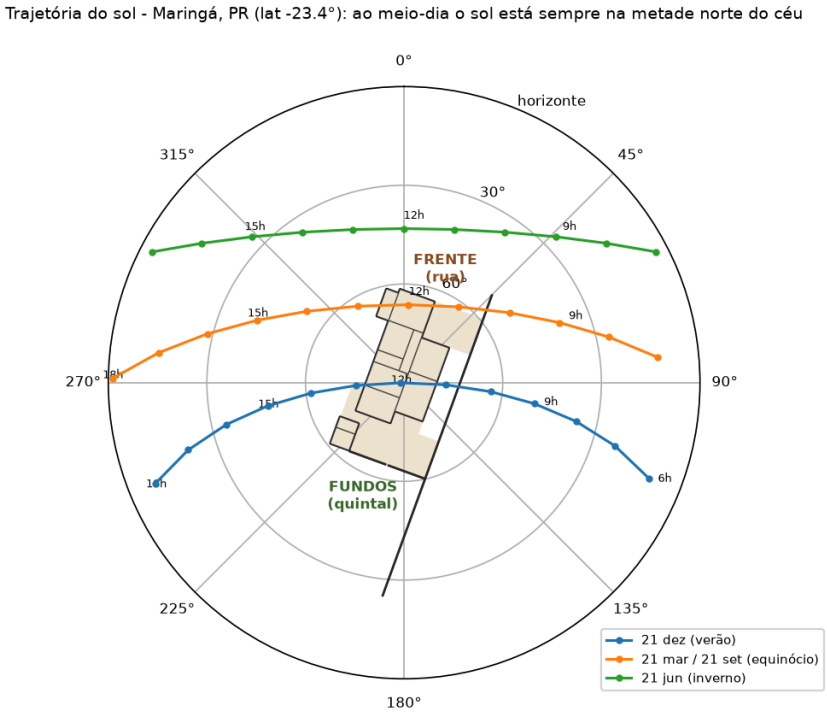

A planta da casa está desenhada no centro, na orientação real; o tamanho dela não está em escala com os ângulos do céu.

Trajetória do sol ao longo do ano com a casa desenhada no centro, na orientação real: a frente (rua) é voltada para o norte e os fundos para o sul.

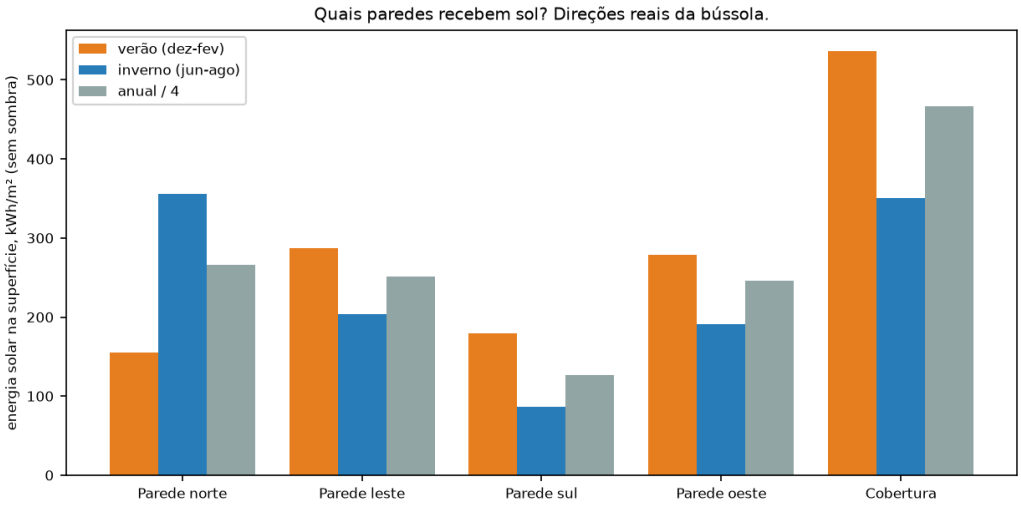

Energia solar em cada parede por estação.

6,2 As paredes e a cobertura atendem à NBR 15575?

Item	Esta casa	Limite (NBR 15575)	Resultado
Transmitância térmica U da parede externa Bloco cerâmico furado de 8 furos 9x19x19 cm + 2 cm de reboco nos dois lados = parede de 13 cm (bloco padrão brasileiro) (absortância da pintura / cobertura 0,45)	2,52 W/m²K	<= 3,7	atende
Capacidade térmica da parede externa Bloco cerâmico furado de 8 furos 9x19x19 cm + 2 cm de reboco nos dois lados = parede de 13 cm (bloco padrão brasileiro) (absortância da pintura / cobertura 0,45)	134 kJ/m²K	>= 130	atende
Transmitância térmica U da cobertura (indicativa) Telha cerâmica + sótão + laje de concreto de 12 cm (absortância da pintura / cobertura 0,7)	1,78 W/m²K	<= 1,5	não atende

Calculado com: **Motor rápido (Python, deste projeto)** · detalhes e confiabilidade na seção 10

6,3 E se os materiais mudarem?

Calculado com: **Motor rápido (Python, deste projeto)** · detalhes e confiabilidade na seção 10

Numa casa pronta é muito difícil trocar as paredes, mas a cobertura muitas vezes pode ser melhorada; por isso as duas são mostradas separadamente (cada uma com a outra parte mantida como é hoje). Melhorias de cobertura, como lã isolante, estão na seção 7.

Paredes


Cobertura mantida: Clay tile + roof void + 12 cm concrete slab ceiling

Paredes	Média de horas confortáveis	Quente demais	Frio demais	Conta de resfriamento	vs. atual
Bloco de concreto celular autoclavado de 15 cm + 1 cm de reboco nos dois lados = parede de 17 cm	7.247 h = 83% Bom 4/5	865 h	648 h	R$ 1.041/ano	R$ -616/ano
Tijolo ecológico (solo-cimento) de 12,5 cm + 2 cm de reboco nos dois lados = parede de 16,5 cm	7.072 h = 81% Bom 4/5	1.021 h	667 h	R$ 1.687/ano	+R$ 30/ano
Bloco de concreto celular autoclavado de 10 cm + 1 cm de reboco nos dois lados = parede de 12 cm	7.026 h = 80% Bom 4/5	1.028 h	706 h	R$ 1.198/ano	R$ -459/ano
Tijolo cerâmico furado de 14 cm + 2 cm de reboco nos dois lados = parede de 18 cm (mais espessa, “tijolo 6 furos em pé”)	7.016 h = 80% Bom 4/5	1.039 h	705 h	R$ 1.448/ano	R$ -209/ano
Bloco de concreto de 14 cm + 1,5 cm de reboco nos dois lados = parede de 17 cm	6.984 h = 80% Bom 4/5	1.071 h	705 h	R$ 1.626/ano	R$ -31/ano
Steel frame: placa cimentícia de 10 mm + 90 mm de lã de vidro + gesso acartonado de 12,5 mm = parede de 11,3 cm	6.856 h = 78% Bom 4/5	1.176 h	728 h	R$ 969/ano	R$ -688/ano
Tijolo ecológico (solo-cimento) de 12,5 cm, sem reboco, aparente = parede de 12,5 cm	6.810 h = 78% Bom 4/5	1.197 h	753 h	R$ 1.877/ano	+R$ 220/ano
Bloco cerâmico furado de 8 furos 9x19x19 cm + 2 cm de reboco nos dois lados = parede de 13 cm (bloco padrão brasileiro) **(atual)**	6.775 h = 77% Bom 4/5	1.210 h	775 h	R$ 1.657/ano	-

Cobertura / forro

Paredes mantidas: Ceramic hollow brick 8-hole 9x19x19 cm + 2 cm plaster both sides = 13 cm wall (standard Brazilian block)

Cobertura / forro	Média de horas confortáveis	Quente demais	Frio demais	Conta de resfriamento	vs. atual
Telha sanduíche isolada (aço + núcleo de PIR de 30 mm), sem sótão	6.953 h = 79% Bom 4/5	942 h	865 h	R$ 1.068/ano	R$ -589/ano
Telha cerâmica + sótão + laje de concreto de 12 cm **(atual)**	6.775 h = 77% Bom 4/5	1.210 h	775 h	R$ 1.657/ano	-
Laje de concreto impermeabilizada atrás de platibanda (casa “caixote”), sem sótão	6.535 h = 75% Aceitável 3/5	1.438 h	787 h	R$ 1.936/ano	+R$ 279/ano
Telha de fibrocimento + sótão + forro de PVC (cobertura leve)	6.237 h = 71% Aceitável 3/5	1.510 h	1.012 h	R$ 1.774/ano	+R$ 117/ano
Telha cerâmica + sótão + forro de gesso	6.119 h = 70% Aceitável 3/5	1.641 h	1.000 h	R$ 1.920/ano	+R$ 263/ano

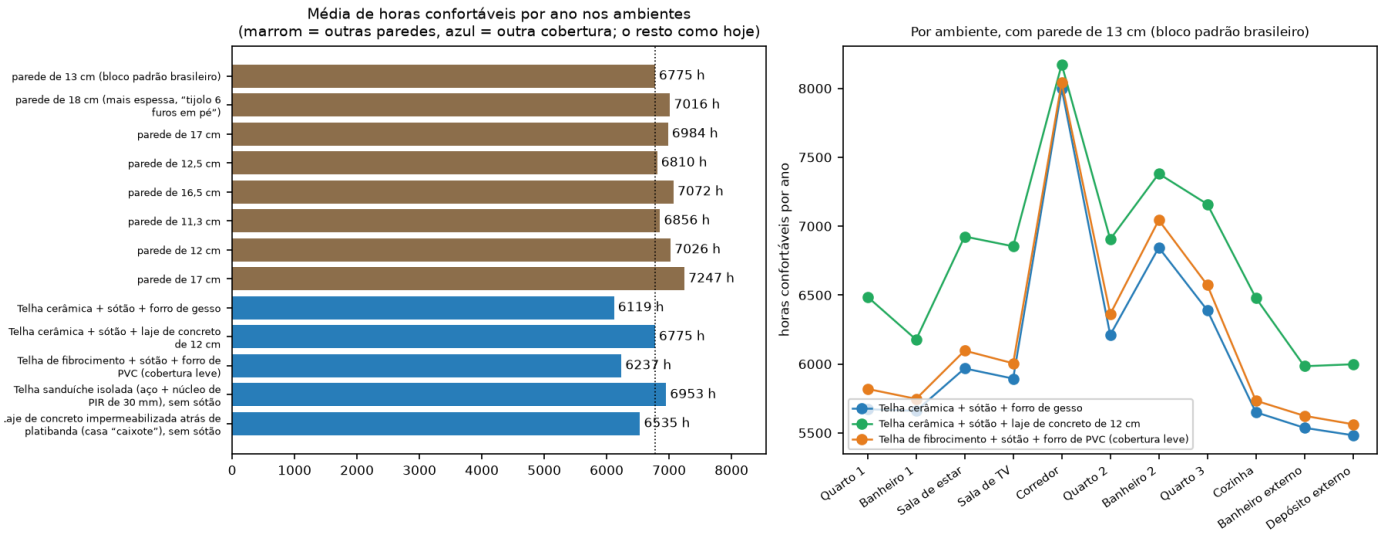

Horas confortáveis com paredes e coberturas diferentes.

O que conta como bom? (sol e construção)

Sol de verão na parede Regra prática

Energia solar em uma parede vertical sem sombra nos três meses de verão (dez–fev no sul, jun–ago no norte). Quanto menor, melhor: é calor que você não quer.

Baixo 5/5	abaixo de 150 kWh/m²	Pouco calor do sol no verão.
Moderado 4/5	150 a 225 kWh/m²	Algum calor; um beiral ou cor clara resolvem.
Alto 3/5	225 a 300 kWh/m²	Parede quente: precisa de sombra, cor clara ou isolamento.
Muito alto 2/5	300 ou mais kWh/m²	Parede muito quente.

Esta casa: Parede norte 155 Moderado 4/5 | Parede leste 287 Alto 3/5 | Parede sul 179 Moderado 4/5 | Parede oeste 279 Alto 3/5

Fonte: Regra prática deste estudo (nenhuma norma dá um número). Aproximadamente 1,7 / 2,5 / 3,3 kWh/m² por dia. A norma trata o calor das paredes por limites de transmitância térmica e cor da pintura.

Sol de inverno na parede Regra prática

Energia solar em uma parede vertical nos três meses de inverno (jun–ago no sul, dez–fev no norte). Quanto maior, melhor em um inverno fresco: calor de graça (a NBR 15220-3 recomenda aquecimento solar passivo no inverno para a zona 3).

Baixo 2/5	abaixo de 120 kWh/m²	Quase nenhum sol no inverno.
Moderado 3/5	120 a 220 kWh/m²	Algum sol no inverno.
Bom 4/5	220 a 320 kWh/m²	Bom sol no inverno.
Alto 5/5	320 ou mais kWh/m²	Muito calor grátis no inverno.

Esta casa: Parede norte 356 Alto 5/5 | Parede leste 204 Moderado 3/5 | Parede sul 86 Baixo 2/5 | Parede oeste 191 Moderado 3/5

Fonte: Regra prática deste estudo (nenhuma norma dá um número); ABNT NBR 15220-3: zoneamento bioclimático brasileiro e diretrizes construtivas (Maringá costuma ser listada na zona 3).

Transmitância térmica U da parede (NBR 15575-4) Norma brasileira

Com que rapidez o calor atravessa a parede (menor = mais isolada). Limite nas zonas 3 a 8: 3,7 se a pintura externa for clara (absortância solar até 0,6) e 2,5 se for mais escura.

Atende aos dois limites 5/5	abaixo de 2,5 W/m²K	Atende ao limite mesmo com pintura escura.
Só com pintura clara 4/5	2,5 a 3,7 W/m²K	Atende ao limite apenas com pintura de cor clara (absortância 0,6 ou menos).
Não atende 1/5	3,7 ou mais W/m²K	Acima do limite: o método simplificado não é atendido.

Esta casa: Transmitância térmica U da parede externa 2,52 (limite <= 3,7) Só com pintura clara 4/5

Fonte: Projeto de emenda da ABNT NBR 15575-4:2021 (mar/2021): método simplificado para paredes, ventilação e áreas transparentes.

Capacidade térmica da parede (NBR 15575-4) Norma brasileira

Quanto calor a parede armazena (maior = temperatura interna mais estável). Limite: pelo menos 130 nas zonas 1 a 7.

Não atende 1/5	abaixo de 130 kJ/m²K	Menos armazenamento de calor que o mínimo.
Atende 5/5	130 ou mais kJ/m²K	Atende ao mínimo de 130.

Esta casa: Capacidade térmica da parede externa 134 (limite >= 130) Atende 5/5

Fonte: Projeto de emenda da ABNT NBR 15575-4:2021 (mar/2021): método simplificado para paredes, ventilação e áreas transparentes.

Transmitância térmica U da cobertura (NBR 15575-5) Norma brasileira

Fluxo de calor pela cobertura + forro. Limite nas zonas 3 a 6: 2,3 se a cobertura for clara (absortância até 0,6) e 1,5 se for escura (por exemplo, telha cerâmica vermelha).

Atende aos dois limites 5/5	abaixo de 1,5 W/m²K	Atende ao limite mesmo para cobertura escura.
Só cobertura clara 4/5	1,5 a 2,3 W/m²K	Atende ao limite apenas se a superfície da cobertura for clara.
Não atende 1/5	2,3 ou mais W/m²K	Acima do limite.

Esta casa: Transmitância térmica U da cobertura (indicativa) 1,78 (limite <= 1,5) Só cobertura clara 4/5

Fonte: Projeto de emenda da ABNT NBR 15575-5:2021: método simplificado para coberturas. O U da nossa cobertura é indicativo: o cálculo padrão não modela um sótão ventilado.

6,4 Desempenho térmico pela NBR 15575-1:2021 por simulação (PHFT)

Calculado com: **EnergyPlus** + **AirflowNetwork** + **OpenFOAM (CFD)** · o EnergyPlus resolve o calor e o fluxo de ar, o OpenFOAM dá a pressão do vento nas aberturas · detalhes e confiabilidade na seção 10

A edição 2021 da NBR 15575-1 julga o desempenho térmico de uma moradia por simulação computacional: a casa como projetada (**modelo real**) é comparada com a mesma casa construída com materiais de referência (**modelo de referência**: paredes e pisos de 100 mm, cobertura de telha + câmara de ar + laje de 100 mm, janelas com 17% da área do piso, sem sombreamento fixo). O indicador principal é o **PHFT**, a porcentagem das horas ocupadas com temperatura operativa entre 18 e 26 °C (faixa dos climas com média anual abaixo de 25 °C: este arquivo climático tem 23,0 °C), nos dormitórios e na sala, com as janelas abertas apenas quando o ambiente está ocupado e o ar interno está a pelo menos 19 °C e mais quente que o externo. A norma também limita a temperatura operativa máxima e mínima e, nos níveis intermediário e superior, exige redução da carga térmica anual de aquecimento e refrigeração (ar-condicionado ideal a 23 °C / 21 °C quando ocupado).

Ambiente	PHFT real	PHFT referência	Horas de calor %	Horas de frio %	T_{max} / T_{min} real
Quarto 1	72,7%	67,6%	25,2	2,1	32,1 / 15,5 °C
Sala de estar	37,2%	22,5%	61,4	1,4	35,3 / 16,1 °C
Sala de TV	38,4%	33,4%	60,0	1,6	35,4 / 15,8 °C
Quarto 2	69,2%	63,7%	29,0	1,8	32,5 / 16,3 °C
Quarto 3	62,4%	57,6%	34,8	2,8	32,8 / 16,2 °C

Resultado para a casa como está: PHFT da moradia = 56,0% contra 49,0% da referência (o nível mínimo exige mais de 90% da referência: **sim**). Temperatura operativa máxima 35,4 °C contra 37,6 °C da referência, com tolerância de +2 °C: **sim**. Mínima 15,5 °C contra 13,9 °C, com tolerância de −1 °C: **sim**. Carga térmica total 6.252 kWh/ano contra 8.756 kWh/ano da referência (28,6% menor). Nível atingido: **Mínimo**.

Pacote	PHFT real	ΔPHFT (necessário 16,6)	T_{max}	T_{min}	Redução da carga	Nível
Situação atual	56,0%	7,0	35,4	15,5	28,6%	**Mínimo**
Lã de rocha 50 mm	63,2%	14,3	33,1	16,7	49,9%	**Mínimo**
Lã de vidro 50 mm	63,6%	14,6	33,0	16,8	50,5%	**Mínimo**
Lã de PET 50 mm	63,6%	14,6	33,1	16,8	50,5%	**Mínimo**
Lã de ovelha 50 mm	63,6%	14,7	33,1	16,8	50,5%	**Mínimo**
Lã de rocha 100 mm	64,8%	15,8	32,8	16,9	53,4%	**Mínimo**
Vedação das esquadrias	56,0%	7,0	35,4	15,5	28,6%	**Mínimo**
Vidro duplo	56,1%	7,1	35,3	15,8	29,4%	**Mínimo**
Vidro duplo low-E	57,7%	8,8	35,0	15,8	34,2%	**Mínimo**
Brise fixo 0,6 m	56,5%	7,6	35,3	15,5	30,1%	**Mínimo**
Persianas móveis	57,2%	8,2	35,3	15,3	32,1%	**Mínimo**
Tudo junto	67,9%	18,9	32,6	16,9	59,4%	**Superior**

O nível intermediário exige ΔPHFT de pelo menos 45 − 0,58 × PHFT da referência (casa unifamiliar) e a redução de carga da tabela 20; o superior exige o mesmo ΔPHFT e redução de 35% (carga da referência abaixo de 100 kWh/m²·ano) ou 55% (acima), ou PHFT de 95% ou mais. Vedação, vidro e sombreamento quase não mexem nos indicadores; o isolamento da cobertura é o que aproxima a casa dos níveis mais altos (ΔPHFT necessário 16,6; as lãs de 50 mm chegam a 14,7). Níveis atingidos: Tudo junto (Superior). Um pacote que cai exatamente no valor necessário está no limite: o resultado muda com pequenas alterações do modelo.

Os níveis da norma e o que significam para morar na casa

Nível	O que a norma exige	Como é morar na casa	Nesta casa
Não atendido	O PHFT é 90% da casa de referência ou menos, ou a temperatura operativa máxima / mínima é pior que a da referência em mais de 2 °C / 1 °C.	A casa é claramente pior que a referência da norma: mais tardes quentes e noites frias dentro de casa, e o ar-condicionado precisa garantir o conforto na maior parte do ano.	Nenhum pacote chega a ele.
Mínimo	PHFT acima de 90% da casa de referência; temperatura operativa máxima no máximo 2 °C acima da referência e mínima no máximo 1 °C abaixo dela.	Tão confortável quanto uma casa feita com os materiais de referência (paredes de 100 mm, cobertura de telha e laje). Nas tardes quentes e nas madrugadas frias os ambientes saem da faixa de 18 a 26 °C; espere usar ventilador ou ar-condicionado em muitos dias e agasalho nas manhãs frias.	**Casa atual**: PHFT 56,0% contra 49,0% da referência (ΔPHFT 7,0), redução de carga de 28,6%.
Intermediário	Tudo do nível mínimo, mais um ganho de PHFT sobre a casa de referência (ΔPHFT) de pelo menos 45 − 0,58 × PHFT da referência (casa unifamiliar) e uma redução da carga térmica anual de aquecimento e refrigeração (tabela 20).	Bem mais horas na faixa confortável sem nenhum equipamento, ambientes mais frescos à tarde e mais quentes de madrugada, e conta de ar-condicionado menor. O ar-condicionado passa a ser um reforço nos dias mais quentes, e não uma necessidade diária.	Nenhum pacote chega a ele.
Superior	Tudo do nível intermediário, com redução de carga de 35% (carga da referência abaixo de 100 kWh/m²·ano) ou 55% (acima), ou um PHFT de 95% ou mais.	A casa mantém uma temperatura confortável quase sozinha: poucas horas de calor ou frio, o ar-condicionado raramente é necessário e, quando é, um aparelho pequeno basta. É o nível que se paga na conta de luz.	Atingido por **Tudo junto**: PHFT 67,9%, ΔPHFT 18,9, redução de carga de 59,4%.

A coluna 'Nesta casa' usa os resultados desta simulação; a descrição de como é morar na casa é a nossa leitura dos números, não texto da norma.

Ventilação cruzada (induzida pelo vento)

A ventilação natural é resolvida pela rede de fluxo de ar (AirflowNetwork) do EnergyPlus: cada janela, porta aberta e fresta é um caminho de ar cuja pressão vem do vento (coeficientes de pressão de cada abertura, calculados pelo CFD do OpenFOAM para 24 direções), da diferença de temperatura e da altura da abertura. Trocas de ar por hora pelas janelas e portas externas, casa atual:

Calculado com: **EnergyPlus** + **AirflowNetwork** + **OpenFOAM (CFD)** · fluxo de ar pelo AirflowNetwork com coeficientes de pressão do CFD · detalhes e confiabilidade na seção 10


Ambiente	ACH médio	Percentil 90	Horas acima de 5 ACH
Quarto 1	5,5	16,0	3.415
Banheiro 1	4,2	5,8	2.746
Sala de estar	2,0	8,3	1.953
Sala de TV	1,5	6,8	1.568
Quarto 2	7,3	23,3	3.444
Banheiro 2	4,3	5,9	2.926
Quarto 3	3,6	9,9	3.380
Cozinha	0,3	0,5	0

Como o ar circula pela casa

Calculado com: **EnergyPlus** + **AirflowNetwork** + **OpenFOAM (CFD)** · rede de fluxo de ar do EnergyPlus com os coeficientes de pressão do CFD do OpenFOAM · detalhes e confiabilidade na seção 10

A rede de fluxo de ar dá, para cada hora, o volume de ar que atravessa cada janela, porta e abertura. A figura mostra a média desses fluxos na planta, para todas as horas com as janelas abertas e para as horas quentes (temperatura operativa acima de 26 °C); as setas são azuis onde entra ar fresco, vermelhas onde o ar sai da casa, laranja para o ar que passa entre ambientes, e a espessura segue a vazão em m³/h. É o fluxo entre ambientes (um nó de ar por ambiente), não um campo de velocidades dentro de cada ambiente: mostra quais aberturas alimentam a casa e por onde o ar sai, não a corrente de ar num ponto.

Como o ar se move pela casa (fluxo líquido de cada abertura) — m³/h

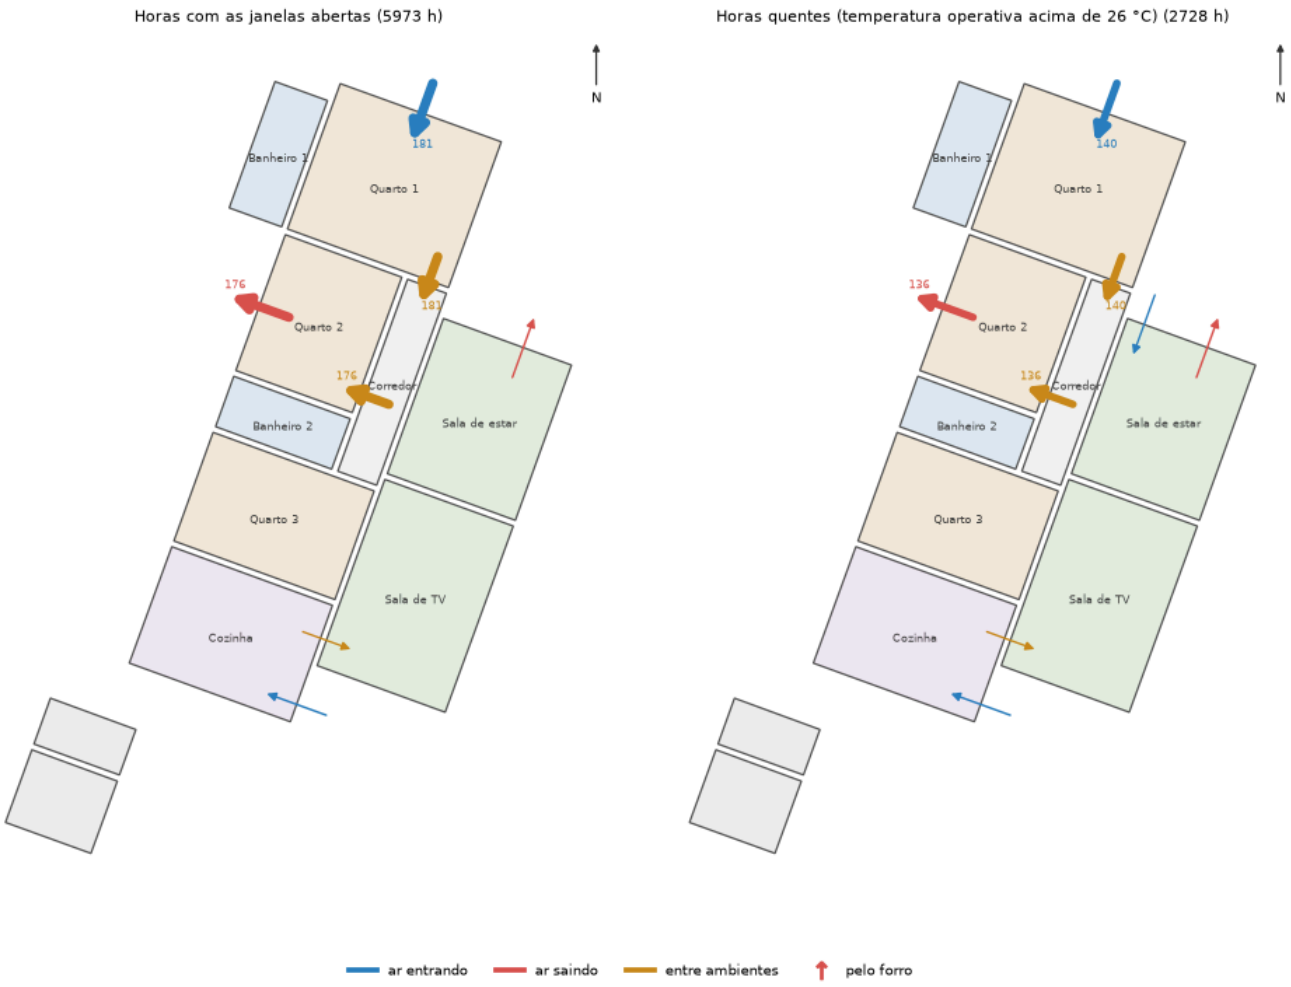

Abertura	Tipo	O ar vai de	para	m³/h
janela 1 · Quarto 1	janela	exterior	Quarto 1	140
porta 5 · Quarto 1	porta	Quarto 1	Corredor	140
janela 1 · Quarto 2	janela	Quarto 2	exterior	136
porta 7 · Corredor	porta	Corredor	Quarto 2	136


Principais caminhos do ar da casa atual nas horas quentes (vazões abaixo de 20 m³/h omitidas).

Circulação para cada direção do vento

> Calculado com: **EnergyPlus** + **AirflowNetwork** + **OpenFOAM (CFD)** · rede de fluxo de ar do EnergyPlus com os coeficientes de pressão do CFD do OpenFOAM · detalhes e confiabilidade na seção 10

Os mesmos fluxos, separados pela direção de onde o vento vem (oito setores de 45°, vento do arquivo climático). A pressão em cada abertura vem dos 24 casos de CFD; por isso o padrão muda com o vento: as aberturas a barlavento alimentam a casa e as de sotavento ou sob sucção deixam o ar sair.

Fluxo de ar para cada direção do vento (horas com as janelas abertas) — m³/h

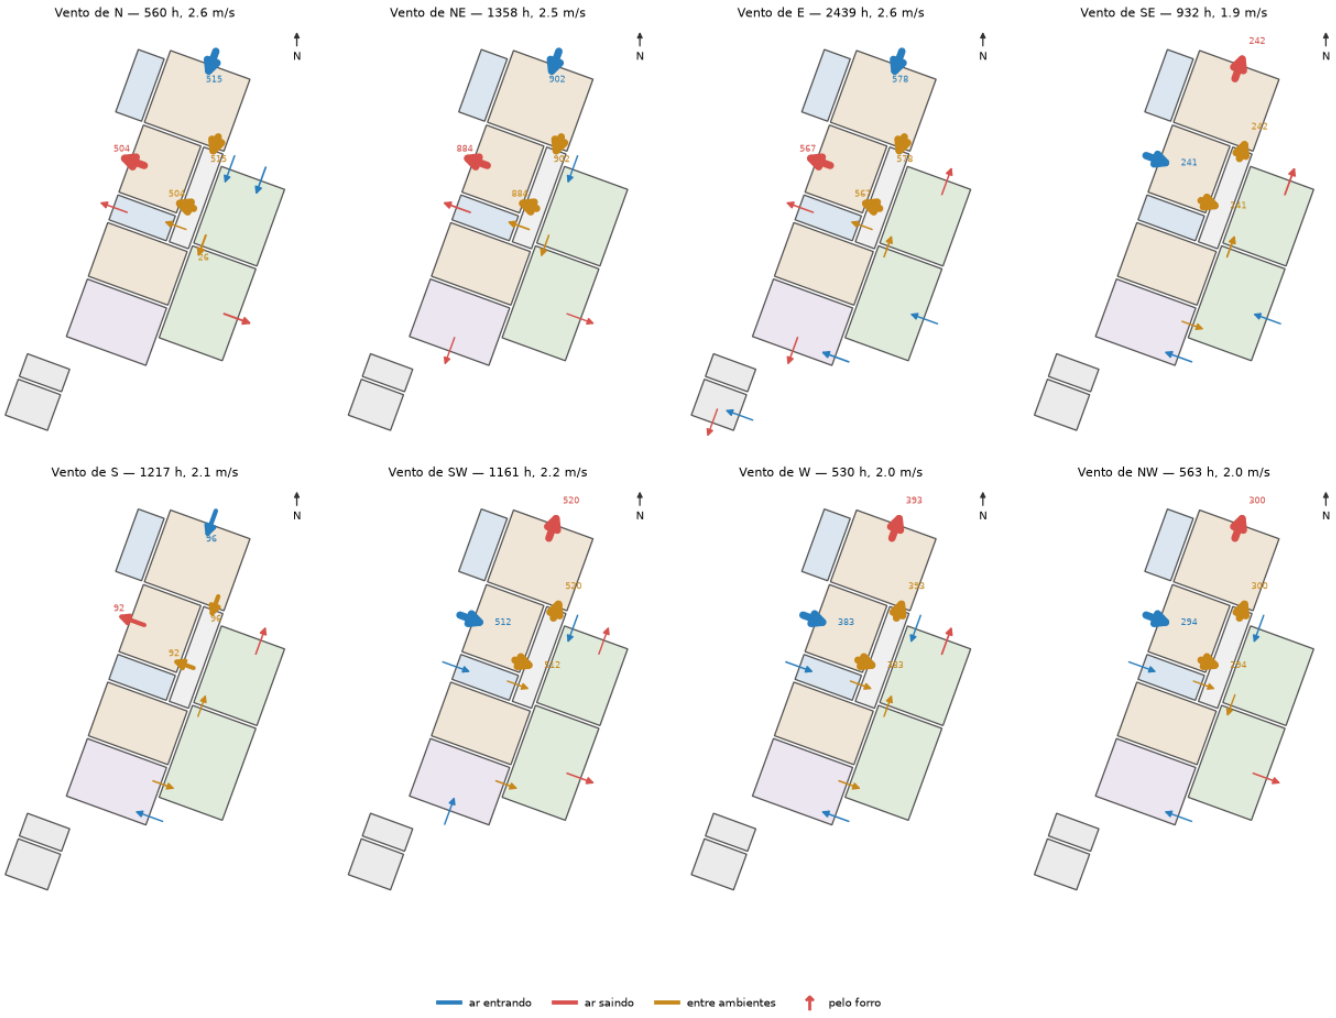



Alterações da planta que melhoram ou pioram a ventilação

> Calculado com: **EnergyPlus** + **AirflowNetwork** + **OpenFOAM (CFD)** · rede de fluxo de ar do EnergyPlus com os coeficientes de pressão do CFD do OpenFOAM · detalhes e confiabilidade na seção 10

Cada alteração é uma nova simulação do ano inteiro do mesmo modelo, com o mesmo clima, a mesma ocupação e as mesmas pressões do CFD; só muda a abertura em questão. A tabela compara o conforto e a exaustão do ar quente, nas horas ocupadas dos quartos e da sala.

Alteração	PHFT	Mais quente °C	Graus-hora acima de 26 °C	Trocas de ar por hora nas horas quentes	Efetividade de exaustão η	Calor retirado (kWh/ano)
Casa como está Janelas de correr (50% abertas), portas dos quartos e da sala abertas enquanto o ambiente está ocupado.	56,0%	35,4	3.503	9,8	0,41	8.796
Portas fechadas (pior) As portas entre os quartos / sala e o resto da casa ficam fechadas: o ar não tem por onde passar.	53,5% (-2,5)	35,5	3.709 (+206)	7,8 (-1,9)	0,37 (-0,04)	7.847 (-949)
Portas fechadas + grelha acima de cada porta As mesmas portas fechadas, com uma grelha permanente de 0,5 x 0,4 m acima de cada uma (a bandeira ventilada usual).	53,7% (-2,3)	35,5	3.701 (+198)	7,9 (-1,8)	0,37 (-0,03)	8.024 (-772)
Janelas de abrir (90% abertas) Janelas que abrem 90% da área envidraçada (de abrir ou maxim-ar) no lugar dos 50% das de correr; mesmo tamanho e caixilho.	58,7% (+2,7)	35,3	3.120 (-383)	14,3 (+4,6)	0,47 (+0,07)	9.824 (+1028)
Exaustão do ar quente pelo forro Uma grelha de 0,2 m2 no forro de cada quarto e da sala, e aberturas de beiral do ático 5 vezes maiores (2% da área do piso, em vez de 0,4%).	56,8% (+0,8)	35,2	3.274 (-229)	10,9 (+1,2)	0,45 (+0,04)	12.256 (+3460)
Janelas de abrir + exaustão pelo forro Janelas de abrir (90%) junto com as grelhas no forro e as aberturas de beiral maiores.	59,3% (+3,3)	35,1	2.954 (-549)	15,3 (+5,6)	0,50 (+0,10)	13.215 (+4419)

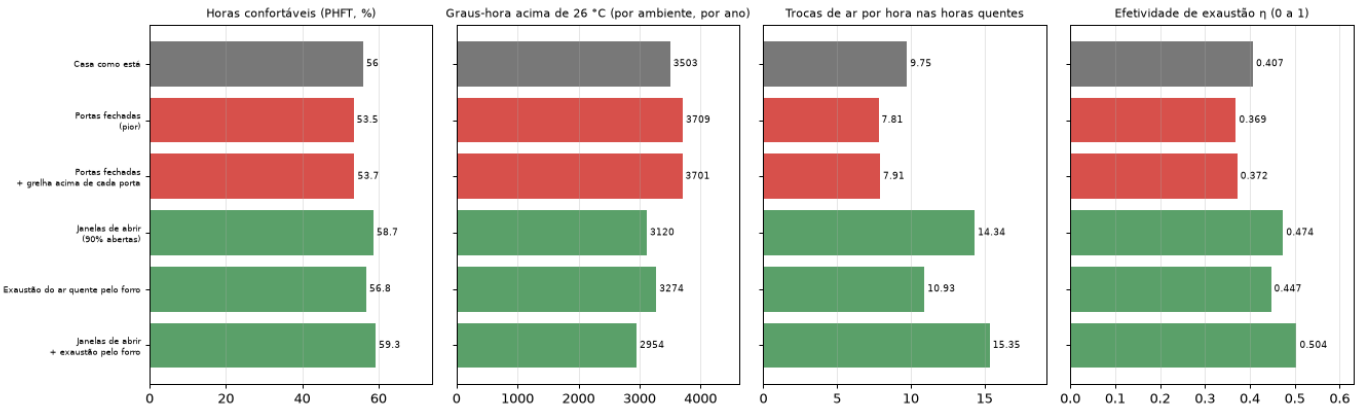

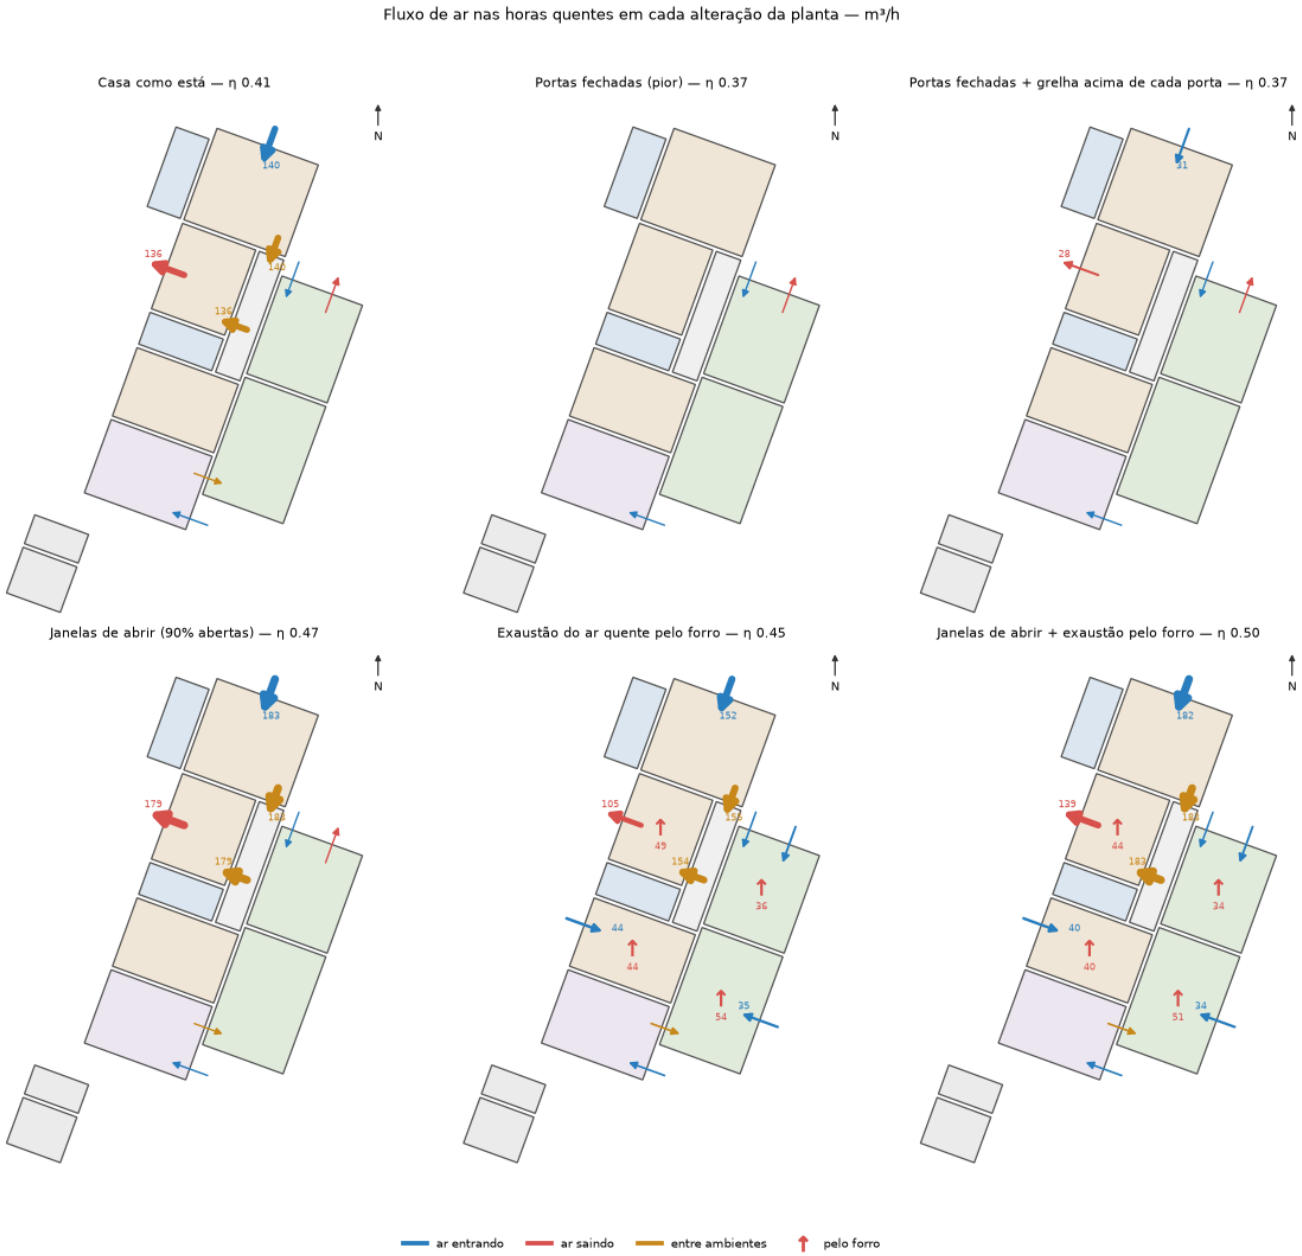

Leitura: a melhor alteração para o conforto é **Janelas de abrir + exaustão pelo forro** (PHFT 59,3% contra 56,0%, efetividade de exaustão 0,50 contra 0,41); a pior é **Portas fechadas (pior)** (PHFT 53,5%). A casa de referência tem PHFT 49,0%.

Efetividade da exaustão do ar quente

Calculado com: **EnergyPlus + AirflowNetwork** · temperaturas e vazões da rede de fluxo de ar · detalhes e confiabilidade na seção 10

Não existe um coeficiente padrão único para isso; por isso o relatório usa três indicadores mensuráveis: (1) as **trocas de ar por hora nas horas quentes**; (2) a **efetividade de exaustão η** = (T fechada − T ventilada) ÷ (T fechada − T externa), calculada com as temperaturas operativas de cada ambiente nas horas ocupadas em que a casa de janelas fechadas passa de 26 °C e está mais de 1 °C acima do ar externo (0 = a ventilação não resfria o ambiente, 1 = o ambiente acompanha o ar externo); (3) o **calor retirado** pelo ar que sai da casa, ρ·cp·V·(T zona − T externa), em kWh por ano. A idade do ar e a retirada de uma pluma de ar quente junto ao forro exigem um CFD interno, que este estudo não faz.

Fonte do procedimento: seção 11,4 da ABNT NBR 15575-1:2021 (texto integral, cópia guardada em norms/source_docs) e o projeto público de emenda de março de 2021 (LabEEE); as tabelas 3, 4, 20 e 21 conferem nos dois, e a equação da figura 4 (ΔPHFTmín = 45 − 0,58 × PHFT da referência, unifamiliar) foi lida da figura do projeto. Zona bioclimática: um artigo não oficial (UGREEN, outubro de 2026, guardado em norms/source_docs) diz que Maringá passou da zona 1 para a zona 4B na NBR 15220-3:2024, que está entre as zonas em que vale o critério de temperatura mínima; a norma de 2024 em si não foi conferida. Suposições nossas: a cozinha e o corredor são ambientes de permanência transitória (não entram no PHFT); as portas internas entre dormitório ou sala e ambiente transitório ficam abertas; a faixa de 18-26 °C e os pontos de ajuste de 23/21 °C valem porque a temperatura média anual está abaixo de 25 °C;os coeficientes de pressão do vento vêm do CFD (a fórmula genérica de Swami & Chandra fica só como comparação); os muros do lote e as edificações vizinhas estão no CFD com alturas estimadas, mas não nos modelos de sombra e de luz natural; a temperatura do solo é a média anual do arquivo climático.

7. Melhorias: isolamento, vedação, vidro e sombreamento

Cada melhoria abaixo é simulada no ano inteiro e comparada com a casa como ela é hoje. A **lã no telhado** fica sobre o forro (lado do sótão); a **vedação** são borrachas e escovas nas esquadrias e portas; o **vidro duplo** substitui o vidro simples; o **brise fixo** é uma projeção horizontal sobre cada janela; as **persianas móveis** fecham sozinhas no modelo quando o sol na janela é forte. A última linha combina as principais medidas.


7,1 Resultados por melhoria

Melhoria	O que é	Horas confortáveis	Horas quente demais	Hora mais quente	Resfriamento R$/ano	Variação na conta	Luz natural
Situação atual	Casa existente	82,0% Bom 4/5	788 h	32,9 °C	R$ 1.657	R$ 0/ano	100%
Lã de rocha 50 mm	Lã de rocha 50 mm	86,8% Bom 4/5	521 h	31,4 °C	R$ 1.094	R$ -563/ano	100%
Lã de vidro 50 mm	Lã de vidro 50 mm	86,9% Bom 4/5	515 h	31,3 °C	R$ 1.079	R$ -578/ano	100%
Lã de PET 50 mm	Lã de PET (garrafas recicladas) 50 mm	86,9% Bom 4/5	516 h	31,3 °C	R$ 1.079	R$ -578/ano	100%
Lã de ovelha 50 mm	Lã de ovelha 50 mm	86,9% Bom 4/5	516 h	31,3 °C	R$ 1.079	R$ -578/ano	100%
Lã de rocha 100 mm	Lã de rocha 100 mm	87,5% Bom 4/5	491 h	31,1 °C	R$ 996	R$ -661/ano	100%
Vedação das esquadrias	Borrachas e escovas de vedação nas esquadrias e portas	82,2% Bom 4/5	785 h	32,8 °C	R$ 1.651	R$ -6/ano	100%
Vidro duplo	Vidro duplo incolor	82,5% Bom 4/5	783 h	32,7 °C	R$ 1.621	R$ -36/ano	89%
Vidro duplo low-E	Vidro duplo low-E	83,6% Bom 4/5	656 h	32,4 °C	R$ 1.442	R$ -215/ano	80%
Brise fixo 0,6 m	Brise horizontal fixo 0,6 m	82,5% Bom 4/5	729 h	32,8 °C	R$ 1.617	R$ -40/ano	100%
Persianas móveis	Persianas / venezianas móveis (fechadas com sol forte)	82,6% Bom 4/5	711 h	32,7 °C	R$ 1.589	R$ -68/ano	100%
Tudo junto	Lã de rocha 50 mm; Borrachas e escovas de vedação nas esquadrias e portas; Vidro duplo low-E; Brise horizontal fixo 0,6 m; Persianas / venezianas móveis (fechadas com sol forte)	88,5% Bom 4/5	393 h	30,7 °C	R$ 823	R$ -834/ano	80%

Calculado com: **Motor rápido (Python, deste projeto)** · conferência com o EnergyPlus em 7,4 · detalhes e confiabilidade na seção 10

De onde vêm os números da tabela acima:

Coluna	Como é calculada	Motor	Quanto confiar
Horas confortáveis	Parcela das 8,760 horas do ano em que a temperatura operativa do ambiente (média entre a do ar e a das superfícies) está dentro da faixa de 80% de aceitabilidade do modelo adaptativo da ASHRAE 55; média dos ambientes. O ar-condicionado funciona no seu horário neste cálculo, por isso o percentual é maior que o PHFT da seção 6,4 (casa sem ar-condicionado).	Motor rápido. Conferido com o EnergyPlus em 7,4.	Média: boa para ordenar as melhorias, o percentual absoluto é aproximado.
Horas quente demais	Horas do ano com a temperatura operativa acima do limite superior da mesma faixa; média por ambiente.	Motor rápido.	Média, igual à anterior.
Hora mais quente	Maior temperatura operativa do ano em cada ambiente, em média dos ambientes. Vem de uma hora do ano climático típico; ondas de calor reais serão mais quentes.	Motor rápido.	Média-baixa: uma única hora extrema é sensível ao arquivo climático.
Resfriamento R$/ano	Calor retirado por um ar-condicionado que mantém 26 °C nas horas de uso de cada tipo de ambiente, dividido pela eficiência (COP 3,0) e multiplicado pela tarifa (R$ 1,00/kWh, suposição definida no arquivo do projeto).	Motor rápido (energia); tarifa e COP são suposições.	Baixa: use como ordem de grandeza e para comparar melhorias. O EnergyPlus dá cerca de metade desta energia (7,4).
Variação na conta	Custo de resfriamento (e de aquecimento, quando ativado) da melhoria menos o custo da casa como está. Negativo = economia.	Motor rápido.	Baixa-média: a diferença entre melhorias é mais confiável que o valor absoluto.
Luz natural	Transmitância visível do vidro novo dividida pela do vidro existente. Conta só o vidro: persianas e sombreamento não entram aqui e nenhum motor de luz é rodado para esta coluna.	Valor de catálogo (sem motor); a luz natural da própria casa está nas seções de luz natural (Radiance).	Média: valor de catálogo, não um cálculo.

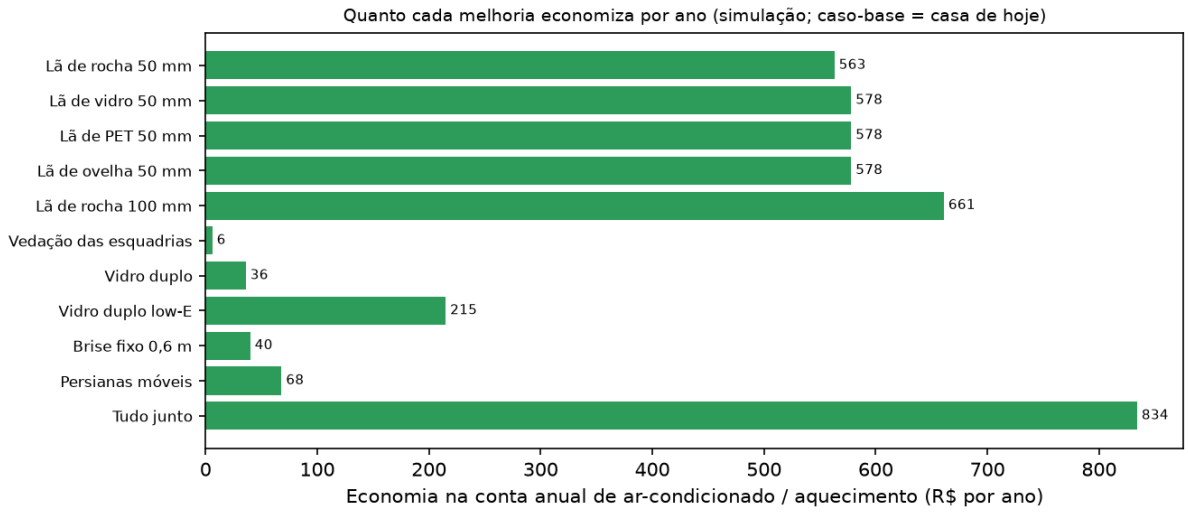

7,2 Qual lã e que espessura? (variação na conta anual e média de horas confortáveis)

Lã	25 mm	50 mm	75 mm	100 mm	150 mm
Lã de vidro λ 0,040 W/m·K	R$ -453 86,1%	R$ -578 86,9%	R$ -637 87,3%	R$ -670 87,5%	R$ -709 87,8%
Lã de rocha λ 0,044 W/m·K	R$ -434 85,9%	R$ -563 86,8%	R$ -625 87,2%	R$ -661 87,5%	R$ -702 87,6%
Lã de PET (garrafas recicladas) λ 0,040 W/m·K	R$ -453 86,0%	R$ -578 86,9%	R$ -637 87,3%	R$ -672 87,5%	R$ -710 87,7%
Lã de ovelha λ 0,040 W/m·K	R$ -453 86,0%	R$ -578 86,9%	R$ -638 87,3%	R$ -672 87,5%	R$ -710 87,6%

Calculado com: **Motor rápido (Python, deste projeto)** · detalhes e confiabilidade na seção 10

Negativo = economia por ano. Mais lã sempre ajuda, com retorno decrescente: os primeiros 50 mm dão a maior parte do benefício. As lãs diferem pouco na condutividade; a escolha costuma depender de preço, comportamento ao fogo, manuseio e umidade.

7,3 Valores usados e quão confiáveis são

Medida	Valor usado	Confiança no valor	Fonte
Lã de vidro	λ 0,040 W/m·K, ρ 15 kg/m³	típico	range 0,030-0,046 W/mK (Saint-Gobain, wool insulation comparison); mid-range value
Lã de rocha	λ 0,044 W/m·K, ρ 40 kg/m³	verificado	Rockwool datasheet (panel, 0,044 W/mK at 50 C, EN 12667)
Lã de PET (garrafas recicladas)	λ 0,040 W/m·K, ρ 30 kg/m³	suposição	typical manufacturer range 0,037-0,041 W/mK; check the product you buy
Lã de ovelha	λ 0,040 W/m·K, ρ 25 kg/m³	suposição	typical range 0,038-0,042 W/mK; check the product you buy
Vidro simples (existente)	U 5,8 W/m²K, g 0,85, VT 0,88	verificado	5,8 W/m2K is the single-glass limit of EN 673 / ISO 10077
Vidro duplo incolor	U 2,8 W/m²K, g 0,76, VT 0,78	típico	typical catalogue values for 4-12-4 clear double glazing (EN 673 / NFRC ranges)
Vidro duplo low-E	U 1,8 W/m²K, g 0,40, VT 0,70	típico	typical catalogue values for low-E (solar control) double glazing
Borrachas e escovas de vedação nas esquadrias e portas	trocas de ar com a casa fechada −25%	suposição	AIVC: weatherstripping alone cuts house air change 10-14,7%, a full retrofit up to 27,5%; 25% used for frames and doors
Brise horizontal fixo	profundidade definida por pacote	suposição	analytic profile-angle shading of the window (sun-path geometry, pvlib); depth in metres from project.json
Persianas / venezianas móveis (fechadas com sol forte)	ganho fechado x0,3	suposição	external blinds let through about 10-30% of solar gain when closed; closed when direct sun on the window exceeds 250 W/m2 (08-18 h)

Calculado com: **Modelo 3D (IFC) e tabelas** · valores de catálogo, não calculados · detalhes e confiabilidade na seção 10

Os preços das melhorias não estão incluídos: com um orçamento, divida-o pela economia anual para obter o tempo de retorno. Coluna de luz natural: parcela da luz natural que ainda entra (só a transmitância do vidro; persianas e brise não são aplicados à luz natural).

7,4 Conferência com um motor de referência (EnergyPlus)

Calculado com: **EnergyPlus + AirflowNetwork** · detalhes e confiabilidade na seção 10

Todos os pacotes acima foram recalculados com o **EnergyPlus** (Departamento de Energia dos EUA), motor de código aberto validado pela norma ASHRAE 140 e usado dentro do DesignBuilder e do OpenStudio. Ele resolve o balanço de calor de cada superfície com funções de transferência de condução, compartilha as paredes entre os ambientes, modela o forro ventilado acima de cada ambiente, sombreia as janelas com os beirais reais e usa ventilação por vento e empuxo térmico (janelas 50% abertas quando o ar externo está mais frio e acima de 18 °C). O ar-condicionado mantém o mesmo ponto de ajuste, horários e COP do motor rápido. Nenhum dos dois motores considera ganhos internos (pessoas, lâmpadas, aparelhos).

Pacote	Conforto % sem ar-cond. (EnergyPlus)	Ar-cond. kWh/ano rápido	Ar-cond. kWh/ano EnergyPlus	Economia/ano EnergyPlus
Situação atual	77,7	1.657	671	-
Lã de rocha 50 mm	83,1	1.094	286	R$ 385
Lã de vidro 50 mm	83,1	1.079	278	R$ 393
Lã de PET 50 mm	83,1	1.079	278	R$ 393
Lã de ovelha 50 mm	83,1	1.079	278	R$ 393
Lã de rocha 100 mm	83,4	996	235	R$ 436
Vedação das esquadrias	78,0	1.651	669	R$ 2
Vidro duplo	78,5	1.621	651	R$ 20
Vidro duplo low-E	78,5	1.442	588	R$ 83
Brise fixo 0,6 m	77,5	1.617	654	R$ 17
Persianas móveis	77,3	1.589	627	R$ 44
Tudo junto	81,7	823	182	R$ 489

Resultado com o EnergyPlus: caso base: 77,7% das horas na zona de conforto (motor rápido 77,3%), 594 horas de calor (rápido 1211), 1356 horas de frio (rápido 775); ar-condicionado 671 kWh/ano (rápido 1.657). Os dois motores concordam na ordem: **isolar a cobertura é de longe a melhor medida**; vidro e sombreamento mudam pouco.

Diferenças entre os motores são esperadas: o EnergyPlus dá cerca de metade da energia de ar-condicionado do motor rápido e mais horas de frio (ele acopla o piso ao solo e perde calor pelo forro com mais liberdade). Para decisões, prefira os números do EnergyPlus; o motor rápido continua útil para simulações rápidas de hipóteses. Ainda não modelados: ganhos internos, abertura de portas, a inclinação do telhado (usa-se um telhado plano com o mesmo volume de forro) e a sombra dos vizinhos.

8. Classificação de luz natural para construção sustentável (LEED / IES LM-83)

Calculado com: **Motor rápido (Python, deste projeto)** · conferência com o Radiance em 8,1 · detalhes e confiabilidade na seção 10

O LEED é a certificação de construção sustentável mais usada no mundo. O crédito de luz natural (v4,1, Opção 1) é dado a partir do **sDA300/50%** simulado (parcela do piso de permanência que recebe 300 lux em pelo menos metade das horas de uso) e do **ASE1000,250** (parcela do piso com mais de 1,000 lux de sol direto por mais de 250 horas por ano, risco de ofuscamento e superaquecimento), ambos definidos na norma IES LM-83 (edição atual LM-83-23, fevereiro de 2023). Degraus: sDA médio de pelo menos 40% = 1 ponto, 55% = 2 pontos, 75% = 3 pontos; um ASE acima de 10% precisa ser justificado com uma estratégia contra ofuscamento.

Ambiente	Área m²	sDA300/50%	ASE1000,250	Degrau LEED isolado
Quarto 1	15,6	100% 3 pontos 5/5	33% Muito alta 1/5	3 ponto(s)
Sala de estar	13,2	78% 3 pontos 5/5	0% Muito baixa 5/5	3 ponto(s)
Sala de TV	15,8	100% 3 pontos 5/5	7% Aceitável 4/5	3 ponto(s)
Quarto 2	10,5	100% 3 pontos 5/5	21% Muito alta 1/5	3 ponto(s)
Quarto 3	11,6	100% 3 pontos 5/5	19% Alta 2/5	3 ponto(s)
Cozinha	12,5	100% 3 pontos 5/5	0% Muito baixa 5/5	3 ponto(s)
Casa inteira (ponderada pela área)	79,2	96% 3 pontos 5/5	14% Alta 2/5	3 ponto(s)

Resultado: sDA300/50% ponderado pela área = 96,3% e ASE1000,250 = 13,5%: **3 de 3 ponto(s) de luz natural** (ASE acima de 10%: é preciso uma estratégia contra ofuscamento). Ambientes abaixo de 40%: nenhum.

Isto é uma pré-avaliação indicativa: o LEED exige avaliador certificado, modelagem de mobiliário e persianas, grade de 0,6 m e o procedimento completo da LM-83 (nossa grade é de 0,5 m, com 8h-18h como horas de uso e persianas abertas). O LEED v4,1 cita formalmente a edição de 2012 da LM-83; a edição de 2023 mantém as mesmas duas métricas (não conseguimos verificar as mudanças detalhadas). Residências costumam ser certificadas pelo LEED for Homes, cujas regras de luz natural são diferentes.

Luz natural LEED (sDA300/50%, média ponderada pela área dos ambientes de permanência) Padrão internacional

Autonomia espacial de luz natural média de salas, dormitórios e cozinhas (ponderada pela área do piso): parcela do piso que recebe 300 lux em pelo menos metade das horas de uso. O LEED v4,1 dá 1 ponto a partir de 40%, 2 pontos a partir de 55% e 3 pontos a partir de 75%. Apenas pré-avaliação indicativa: um crédito LEED de verdade exige avaliador certificado e o método completo da LM-83.

Sem pontos 2/5	abaixo de 40 % do piso	Abaixo dos 40% necessários para o primeiro ponto.
1 ponto 3/5	40 a 55 % do piso	Atende ao primeiro degrau de luz natural do LEED.
2 pontos 4/5	55 a 75 % do piso	Atende ao segundo degrau de luz natural do LEED.
3 pontos 5/5	75 ou mais % do piso	Atende ao degrau máximo de luz natural do LEED.

Esta casa: Casa inteira 96% 3 pontos 5/5

Fonte: USGBC LEED v4,1, crédito de Luz natural, Opção 1 (simulação): média de sDA300/50% de 40% / 55% / 75% = 1 / 2 / 3 pontos; ASE1000,250 acima de 10% exige estratégia contra ofuscamento (limites lidos na página do crédito v4,1 no LEEDuser); ANSI/IES LM-83-23 (publicada em fev/2023): autonomia espacial de luz natural (sDA) e exposição solar anual (ASE); o LEED v4,1 ainda cita a edição de 2012, com as mesmas duas métricas. Também é exigido ASE1000,250 de no máximo 10% (senão é preciso explicar a estratégia contra ofuscamento). Banheiros, corredores e áreas externas não são de "permanência".

8,1 Conferência com um motor de referência (Radiance)

Calculado com: **Radiance** · detalhes e confiabilidade na seção 10

Os números acima vêm do nosso motor rápido (sol por traçado de raios + estimativa de fluxo dividido com céu uniforme). Para testá-los, os mesmos ambientes e pontos de medição foram recalculados com o **Radiance** (Lawrence Berkeley National Laboratory, motor de código aberto validado pela CIE 171 e usado pelo ClimateStudio e pelo Honeybee: céu de Perez do mesmo arquivo climático, 4 reflexões de luz, método anual de coeficientes de luz natural e a regra da LM-83 que fecha as persianas quando o sol direto atinge mais de 2% do ambiente (transmitância da persiana 5%). Um sensor acima do telhado reproduz a iluminância do arquivo climático com diferença de 2%, então o céu está calibrado.

Ambiente	Área m²	sDA300/50% rápido	sDA300/50% Radiance	ASE Radiance	Lux médio rápido → Radiance
Quarto 1	15,6	100%	51% 1 ponto 3/5	47%	3.222 → 2.239
Sala de estar	13,2	78%	0% Sem pontos 2/5	0%	323 → 170
Sala de TV	15,8	100%	20% Sem pontos 2/5	16%	1.062 → 737
Quarto 2	10,5	100%	24% Sem pontos 2/5	48%	1.880 → 1.407
Quarto 3	11,6	100%	28% Sem pontos 2/5	38%	1.689 → 1.242
Cozinha	12,5	100%	0% Sem pontos 2/5	0%	316 → 108

Resultado com o Radiance: sDA300/50% ponderado pela área = 21,3% (motor rápido: 96,3%), ASE1000,250 = 24,4%: **0 de 3 ponto(s) de luz natural**. O motor rápido é otimista no fundo dos ambientes; prefira os números do Radiance para decisões.

Ainda não modelados na rodada do Radiance: mobiliário, caixilhos e montantes (usa-se transmitância 0,80 para toda a abertura), a treliça da porta de vidro, os prédios vizinhos e a sombra de árvores. As persianas seguem a regra simplificada da LM-83 por ambiente. Janelas e brise como no caso base.

9. Biofilia: vistas e planta

Calculado com: **Análise de biofilia (traçado de raios e isovista em planta, deste projeto)** + **Modelo 3D (IFC) e tabelas** · raios lançados de dentro de cada ambiente pelas janelas; os motores das seções 2 a 8 fornecem luz natural e ventilação · detalhes e confiabilidade na seção 10

Biofilia é a necessidade humana de estar ligado à natureza. Esta seção mede quanto dela a casa entrega, com duas referências publicadas: a **Matriz de Design Biofílico** de 14 padrões (Terrapin Bright Green; a régua de sete colunas vem do vídeo da UGREEN) e o **Índice de Cura Biofílico** de Salingaros (dez componentes, de 0 a 20). Ela olha as vistas e as superfícies, não só a planta, porque as pessoas não percebem uma planta. Cada padrão diz qual motor o produziu e quanto confiar; o que nenhum motor mede (água, sons e cheiros, materiais, complexidade) fica *não avaliado* até o proprietário declarar.

Apenas indicativo: Apenas indicativo: a matriz e o Índice de Cura Biofílico não têm validação clínica; o autor do índice chama a ligação com a cura de conjectura. Plantas em vasos dentro de casa não purificam o ar em ambientes reais.

9,1 Matriz de Design Biofílico: 14 padrões



Um padrão é colocado numa coluna pela parcela dos ambientes contados (ambientes ocupados, exceto banheiros, corredor e áreas externas) que cumprem um critério forte: nenhum = não incluído, só uma forma fraca = só em detalhe, até a metade = em poucas áreas, mais da metade = casa. As duas colunas além de *casa* exigem outros edifícios e não são usadas. Esses limiares são desta ferramenta, não uma regra publicada, e a matriz não tem nota total oficial, então nenhuma é inventada. Padrões apoiados em indicador fraco ficam limitados a *em poucas áreas*.

Padrão	Coluna	Como	Confiança	Evidência
A1 Conexão visual com a natureza	**Só em detalhe**	calculado traçado de raios (biophilia_views.py)	média	0 de 6 ambientes contados veem céu, vegetação (camada intermediária) e chão por uma janela, ou ao menos 15% de verde: -. Uma vista de muros, rua ou casas vizinhas não conta como natureza. As árvores vêm do IFC (caixas em posições estimadas).
A2 Conexão não visual com a natureza	**Não avaliado**	não avaliado -	—	Não avaliado: nenhum motor mede sons de água e fauna, plantas aromáticas, texturas de madeira e pedra reais. Declare em project.json (biophilia.matrix.A2).
A3 Estímulos sensoriais não rítmicos	**Só em detalhe**	inferido (indicador indireto) traçado de raios (biophilia_views.py)	baixa	Só um indicador indireto: folhas e sombras em movimento precisam de vegetação à vista; som, cheiro e tato não são avaliados. Há verde visível de alguma janela.
A4 Variabilidade térmica e do fluxo de ar	**Em poucas áreas**	inferido (indicador indireto) motor rápido (horas de ventilação cruzada) + estudo de ventilação do EnergyPlus	baixa	Indicador indireto: 5 de 6 ambientes contados têm boa movimentação de ar: Quarto 1, Sala de estar, Quarto 2, Quarto 3, Cozinha. O padrão pede variabilidade do ar e da temperatura, que não é medida: isto só mostra quanto ar circula. Ambientes com resultado do EnergyPlus usam 5 ou mais trocas de ar por hora nas horas quentes como critério (casa: 9,8, efetividade de exaustão 0,41); os demais usam as horas de ventilação cruzada do motor rápido.
A5 Presença de água	**Não avaliado**	não avaliado -	—	Não avaliado: nenhum motor mede água vista e ouvida (espelho d'água, piscina, fonte). Declare em project.json (biophilia.matrix.A5).
A6 Luz dinâmica e difusa	**Só em detalhe**	calculado orientação das janelas (IFC) + luz natural do Radiance	média	0 de 6 ambientes contados têm janelas voltadas para ao menos duas direções: -; 6 chegam a 100 lux ou mais em média (8-18 h, Radiance). O sDA sozinho não é usado: mede luz para trabalho, não variação.
A7 Conexão com sistemas naturais	**Só em detalhe**	inferido (indicador indireto) traçado de raios + árvores do IFC	baixa	Só um indicador indireto: vegetação que acompanha as estações vista dos ambientes; a trajetória do sol e o clima ainda não estão ligados às vistas.
B1 Formas e padrões biomórficos	**Não incluído**	inferido (indicador indireto) geometria do IFC	baixa	0 de 158 elementos de construção do IFC têm geometria curva. O modelo é feito de caixas, então isso pode refletir só a modelagem, não a casa real.
B2 Conexão material com a natureza	**Não avaliado**	não avaliado -	—	Não avaliado: nenhum motor mede materiais naturais à vista (madeira, pedra, barro) em vez de laminados sintéticos; o modelo só tem as construções de parede e cobertura do project.json, não os acabamentos. Declare em project.json (biophilia.matrix.B2).
B3 Complexidade e ordem	**Não avaliado**	não avaliado -	—	Não avaliado: nenhum motor mede complexidade organizada: detalhe rico porém coerente. Declare em project.json (biophilia.matrix.B3).
C1 Refúgio	**Em poucas áreas**	calculado isovista em planta (biophilia_views.py)	baixa	6 de 6 ambientes contados têm um ponto com ao menos 60% das direções bloqueadas em 2 m (costas protegidas) e uma linha de visão de 6 m ou mais. O critério é generoso em ambientes pequenos.
C2 Perspectiva (vista de longo alcance)	**Em poucas áreas**	calculado traçado de raios + isovista em planta (biophilia_views.py)	média	3 de 6 ambientes contados têm uma janela cujo obstáculo mais próximo está a 6 m ou mais (ou vista aberta): Quarto 1, Sala de estar, Cozinha. Obstáculo mais próximo: distância mediana na faixa horizontal da abertura.
C3 Mistério	**Em poucas áreas**	inferido (indicador indireto) isovista em planta (biophilia_views.py)	baixa	Indicador indireto: 3 de 6 ambientes contados mostram dois ou mais grupos separados de vistas longas do melhor ponto (vistas reveladas aos poucos). Paredes curvas e brises não são detectados.
C4 Risco/perigo	**Não avaliado**	não avaliado -	—	Não avaliado: nenhum motor mede risco controlado: balanços, terraços, bordas altas. Declare em project.json (biophilia.matrix.C4).

Padrões por coluna: Não incluído 1, Só em detalhe 4, Em poucas áreas 4, Casa 0; não avaliados 5.

9,2 Índice de Cura Biofílico (Salingaros)

Calculado com: **Análise de biofilia (traçado de raios e isovista em planta, deste projeto)** · luz do sol, vida e curvas pelo modelo; o resto pelo proprietário · detalhes e confiabilidade na seção 10

O índice soma dez componentes, cada um avaliado em 0 (nenhum), 1 (algum) ou 2 (muito), num total de 0 a 20 com pesos iguais. O autor chama a ligação entre o índice e a cura de **conjectura ainda a testar**; trate-o como um número aproximado e comparativo. Aqui só 3 dos 10 componentes podem ser estimados pelo modelo, então o número abaixo é parcial, não uma nota de 20.

Componente	0 / 1 / 2	Como	Evidência
Luz do sol (de várias direções)	**1**	inferido (indicador indireto) horas de sol direto do motor rápido + orientação das janelas (IFC)	4 de 6 ambientes contados recebem sol direto nas janelas (0,05 h/dia ou mais, média do ano), 2 recebem 0,5 h/dia ou mais; os ambientes com sol se voltam para 3 dos 4 quadrantes da bússola. O índice pede sol vindo de várias direções.
Vida	**1**	inferido (indicador indireto) árvores do IFC + traçado de raios	7 elementos de árvore no IFC; 0% dos ambientes contados veem 15% ou mais de verde. Animais e pessoas não são contados.
Curvas	**0**	inferido (indicador indireto) geometria do IFC	Elementos curvos do IFC (o modelo é de caixas: pode ser só a modelagem).
Cor	**—**	não avaliado -	Não avaliado: falta a estimativa do observador (0, 1 ou 2); declare em project.json (biophilia.bhi).
Gravidade	**—**	não avaliado -	Não avaliado: falta a estimativa do observador (0, 1 ou 2); declare em project.json (biophilia.bhi).
Fractais	**—**	não avaliado -	Não avaliado: falta a estimativa do observador (0, 1 ou 2); declare em project.json (biophilia.bhi).
Detalhe	**—**	não avaliado -	Não avaliado: falta a estimativa do observador (0, 1 ou 2); declare em project.json (biophilia.bhi).
Água	**—**	não avaliado -	Não avaliado: falta a estimativa do observador (0, 1 ou 2); declare em project.json (biophilia.bhi).
Representações da natureza	**—**	não avaliado -	Não avaliado: falta a estimativa do observador (0, 1 ou 2); declare em project.json (biophilia.bhi).
Complexidade organizada	**—**	não avaliado -	Não avaliado: falta a estimativa do observador (0, 1 ou 2); declare em project.json (biophilia.bhi).

> **Resultado:** 2 de 6 possíveis nos 3 componentes que o modelo consegue estimar; com as avaliações do proprietário 2 de 6 em 3 de 10 componentes (o índice completo exige os dez).

9,3 Vista para fora de cada ambiente

Calculado com: **Análise de biofilia (traçado de raios e isovista em planta, deste projeto)** · traçado de raios por cada janela; árvores do IFC em posições estimadas · detalhes e confiabilidade na seção 10


Cada imagem é vista de dentro do ambiente, por uma janela, sentado (1,2 m) e em pé (1,6 m). Cores: céu azul, vegetação verde, chão vermelho, paredes, telhados e vizinhos cinza. Uma vista restauradora tem céu, uma camada intermediária de vegetação e chão (cada um com ao menos 5% da janela), com o obstáculo mais próximo a 6 m ou mais (regra do

vídeo da UGREEN, aplicada aqui como critério desta ferramenta; um muro, a rua ou as casas vizinhas não contam como natureza). As distâncias são medidas a partir do olho, 1 m atrás da janela, então 6 m são 5 m a partir do vidro. O vidro é tratado como totalmente transparente, as árvores são caixas em posições estimadas e a tabela usa o olho em pé.


Ambiente	Janelas	Verde à vista (melhor janela)	Céu + intermediário + chão	Obstáculo mais próximo a 6 m ou mais	Linha de visão mais longa (planta)
Quarto 1	1	0%	não	sim	60 m
Banheiro 1 (serviço)	1	0%	não	não	5 m
Sala de estar	1	0%	não	sim	33 m
Sala de TV	1	0%	não	não	31 m
Quarto 2	1	0%	não	não	10 m
Banheiro 2 (serviço)	1	0%	não	não	4 m
Quarto 3	1	0%	não	não	15 m
Cozinha	1	4%	não	sim	23 m
Banheiro externo (serviço)	1	0%	não	não	12 m
Depósito externo (serviço)	1	17%	sim	sim	19 m

Vista a partir de Quarto 1

Janela 0 — sentado (1,2 m)
verde 0% · obstáculo mais próximo: 20.1 m · 3 camadas: não

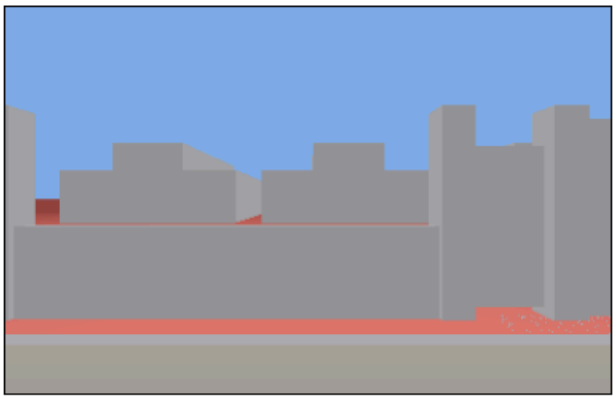


Janela 0 — em pé (1,6 m)
verde 0% · obstáculo mais próximo: 20.2 m · 3 camadas: não

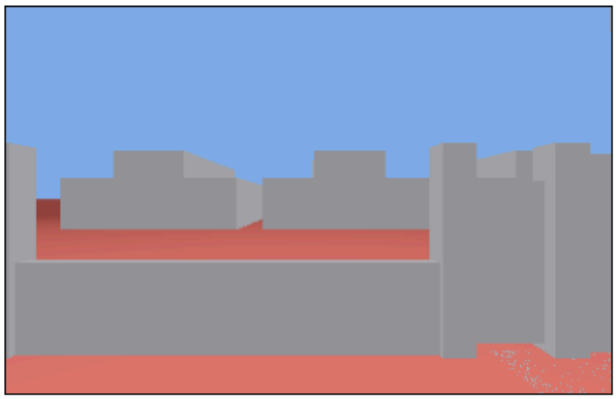


céu vegetação chão construído (paredes, telhados, vizinhos)

Vista a partir de Banheiro 1

Janela 4 — sentado (1,2 m)
verde 0% · obstáculo mais próximo: — · 3 camadas: não

 


Janela 4 — em pé (1,6 m)
verde 0% · obstáculo mais próximo: — · 3 camadas: não

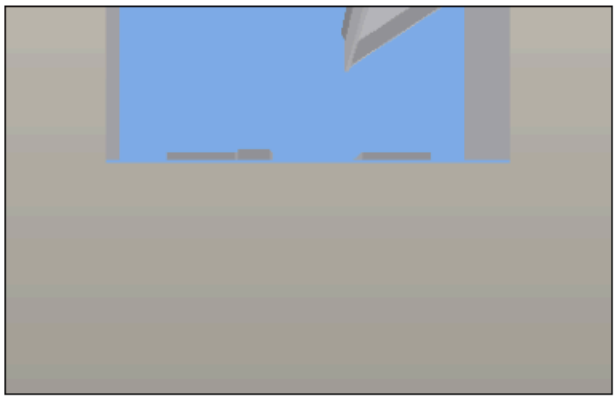


céu vegetação chão construído (paredes, telhados, vizinhos)

Vista a partir de Sala de estar

Janela 6 — sentado (1,2 m)
verde 0% · obstáculo mais próximo: 7.5 m · 3 camadas: não

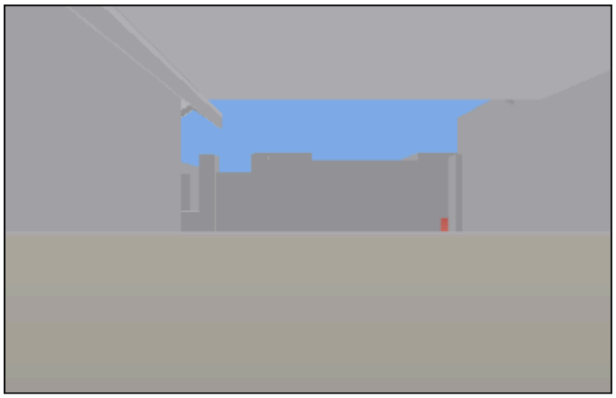

Janela 6 — em pé (1,6 m)
verde 0% · obstáculo mais próximo: 7.2 m · 3 camadas: não

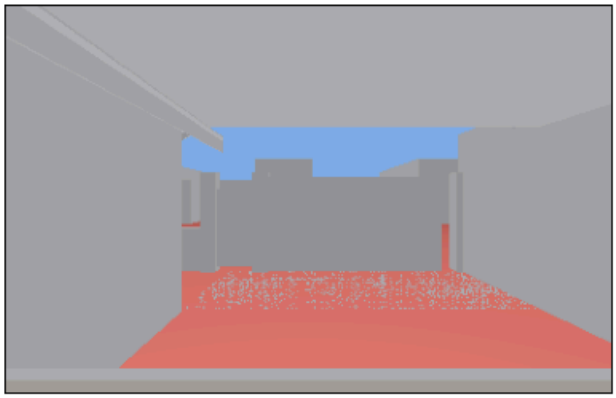


céu · vegetação · chão · construído (paredes, telhados, vizinhos)

Vista a partir de Sala de TV

Janela 7 — sentado (1,2 m)
verde 0% · obstáculo mais próximo: 3.9 m · 3 camadas: não




Janela 7 — em pé (1,6 m)
verde 0% · obstáculo mais próximo: 3.9 m · 3 camadas: não

 


céu · vegetação · chão · construído (paredes, telhados, vizinhos)

Vista a partir de Quarto 2

Janela 1 — sentado (1,2 m)
verde 0% · obstáculo mais próximo: 2.7 m · 3 camadas: não

 


Janela 1 — em pé (1,6 m)
verde 0% · obstáculo mais próximo: 2.9 m · 3 camadas: não

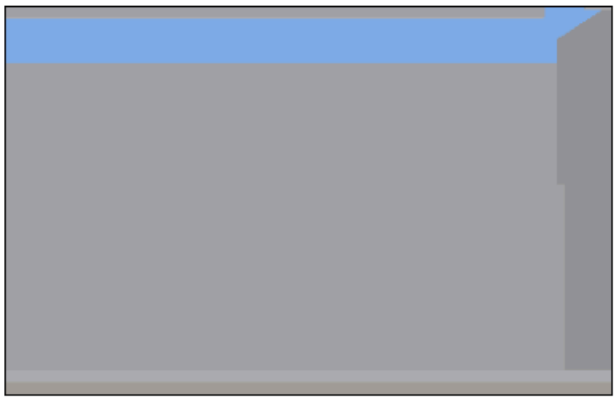


céu · vegetação · chão · construído (paredes, telhados, vizinhos)

Vista a partir de Banheiro 2

Janela 3 — sentado (1,2 m)
verde 0% · obstáculo mais próximo: — · 3 camadas: não

 


Janela 3 — em pé (1,6 m)
verde 0% · obstáculo mais próximo: — · 3 camadas: não

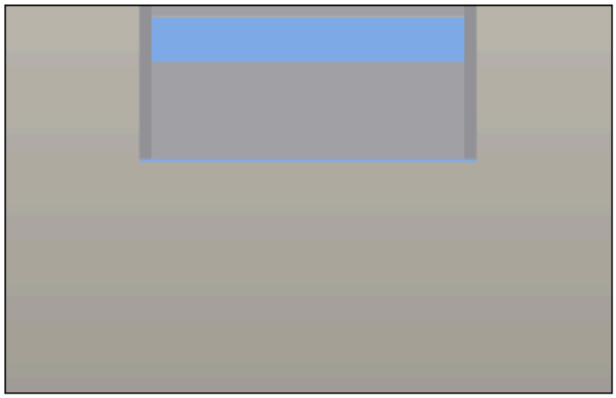


céu · vegetação · chão · construído (paredes, telhados, vizinhos)

Vista a partir de Quarto 3

Janela 2 — sentado (1,2 m)
verde 0% · obstáculo mais próximo: 2.7 m · 3 camadas: não

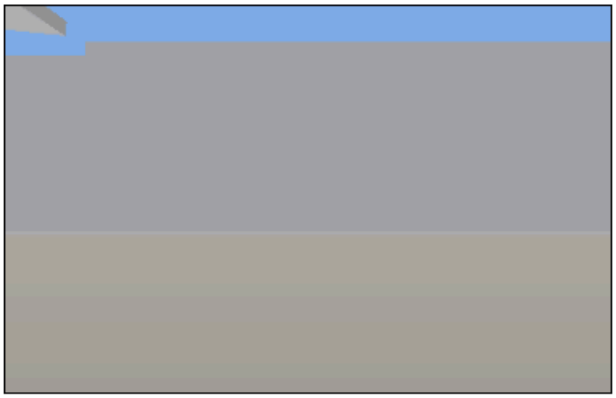


Janela 2 — em pé (1,6 m)
verde 0% · obstáculo mais próximo: 2.9 m · 3 camadas: não

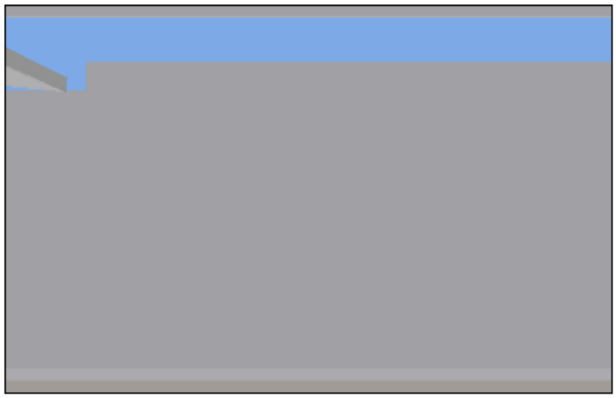


céu · vegetação · chão · construído (paredes, telhados, vizinhos)

Vista a partir de Cozinha

Janela 5 — sentado (1,2 m)
verde 8% · obstáculo mais próximo: 6.5 m · 3 camadas: não

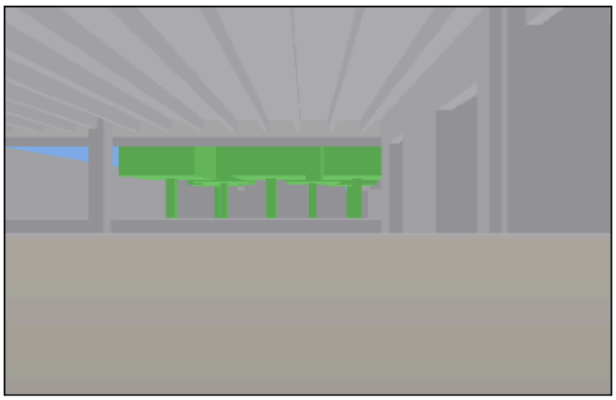


Janela 5 — em pé (1,6 m)
verde 4% · obstáculo mais próximo: 10.7 m · 3 camadas: não

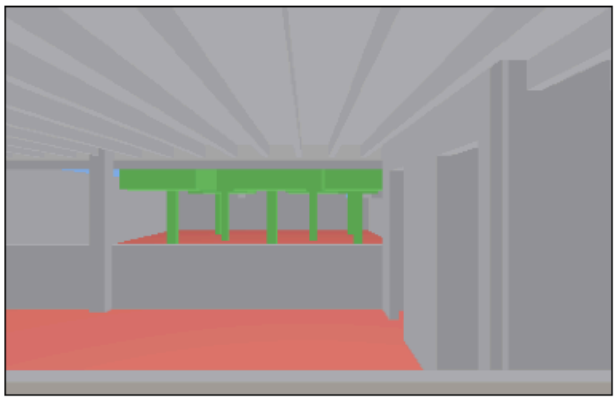


céu · vegetação · chão · construído (paredes, telhados, vizinhos)

Vista a partir de Banheiro externo

Janela 8 — sentado (1,2 m)
verde 0% · obstáculo mais próximo: — · 3 camadas: não

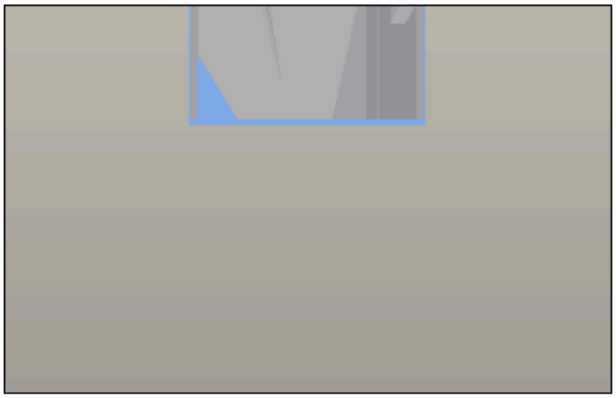


Janela 8 — em pé (1,6 m)
verde 0% · obstáculo mais próximo: 4.2 m · 3 camadas: não

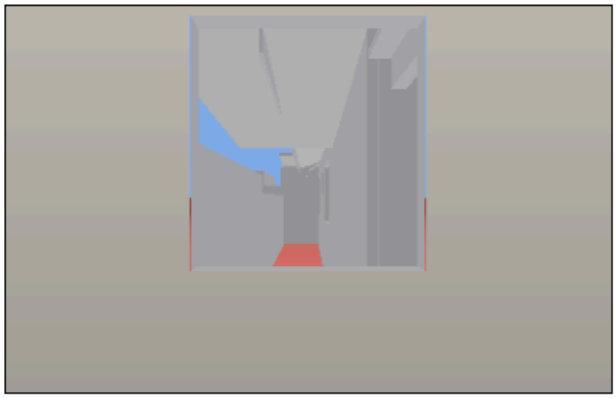


céu vegetação chão construído (paredes, telhados, vizinhos)

Vista a partir de Depósito externo

Janela 9 — sentado (1,2 m)
verde 41% · obstáculo mais próximo: 9.8 m · 3 camadas: não

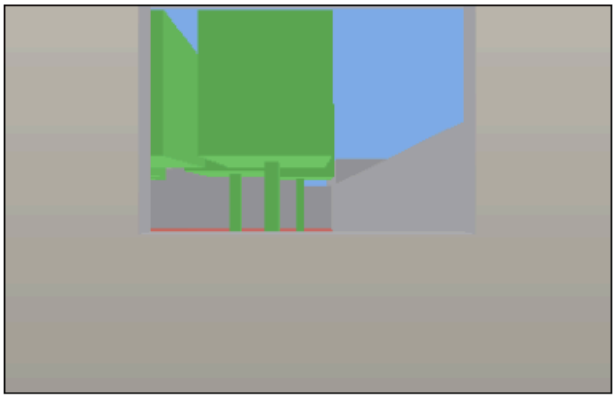

Janela 9 — em pé (1,6 m)
verde 17% · obstáculo mais próximo: 8.4 m · 3 camadas: sim

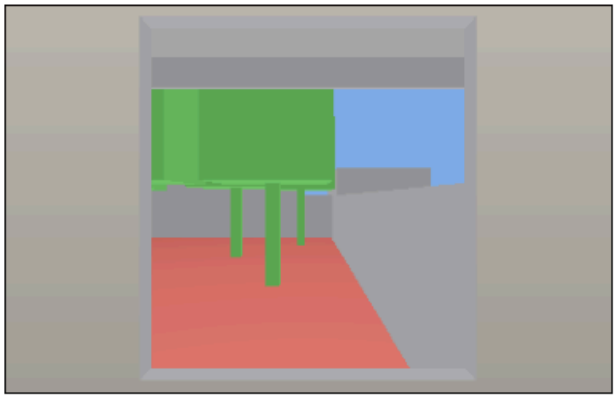

céu vegetação chão construído (paredes, telhados, vizinhos)

9,4 Umidade e mofo (triagem)

Calculado com: **EnergyPlus + AirflowNetwork + OpenFOAM (CFD)** · umidade da zona e temperaturas das superfícies internas; AirflowNetwork com as pressões do CFD · detalhes e confiabilidade na seção 10

Pouco sol direto e ventilação fraca, em clima úmido, favorecem o mofo. O EnergyPlus dá a umidade e a temperatura da parede ou do forro mais frio de cada ambiente no ano inteiro; a umidade relativa da superfície vem daí. A triagem usa o teste simplificado da ASHRAE 160: a média móvel de 30 dias da umidade relativa da superfície deve ficar abaixo de 80% enquanto a temperatura média de 30 dias está entre 5 e 40 °C. Adendos da ASHRAE trocam esse limite fixo por um modelo de índice de mofo porque ele é conservador (confira a edição vigente), e a OMS (2009) não dá um limite numérico; leia como triagem, não como diagnóstico. Rodam-se dois casos: **aberta** = a casa como é, com os moradores abrindo as janelas pela regra usual, e **fechada** = um caso-limite com as janelas fechadas o ano todo, sem ar-condicionado e com os moradores dentro, que não é como a casa é usada. Do lado de fora o ar passa de 80% em 2.058 horas do ano (média 66%).

Ambiente	Sol direto h/dia	Vent. cruzada %	Horas com ar acima de 80%	Maior UR da superfície em 30 dias, aberta / fechada	Ano acima do limite, aberta / fechada	Leitura
Quarto 1	0,64	36	672	72% / 89%	0,0% / 45,3%	só no caso-limite de casa fechada
Banheiro 1 (serviço)	0,05	0	890	74% / 74%	0,0% / 0,0%	não avaliável: sem fonte de umidade no modelo · pouco sol
Sala de estar	0,00	100	597	73% / 90%	0,0% / 90,4%	só no caso-limite de casa fechada · pouco sol
Sala de TV	0,27	77	606	73% / 92%	0,0% / 88,0%	só no caso-limite de casa fechada · pouco sol
Corredor (serviço)	0,01	76	591	72% / 80%	0,0% / 0,0%	não avaliável: sem fonte de umidade no modelo · pouco sol
Quarto 2	0,51	36	630	70% / 93%	0,0% / 100,0%	só no caso-limite de casa fechada
Banheiro 2 (serviço)	0,06	36	614	72% / 71%	0,0% / 0,0%	não avaliável: sem fonte de umidade no modelo · pouco sol
Quarto 3	0,42	36	518	68% / 97%	0,0% / 100,0%	só no caso-limite de casa fechada
Cozinha	0,01	77	686	74% / 75%	0,0% / 0,0%	não avaliável: sem fonte de umidade no modelo · pouco sol
Banheiro externo (serviço)	0,31	0	772	73% / 73%	0,0% / 0,0%	não avaliável: sem fonte de umidade no modelo
Depósito externo (serviço)	0,08	0	719	72% / 72%	0,0% / 0,0%	não avaliável: sem fonte de umidade no modelo · pouco sol

Ambientes a observar: Quarto 1, Sala de estar, Sala de TV, Quarto 2, Quarto 3

Limites: no modelo, as pessoas são a única fonte de umidade (quartos e sala); a cozinha e os banheiros não têm nenhuma (sem cozimento, sem banho), as paredes não armazenam umidade e não há chuva nem umidade ascendente. A tabela mostra então como o clima e a ventilação pressionam cada ambiente; um banheiro com vapor todos os dias ficaria pior do que o mostrado. A temperatura da superfície é a da parede ou do forro mais frio do ambiente, não a de cantos e atrás de móveis, onde as pontes térmicas pioram o quadro.

9,5 Sugestões, por esforço


Cada sugestão diz quais padrões ela pode elevar. Só as alterações de ventilação (EnergyPlus, seção 6,4) e a parede verde (medida nas vistas) trazem números; as demais são recomendações, sem ganho inventado. Cenários de árvores de sombra (sol, conforto) ainda não são simulados; as árvores entram só nas vistas, nunca nos números do caso base.

Esforço	Sugestão	Padrões	Onde / medido
Baixo esforço	Trepadeiras ou parede verde no muro que estas janelas enxergam (hoje a vista é um muro a poucos metros).	A1, A3, A7	Sala de TV: verde à vista 0% → 0% (até 14%); Quarto 2: verde à vista 0% → 0% (até 39%); Quarto 3: verde à vista 0% → 0% (até 39%) · traçado de raios (placa vegetal idealizada)
Baixo esforço	Plantar uma árvore de sombra que perde folhas no lado oeste e árvores no eixo das janelas principais: verde à vista, folhas e sombras em movimento, sombra no verão. A ser simulado como cenário (sombra e vistas).	A1, A3, A6, A7	Quarto 1, Sala de estar, Sala de TV, Quarto 2, Quarto 3
Baixo esforço	Pérgola com trepadeira sobre uma varanda ou a fachada voltada para oeste: luz filtrada que muda ao longo do dia.	A1, A3, A6	-
Baixo esforço	Uma pequena fonte de água com som (água em movimento), de preferência no lado leste, para refletir a luz da manhã para dentro.	A5, A2	-
Baixo esforço	Plantas aromáticas ao longo da circulação (capim-limão, hortelã, manjericão) como marcos sensoriais.	A2	-
Baixo esforço	Madeira ou pedra de verdade nas superfícies que as pessoas tocam (puxadores, bancos, bancadas) em vez de laminados sintéticos.	B2, A2	-
Baixo esforço	Tecidos, azulejos ou ornamentos inspirados na natureza (formas orgânicas, padrões fractais, cores da paisagem) para quebrar superfícies planas e monocromáticas.	B1, B3	-
Baixo esforço	Marcar os vidros grandes (portas de vidro) para as aves os enxergarem, e manter as luminárias voltadas para baixo.	A1	-
Baixo esforço	Não manter estes ambientes fechados por semanas: com as janelas abertas a triagem não acha risco, mas um quarto fechado o ano todo com seus ocupantes passa do limite por meses. Manter uma janela entreaberta ou instalar uma abertura / exaustor, e usar tinta antimofo nas paredes mais frias.	A4	Quarto 1, Sala de estar, Sala de TV, Quarto 2, Quarto 3
Médio esforço	Trocar as janelas de correr por janelas de abrir, com cerca de 90% da área envidraçada aberta (o caso base supõe janelas de correr que abrem cerca de metade).	A4, A6	PHFT 58,7% (hoje 56,0%), graus-hora 3.120 (3.503), η 0,47 (0,41) · EnergyPlus (estudo de ventilação)
Médio esforço	Incluir uma grelha de cerca de 0,2 m² por ambiente no forro e beirais com aberturas maiores, para o ar quente sair pelo sótão.	A4	PHFT 56,8% (hoje 56,0%), graus-hora 3.274 (3.503), η 0,45 (0,41) · EnergyPlus (estudo de ventilação)
Médio esforço	As duas juntas: janelas de abrir mais abertas e exaustão pelo forro.	A4	PHFT 59,3% (hoje 56,0%), graus-hora 2.954 (3.503), η 0,50 (0,41) · EnergyPlus (estudo de ventilação)
Médio esforço	Preferir vidro de tonalidade neutra: vidro escuro distorce as cores da paisagem. O modelo supõe vidro claro (transmitância 0,8, sem cor), então é só orientação, sem simulação.	A1	-
Alto esforço	Janela maior ou porta de vidro voltada para a melhor paisagem do lote (jardim ou árvores), com o obstáculo mais próximo a 6 m ou mais (vista restauradora: céu, vegetação e chão).	A1, C2	-
Alto esforço	Poço de luz, jardim de inverno ou jardim rebaixado ao lado de ambientes sem luz natural direta; melhor decidir antes de construir ou numa reforma.	A1, A4, A6, C1	-


Cenário de parede verde: uma placa idealizada de folhagem de 0,4 m de espessura e 4 m de largura é colocada 0,2 m à frente do obstáculo que cada janela enxerga (janelas cujo obstáculo mais próximo está a menos de 4 m e cobre 60% ou mais da abertura). A figura e o primeiro número usam uma placa de 1,8 m de altura (uma parede trepadeira da altura do muro mais baixo); o número depois de 'até' é um limite superior com uma placa de 3,4 m que cobre todo o obstáculo. É medido só nas vistas, com o mesmo traçado de raios; os números do caso base não mudam, e não é um projeto de plantio.

Parede verde diante do obstáculo (placa idealizada de 0,4 × 4 × 1,8 m)


Sala de TV · Janela 7 — hoje
verde 0%

 


Sala de TV · Janela 7 — com parede verde
verde 0%

 


Quarto 2 · Janela 1 — hoje
verde 0%

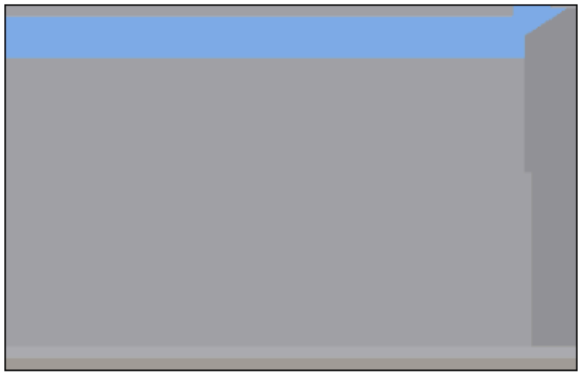


Quarto 2 · Janela 1 — com parede verde
verde 0%

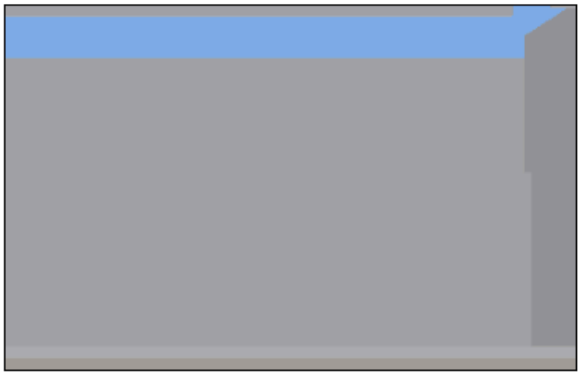

Quarto 3 · Janela 2 — hoje
verde 0%

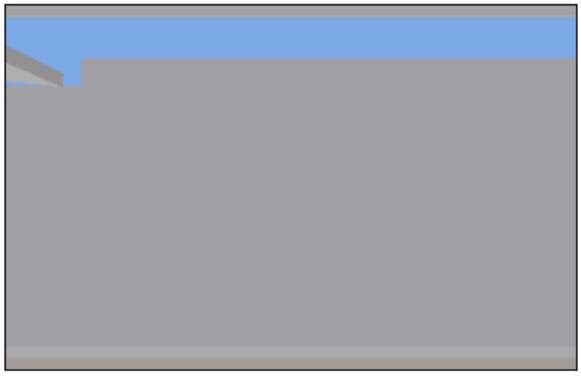

Quarto 3 · Janela 2 — com parede verde
verde 0%

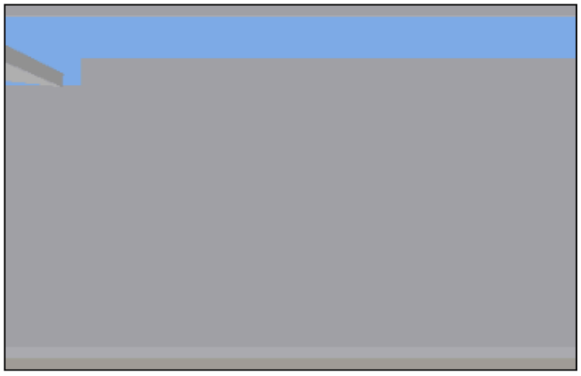

10. Como foi calculado e quanto confiar

Esta seção conta como os números foram produzidos, para você julgar quanto confiar neles. O motor rápido é código Python aberto escrito para este projeto; ele é conferido com três motores de referência de código aberto: Radiance (luz natural), EnergyPlus (calor, energia e NBR 15575) e OpenFOAM (pressão do vento). Os submodelos rápidos são padrão em física das edificações, mas simplificados. Nada aqui foi medido no edifício real.

> Situação da validação: o código é verificado por testes de regressão (o caso-base não pode mudar ao acrescentar um recurso) e por conferências da geometria solar e do balanço de energia; NÃO foi validado contra medições, e os motores de referência rodaram sobre uma versão simplificada do modelo (veja os limites de cada um). Para licença, certificação ou decisão de investimento, confirme com uma simulação feita por profissional qualificado (por exemplo EnergyPlus, Radiance).

Motores de referência

RADSITE | radiance-online.org

Radiance 6,0,2
Luz natural: sDA, ASE, LEED (LM-83)

EnergyPlus 26,2,0
Calor, energia e NBR 15575 (PHFT)

Os logos pertencem aos respectivos projetos (Radiance: LBNL; EnergyPlus: DOE dos EUA / NREL; OpenFOAM: OpenCFD / ESI Group) e aparecem apenas para creditar os programas usados.

Os motores em detalhe: parâmetros, fórmulas e referências

Motor rápido (Python, deste projeto)

Usado para: Sol e sombras, luz natural (lux, lumens, sDA, ASE), tamanho das janelas e horas de ventilação cruzada, temperatura interna, conforto, energia e custo de ar-condicionado / aquecimento, materiais e cenários de melhoria (seções 2 a 7).

Parâmetros:

- 8,760 passos horários do ano climático típico; grade de sensores de 0,5 m a 0,76 m de altura
- Luz natural: eficácia luminosa de 100 lm/W (direta) e 115 lm/W (difusa), refletância média 0,55, fator de utilização 0,45, fator de manutenção 0,8
- Térmico: resistências superficiais 0,04 (externa), 0,13 (parede), 0,17 (forro e piso) m^2K/W; coeficiente superficial externo 17 W/m^2K; absortância solar da parede 0,45; U, g e VT do vidro vindos do catálogo
- Conforto: faixa adaptativa da ASHRAE 55, aceitabilidade de 80% e 90%; temperatura externa média móvel limitada a 10-33,5 °C
- Refrigeração: ponto de ajuste e horários por tipo de ambiente (project.json), COP e tarifa como na seção 5,3; janelas fechadas com o equipamento ligado

Fórmulas:

- Lumens a instalar = lux × área ÷ (utilização 0,45 × manutenção 0,8)
- Temperatura de conforto = 0,31 × T(externa média móvel) + 17,8 °C; faixa confortável = ± 3,5 °C (80%) ou ± 2,5 °C (90%)
- Temperatura operativa = (temperatura do ar + temperatura radiante média das superfícies) ÷ 2
- Eletricidade = calor retirado ÷ COP; custo anual = eletricidade × tarifa
- Brise fixo: profundidade da sombra = beiral × tan(ângulo de perfil); persiana móvel: ganho solar × 0,3 quando o sol na janela passa de 250 W/m^2
- sDA300/50% = parcela da área do piso com pelo menos 300 lux em 50% das horas ocupadas; ASE1000,250 = parcela da área com 1,000 lux de sol direto por mais de 250 horas

Referências:

- ASHRAE Standard 55: thermal environmental conditions for human occupancy (adaptive comfort model) - https://www.ashrae.org/technical-resources/standards-and-guidelines
- ABNT NBR 15575 (Residential buildings - performance) and NBR 15220 (Thermal performance of buildings) - https://www.abntcatalogo.com.br
- EN 17037: Daylight in buildings - https://standards.cencenelec.eu
- ANSI/IES LM-83-23: sDA and ASE - https://webstore.ansi.org/standards/iesna/ansiieslm8323
- Embree ray-tracing kernels (Intel) - https://github.com/embree/embree
- IfcOpenShell: open-source IFC toolkit - https://ifcopenshell.org
- pvlib python: a Python package for modeling solar energy systems (Holmgren, Hansen, Mikofski, JOSS 2018) - https://joss.theoj.org/papers/10.21105/joss.00884
- Numba: JIT compiler for Python - https://numba.pydata.org

EnergyPlus + AirflowNetwork

Usado para: Conferência do conforto e da energia dos pacotes de melhoria (seção 7,4) e toda a simulação da NBR 15575-1:2021: PHFT, temperaturas operativas máxima e mínima, carga térmica e trocas de ar pelas aberturas (seção 6,4).

Parâmetros:

- Uma zona térmica por ambiente mais uma zona de forro ventilado; paredes compartilhadas entre ambientes; funções de transferência de condução para cada camada
- Janelas como sistemas de vidro simples; beirais reais como superfícies de sombra
- AirflowNetwork: cada janela, porta aberta e fresta é um caminho de ar; coeficientes de pressão do vento vindos do CFD do OpenFOAM (24 direções), velocidade do vento na altura da abertura pelo perfil de lei de potência (expoente 0,22)
- Rodada da NBR 15575: ocupação, iluminação e equipamentos conforme as tabelas da norma; janelas abertas só com o ambiente ocupado, o ar a pelo menos 19 °C e mais quente que o externo; janelas dos banheiros abertas
- Rodada da carga térmica: janelas fechadas, ar-condicionado ideal a 23 °C (refrigeração) e 21 °C (aquecimento) quando ocupado
- Faixa de temperatura operativa de 18-26 °C porque a temperatura média anual do arquivo climático é menor que 25 °C
- Aberturas (SimpleOpening): coeficiente de descarga 0,6, fator de abertura = fração abrível da janela (0,5 de correr), vazamento fechado 0,00063 kg/s (janelas) e 0,0024 kg/s (portas) a 1 Pa, expoente 0,63 / 0,59; aberturas de beiral do ático com 0,4% da área do piso (fresta de 0,0019 kg/s por m^2 de piso, expoente 0,65)
- Estudo de ventilação (seção 6,4): seis simulações do ano inteiro do mesmo modelo com alterações da planta (portas fechadas, grelha acima das portas, janelas de abrir com 90% de abertura, grelha de 0,2 m^2 no forro de cada ambiente com beirais 5× maiores, e as duas últimas juntas) mais uma simulação com as janelas fechadas; a vazão por cada abertura é lida hora a hora (AFN Linkage Node Volume Flow Rate)
- Setores de vento das setas de fluxo: oito setores de 45° centrados em N, NE, ... NO, com a direção do vento do arquivo climático; horas quentes = janelas abertas e temperatura operativa média dos quartos e da sala acima de 26 °C
- Triagem de umidade e mofo (seção 9,4): duas simulações do ano inteiro sem climatização (janelas abertas pelos moradores e janelas fechadas), saídas horárias da umidade relativa e da temperatura do ar de cada zona e da temperatura da face interna de suas paredes e forro opacos; a única fonte de umidade é a dos ocupantes (quartos e sala)

Fórmulas:

- PHFT = horas ocupadas com 18 °C ≤ temperatura operativa ≤ 26 °C ÷ horas ocupadas × 100

- Nível mínimo: PHFT(real) > 0,9 × PHFT(referência); T(máx,real) ≤ T(máx,ref) + 2 °C; T(mín,real) ≥ T(mín,ref) − 1 °C
- ΔPHFT = PHFT(real) − PHFT(referência); os níveis intermediário e superior exigem ΔPHFT ≥ 45 − 0,58 × PHFT(referência)
- Redução da carga = (carga da referência − carga da casa real) ÷ carga da referência
- Vazão por uma abertura (AirflowNetwork, abertura vertical grande): movida pela diferença de pressão ΔP = pressão do vento ($Cp \times \frac{1}{2}\rho U^2$) ± pressão de empuxo (ρ g Δh ΔT/T) entre os dois lados
- Trocas de ar por hora (ACH) = volume de ar que entra pelas aberturas externas em uma hora ÷ volume do ambiente
- Vazão por uma abertura: Q = Cd × A × fator de abertura × √(2 ΔP / ρ), com ΔP das pressões de vento e de empuxo acima; uma fresta segue Q = C × ΔP^n
- Calor retirado pela ventilação = ρ cp Σ V(saída) × (T(zona) − T(externa)), com ρ cp = 1,2 × 1005 J/(m^3·K), somado em todas as aberturas externas e caminhos forro-ático, hora a hora (kWh por ano)
- Efetividade de exaustão η = (T(fechada) − T(ventilada)) ÷ (T(fechada) − T(externa)), com as temperaturas operativas de um ambiente nas horas ocupadas em que a casa fechada passa de 26 °C e está mais de 1 °C acima da externa; 0 = a ventilação não resfria, 1 = o ambiente acompanha o ar externo
- Graus-hora = Σ máx(T(operativa) − 26 °C, 0) nas horas ocupadas
- Umidade relativa da superfície UR(s) = mín[100, UR(ar) × es(T ar) ÷ es(T superfície)], es(T) = 6,112 × exp(17,62 T ÷ (243,12 + T)) hPa (Magnus); triagem de mofo: média móvel de 30 dias de UR(s) abaixo de 80% enquanto a média de 30 dias de T(s) está entre 5 e 40 °C (teste simplificado da ASHRAE 160)

Referências:

- EnergyPlus (US Department of Energy, NREL) - https://energyplus.net
- ANSI/ASHRAE Standard 140: Standard method of test for the evaluation of building energy analysis computer programs - https://www.ashrae.org/technical-resources/bookstore/standard-140
- EnergyPlus AirflowNetwork and surface-averaged wind pressure coefficients of Swami and Chandra (1987), EnergyPlus Engineering Reference - https://energyplus.net/documentation
- ABNT NBR 15575-1:2021 section 11,4 (thermal performance by simulation) and its public amendment draft (LabEEE, March 2021) - https://labeee.ufsc.br/sites/default/files/documents/P_ABNTNBR15575_1_2020CNGPR_PosCN_SiteLabEEE.pdf
- ANSI/ASHRAE Standard 160-2009: Criteria for moisture-control design analysis in buildings (30-day running average of the surface relative humidity below 80% at 5-40 C; later addenda propose a mould index) - https://www.ashrae.org/technical-resources/standards-and-guidelines
- WHO guidelines for indoor air quality: dampness and mould (2009) - https://www.who.int/publications/i/item/WHO-EURO-2009-4256-44019-62079-eng

Radiance

Usado para: Conferência da luz natural do motor rápido: sDA300/50%, ASE1000,250, lux médio e pontos de luz natural do LEED (seção 8,1).

Parâmetros:

- Coeficientes de luz natural em duas fases (rfluxmtx), 4 reflexões
- Céu de Perez construído a partir do arquivo climático (gendaymtx), 2,305 trechos de céu, 8,760 horas
- Regra de persianas por ambiente: persianas fechadas (transmitância de 5%) quando mais de 2% do ambiente recebe 1,000 lux de sol direto
- Transmitância do vidro de 0,80 para toda a abertura; sem mobiliário, caixilhos, vizinhos nem árvores

Fórmulas:

- Iluminância no sensor = Σ (coeficiente de luz natural × luminância do trecho de céu), somada nos 2,305 trechos em cada hora
- sDA e ASE como definidos na IES LM-83 (mesmas definições do motor rápido)

Referências:

- Radiance Synthetic Imaging System (Lawrence Berkeley National Laboratory) - https://www.radiance-online.org
- CIE 171:2006 Test cases to assess the accuracy of lighting computer programs - https://cie.co.at/publications/test-cases-assess-accuracy-lighting-computer-programs
- Perez et al. (1993): all-weather model for sky luminance distribution - https://doi.org/10.1016/0038-092X(93)90017-I
- ANSI/IES LM-83-23: sDA and ASE - https://webstore.ansi.org/standards/iesna/ansiieslm8323

OpenFOAM (CFD)

Usado para: Coeficientes de pressão do vento (Cp) à frente de cada janela, porta e abertura de beiral, para 24 direções do vento; alimentam o AirflowNetwork do EnergyPlus (seções 6,4 e 6,5).

Parâmetros:

- RANS incompressível permanente (simpleFoam), modelo de turbulência k-epsilon padrão, funções de parede
- Entrada com camada limite atmosférica: 10 m/s a 10 m, comprimento de rugosidade z0 = 0,3 m (suburbano)
- Domínio de 6H a montante, 15H a jusante, 5H de cada lado, 6H acima (H = altura da edificação); snappyHexMesh, células de 0,15 m na casa, mais grossas em volta dos muros do lote e dos vizinhos
- Entorno: muros do lote e edificações vizinhas como caixas fechadas com alturas estimadas por fotografias
- Convergência: resíduos p 1e-5, U 1e-6, k e epsilon 1e-5; a pressão é a média das últimas 20 iterações

Fórmulas:

- $Cp = p \div (\frac{1}{2}\ \rho\ U_EP(z)^2)$, com U_EP(z) = U10 × (z ÷ 10)^0,22 o perfil de vento que o EnergyPlus usa
- $Cp(EnergyPlus) = Cp(CFD) \times (U_CFD(z) \div U_EP(z))^2$, a correção pela diferença de perfis de vento (fator de 0,39 a 0,79 conforme a altura)
- Quantidade de movimento com média de Reynolds: $\nabla\cdot(U\ U) = -\nabla p/\rho + \nabla\cdot[(\nu + \nu_t)(\nabla U + \nabla U^T)]$, com $\nu_t = C\mu\ k^2 \div \varepsilon$ e Cμ = 0,09

Referências:

- OpenFOAM v2312 (OpenCFD / ESI Group), computational wind engineering with RANS k-epsilon - https://www.openfoam.com
- EN 1991-1-4: Eurocode 1, wind actions (table 7,1, pressure coefficients of vertical walls of rectangular buildings) - https://eurocodes.jrc.ec.europa.eu
- EnergyPlus AirflowNetwork and surface-averaged wind pressure coefficients of Swami and Chandra (1987), EnergyPlus Engineering Reference - https://energyplus.net/documentation

Análise de biofilia (traçado de raios e isovista em planta, deste projeto)

Usado para: Vistas para fora de cada ambiente (céu, vegetação, chão, distância), a Matriz de Design Biofílico de 14 padrões, o Índice de Cura Biofílico e as sugestões (seção 9 e a aba Biofilia).

Parâmetros:

- Alturas do olho 1,2 m (sentado) e 1,6 m (em pé), 1,0 m atrás do plano da janela; campo de visão 84° × 56°, 400 × 256 raios por vista; a abertura é o retângulo de vidro da janela

- Classes: céu (nenhum obstáculo acima do horizonte), vegetação (árvores do IFC, caixas para tronco e copa), chão (plano em z = 0), construído (paredes, telhados, vizinhos); as árvores NÃO entram nos motores do caso base, só aqui
- Teste das três camadas: céu, vegetação (a camada intermediária; muro, rua ou casas vizinhas não são natureza) e chão, cada um com ao menos 5% da abertura; vista verde = vegetação com ao menos 15% da abertura
- Distância focal = distância mediana ao primeiro obstáculo (construído ou vegetação) na faixa horizontal de ±5° da abertura, medida a partir do olho (1 m atrás da janela); comparada com 6 m. Supõe-se um pavimento com o piso em z = 0,1 m
- Isovista em planta: 72 direções a 1,4 m a partir de uma grade de 0,6 m dentro de cada ambiente; refúgio = um ponto com ao menos 60% das direções bloqueadas em 2 m e uma linha de visão de 6 m ou mais
- Coluna da matriz pelos ambientes contados (ocupados e não de serviço): nenhum = não incluído; só uma forma fraca = só em detalhe; até a metade = em poucas áreas; mais da metade = casa; indicadores indiretos de baixa confiança ficam limitados a em poucas áreas
- Índice de cura: dez componentes 0, 1 ou 2; luz do sol pelas horas de sol direto nas janelas dos ambientes contados (0: nenhum ambiente recebe 0,05 h/dia; 1: alguns recebem; 2: ao menos metade recebe 0,5 h/dia ou mais de dois ou mais quadrantes da bússola), vida pelas árvores e vistas verdes, curvas pelos elementos curvos do IFC; os demais vêm do proprietário (project.json, biophilia)
- Cenário de parede verde: uma placa idealizada de folhagem de 0,4 m de espessura e 4 m de largura (1,8 m de altura; 3,4 m como limite superior), 0,2 m à frente do obstáculo de cada janela cujo obstáculo mais próximo está a menos de 4 m e cobre 60% ou mais da abertura; medido só nas vistas, nunca nos motores do caso base

Fórmulas:

- BHI = Luz + Cor + Gravidade + Fractais + Curvas + Detalhe + Água + Vida + Representações da natureza + Complexidade organizada, cada um 0 (nenhum), 1 (algum) ou 2 (muito); 0 ≤ BHI ≤ 20 (Salingaros 2019)
- Parcela da abertura de uma classe = raios da classe que cruzam o retângulo da janela ÷ raios que o cruzam
- Raio pela abertura: olho + t·d com t = distância atrás da janela ÷ (d · n) e o ponto de cruzamento dentro do retângulo de vidro
- Área do isovista ≈ ½ Σ r^2 Δθ nas 72 linhas de visão r (Δθ = 5°)

Referências:

- Embree ray-tracing kernels (Intel) - https://github.com/embree/embree
- Browning, Ryan and Clancy (2014): 14 Patterns of Biophilic Design, Terrapin Bright Green - https://www.terrapinbrightgreen.com/reports/14-patterns/
- Salingaros (2019): The biophilic healing index predicts effects of the built environment on our wellbeing, Journal of Biourbanism 8 - https://www.biourbanism.org/the-biophilic-healing-index-predicts-effects-of-the-built-environment-on-our-wellbeing/
- Salingaros: Neuroscience experiments to verify the geometry of healing environments, proposing a Biophilic Healing Index (book chapter, Routledge) - https://www.routledge.com
- UGREEN: Medimos a Biofilia Dessa Mansão Antes da Obra (video; source of the seven-column rubric and the three-layer view rule) - https://www.youtube.com/watch?v=jMehPp3SbCo
- Alvarsson, Wiens and Nilsson (2010): Stress recovery during exposure to nature sound and environmental noise, Int. J. Environ. Res. Public Health 7(3) - https://doi.org/10.3390/ijerph7031036
- Lavdas and Salingaros (2022): Architectural beauty: developing a measurable and objective scale, Challenges 13(2), 56 - https://doi.org/10.3390/challe13020056

Software utilizado

Python 3,11,9 · NumPy 2,4,6 · pandas 3,0,6 · pvlib 0,16,1 · trimesh 5,1,1 · Embree (embreex) 4,4,0 · IfcOpenShell 0,9,0 · Shapely 2,2,0 · Numba 0,68,0 · Matplotlib 3,11,2 · SciPy 1,17,1 · EnergyPlus 26,2,0 · Radiance 6,0,2

Etapas de cálculo e a confiança em cada uma

Etapa	Como é calculado	Confiabilidade
Modelo 3D e orientação	O edifício é lido de um arquivo IFC (IfcOpenShell). Os ambientes são os volumes IfcSpace; paredes, lajes, telhados, janelas e portas viram malhas de triângulos. O modelo é girado para que o norte verdadeiro venha do Norte Verdadeiro do IFC (mais uma correção opcional). Por quê: Tão exato quanto o modelo: tamanhos, posição das janelas e materiais são estimativas, a menos que o modelo venha de um levantamento.	Alta
Posição do sol e sombras	Posição solar para cada uma das 8,760 horas com o pvlib (algoritmo baseado no NREL SPA). A partir de uma grade de pontos sensores (0,5 m, a 0,76 m de altura) em cada ambiente, traça-se um raio em direção ao sol contra todos os elementos opacos com o Embree (biblioteca de traçado de raios): bloqueado = sombra; um raio que passa por uma janela é atenuado pela transmitância dela. Por quê: A geometria do sol é determinística; o resultado só é tão bom quanto a geometria (vizinhos e árvores só contam se estiverem no modelo).	Alta
Clima	Um ano meteorológico típico com dados horários (.epw do EnergyPlus, como o TMYx do climate.onebuilding.org, ou um ano típico do PVGIS): temperatura, umidade, radiação direta/difusa/global, velocidade e direção do vento. Por quê: Um ano típico não é uma previsão: anos reais são mais quentes ou mais frios. Os dados de vento são de terreno aberto a 10 m.	Média
Luz natural (lux e lumens)	Iluminância no plano de trabalho = sol direto (traçado de raios) + luz do céu (céu isotrópico, fator de visão do céu por traçado de raios) + componente inter-refletida (método do fluxo dividido, refletância média 0,55). A radiação é convertida em lux com eficácias luminosas de 100 lm/W (direta) e 115 lm/W (difusa). Os lumens das lâmpadas usam o método dos lumens: lux x área / (utilização 0,45 x manutenção 0,8). Métricas: lux no centro do ambiente da NBR 15575, sDA300/50% e ASE1000,250 (IES LM-83), horas de sol da EN 17037. Por quê: O céu isotrópico ignora o céu mais claro perto do sol e o fluxo dividido superestima a luz no fundo dos ambientes: a conferência com o Radiance dá sDA ponderado de 6% contra 41% aqui. Use-o só para comparações rápidas.	Média
Motor de referência para luz natural: Radiance	Os mesmos ambientes e pontos de medição são recalculados com o Radiance (Lawrence Berkeley National Laboratory), um traçador de raios reverso validado nos casos de teste da CIE 171:2006 e o motor por trás do ClimateStudio e do Honeybee. Método: coeficientes de luz natural em duas fases (rfluxmtx, 4 reflexões) multiplicados por um céu de Perez construído a partir do arquivo climático (gendaymtx, 2,305 trechos de céu) nas 8,760 horas; sDA300/50% e ASE1000,250 como na IES LM-83, com a regra de persianas aproximada por ambiente (persianas fechadas, transmitância de 5%, quando mais de 2% do ambiente recebe 1,000 lux de sol direto). Um sensor acima do telhado confere o céu: ele reproduz a iluminância do arquivo climático com diferença de cerca de 2%. Por quê: Motor validado; o que ainda falta na rodada é mobiliário, caixilhos, a treliça da porta de vidro e árvores (as caixas dos vizinhos estão incluídas), e a regra de persianas é simplificada. Prefira estes números aos do motor rápido de luz natural.	Alta
Motor de referência para calor e energia: EnergyPlus	Os pacotes de melhoria são recalculados com o EnergyPlus (Departamento de Energia dos EUA), o motor de balanço de calor validado pela norma ASHRAE 140 e usado dentro do DesignBuilder e do OpenStudio. Uma zona por ambiente mais uma zona de forro ventilado acima dele; paredes compartilhadas entre ambientes; funções de transferência de condução para cada camada; janelas como sistemas de vidro simples; os beirais reais como superfícies de sombra; ventilação das janelas por vento e empuxo (janelas 50% abertas quando o ar externo está mais frio e acima de 18 C); um ar-condicionado ideal com o mesmo ponto de ajuste, horários e COP do motor rápido. O conforto vem de uma rodada sem climatização (adaptativo da ASHRAE 55) e a energia de uma segunda rodada com o ar-condicionado. Por quê: Motor validado, mas o modelo é simplificado: telhado plano com o mesmo volume de forro, sem ganhos internos, sem abertura de portas, sem sombra de vizinhos, propriedades do vidro supostas, sem calibração com medições. Compare opções; não trate a conta como previsão.	Média
NBR 15575-1:2021 por simulação e ventilação cruzada (EnergyPlus + AirflowNetwork)	Um modelo real e um modelo de referência da casa são simulados nas 8,760 horas com o EnergyPlus. A ventilação natural é resolvida pela rede de fluxo de ar (AirflowNetwork): janelas, portas abertas e frestas são caminhos de ar movidos pela pressão do vento (coeficientes de fachada de Swami e Chandra para edificação baixa, velocidade local do vento na altura da abertura), pelo efeito chaminé e pela altura da abertura; as janelas abrem só com o ambiente ocupado, com o ar a pelo menos 19 C e mais quente que o externo; as janelas dos banheiros ficam abertas. Ocupação, iluminação e equipamentos seguem as tabelas da norma; uma segunda rodada com as janelas fechadas e ar-condicionado ideal (refrigeração a 23 C / aquecimento a 21 C quando ocupado) dá a carga térmica. PHFT, temperaturas operativas máxima e mínima e redução da carga dão os níveis mínimo, intermediário e superior. Por quê: Segue a seção 11,4 da NBR 15575-1:2021 (texto integral, tabelas conferidas com o projeto público de emenda); a zona bioclimática de Maringá na NBR 15220-3:2024 vem de um artigo não oficial; nossas suposições estão listadas no relatório (ambientes transitórios, portas abertas, temperatura do solo). Os coeficientes de pressão do vento vêm do CFD do OpenFOAM desta casa com seus muros e vizinhos (alturas estimadas), não de um ensaio em túnel de vento. Não é um laudo oficial de conformidade.	Média
Circulação do ar, alterações da planta e exaustão do ar quente (EnergyPlus + AirflowNetwork)	A mesma rede de fluxo de ar é simulada no ano inteiro com várias alterações da planta (portas fechadas, grelha acima das portas, janelas de abrir, exaustão pelo forro). A vazão por cada janela, porta, grelha e abertura do forro é lida hora a hora e tirada a média das horas com janelas abertas, das horas quentes e de cada direção do vento, o que dá as setas na planta. A efetividade de exaustão compara a temperatura operativa de cada ambiente com uma simulação de janelas fechadas e com a temperatura externa; o calor retirado pelo ar é rho cp V (T zona - T externa). Por quê: As vazões são médias entre ambientes (um nó de ar por ambiente, sem campo de velocidade e sem idade do ar ou zonas de estagnação); a pressão do vento vem do CFD só do exterior, com as aberturas fechadas, e a grelha, a abertura do forro e a fração das janelas de abrir são tamanhos idealizados, não produtos. Bom para ordenar alterações da planta (as diferenças entre variantes são mais confiáveis que as vazões absolutas); não substitui um CFD interno nem um teste de fumaça.	Média
Pressão do vento nas fachadas: OpenFOAM (CFD)	Para cada uma de 24 direções de vento (a cada 15 graus) a casa (invólucro fechado reconstruído dos telhados, beirais e varandas do IFC) é colocada em um domínio de cálculo (6H a montante, 15H a jusante, 5H nas laterais, 6H acima, H = altura da edificação) e malhada com o snappyHexMesh (1,2 a 2,0 milhões de células, 0,15 m na casa, mais grossas em volta dos muros do lote e dos vizinhos). O OpenFOAM v2312 resolve as equações de Navier-Stokes com média de Reynolds em regime permanente, com o modelo de turbulência k-epsilon padrão, entrada com camada limite atmosférica (10 m/s a 10 m, comprimento de rugosidade 0,3 m) e funções de parede para solo rugoso. Os muros do lote e as edificações vizinhas entram como caixas fechadas (alturas estimadas por fotografias). A pressão 0,3 m à frente de cada janela, porta e abertura de beiral, convertida em coeficiente da pressão dinâmica do perfil de vento do EnergyPlus (lei de potência, terreno suburbano) naquela altura, dá os coeficientes de pressão entregues à rede de fluxo de ar do EnergyPlus. Uma verificação numérica (três malhas, rugosidade, tamanho do domínio, uma caixa comparada com o Eurocódigo) dá a incerteza de cada coeficiente. Roda em um contêiner Docker. Por quê: O RANS k-epsilon é o modelo de engenharia usual para cargas médias de vento em edificações e o OpenFOAM é validado para ele, mas esta rodada usa a forma real do telhado, os muros do lote e os vizinhos com alturas estimadas por fotografias, sem árvores, uma única rugosidade de aproximação e malha de tamanho moderado; não houve conferência com túnel de vento.	Média
Temperatura interna (modelo térmico)	Cada ambiente é um modelo de balanço térmico concentrado resolvido hora a hora (Python, compilado com Numba): camadas de parede, forro e piso como nós de armazenamento de calor (resistências e capacidades a partir da condutividade, densidade, calor específico e espessura, no estilo ISO 6946 / NBR 15220-2), temperatura sol-ar nas superfícies externas, sótão ventilado, janelas (U e ganho solar), ventilação (infiltração com tudo fechado, ventilação cruzada pelo vento com janelas abertas, ambientes ligados por portas) e massa térmica. Temperatura operativa = média da temperatura do ar e das superfícies. O conforto usa o modelo adaptativo da ASHRAE 55 (aceitabilidade de 80% e 90%) e as verificações de dia mais quente/frio da NBR 15575. Por quê: Um modelo simplificado de uma zona por ambiente, não calibrado com medições. Foi conferido contra o EnergyPlus nos pacotes de melhoria (veja a etapa do EnergyPlus): os motores concordam na ordem das medidas, mas o EnergyPlus dá cerca de metade da energia de ar-condicionado. Use-o para comparações rápidas, não como previsão exata.	Média
Energia e custo de ar-condicionado / aquecimento	Quando o ambiente fica acima da temperatura de refrigeração (ou abaixo da de aquecimento) no seu horário de uso, o modelo soma o fluxo de calor necessário para manter a temperatura; eletricidade = calor / COP (refrigeração) ou combustível = calor / eficiência (aquecimento), custo = energia x tarifa. As janelas ficam fechadas com o equipamento ligado. Só calor sensível; sem calor de pessoas, aparelhos ou iluminação. Por quê: As contas reais diferem: carga latente, hábitos dos moradores, eficiência do equipamento e a tarifa (uma suposição) importam. Trate o custo como ordem de grandeza e como forma de comparar opções.	Baixa
Vento e ventilação cruzada	Rosas dos ventos do arquivo climático; cada janela é classificada como a barlavento / sotavento / lateral a cada hora; ambientes cujas janelas conectadas ficam de frente para o vento e para o lado oposto recebem mais trocas de ar. Sem cálculo de pressão (o CFD e o AirflowNetwork são usados só na seção 6,4). Por quê: Uma estimativa por regras: o vento na casa é menor e mais turbulento que na estação; não há cálculo de escoamento por pressão.	Baixa
Cenários de melhoria	Cada melhoria altera o modelo-base e o ano inteiro é simulado de novo: o isolamento do telhado soma uma camada de condução (espessura / condutividade) no lado do sótão do forro; a vedação reduz a taxa de trocas de ar com a casa fechada; o vidro altera o U da janela, o fator de ganho solar e a transmitância visível; o brise fixo corta o sol direto pela profundidade da sombra = beiral x tan(ângulo de perfil); persianas móveis multiplicam o ganho solar por 0,3 sempre que o sol na janela passa de 250 W/m2 durante o dia.	Média

	Por quê: Bom para ordenar opções (as diferenças entre cenários são mais confiáveis que os valores absolutos). As propriedades dos materiais são valores de catálogo; a confiança de cada valor aparece ao lado dele. O sombreamento é analítico, não por traçado de raios.	
Avaliações e pré-avaliação LEED	Os números são comparados com normas da ABNT quando existem (NBR 15575, NBR 15220, NBR 5413, NBR 16401), com padrões internacionais nos demais casos (EN 17037, IES LM-83, ASHRAE 55, OMS) e com algumas regras práticas identificadas como tal. Os pontos de luz natural do LEED v4,1 seguem a Opção 1 (sDA300/50% e ASE1000,250). Por quê: Vários valores de norma foram lidos de resumos públicos ou projetos de emenda, não dos textos completos da ABNT; o resultado LEED é uma pré-avaliação indicativa, não uma certificação.	Média
Vistas para fora de cada ambiente (traçado de raios)	De um olho dentro de cada ambiente (sentado a 1,2 m e em pé a 1,6 m, 1 m atrás da janela, olhando para fora) traça-se um raio por pixel pela abertura da janela e classifica-se pelo que ele encontra primeiro: céu, vegetação (as árvores do IFC), chão ou construído (paredes, telhados, vizinhos). Informam-se as parcelas da abertura, a distância ao obstáculo mais próximo na faixa horizontal (mediana) e um teste de três camadas (céu, plano intermediário, chão, cada uma com ao menos 5% da abertura), e as imagens coloridas são desenhadas a partir das mesmas classes. Um isovista em planta (72 linhas de visão a 1,4 m a partir de uma grade de 0,6 m do ambiente) dá a linha de visão mais longa e o número de grupos separados de vistas longas. Por quê: A geometria é tão boa quanto o modelo: as árvores são caixas em posições estimadas de uma foto da rua, vizinhos e muros têm alturas estimadas, o vidro é tratado como totalmente transparente e a vista é uma direção fixa. A distância de 6 m e o teste das três camadas são regras desta ferramenta tiradas do resumo de um vídeo, não um padrão publicado.	Média
Triagem de umidade e mofo (EnergyPlus)	Duas simulações do ano inteiro do EnergyPlus da casa real sem climatização (janelas abertas pelos moradores e janelas fechadas) dão, para cada ambiente, a umidade relativa do ar, a temperatura do ar e a temperatura da face interna de suas paredes e forro opacos. A umidade relativa da superfície é UR(ar) x es(T ar) / es(T superfície) na superfície mais fria (es pela fórmula de Magnus). Aplica-se o teste simplificado da ASHRAE 160: a média móvel de 30 dias da umidade relativa da superfície deve ficar abaixo de 80% enquanto a temperatura média de 30 dias está entre 5 e 40 C; a parcela do ano acima do limite e a maior média de 30 dias aparecem ao lado do sol direto e da ventilação cruzada do ambiente. Por quê: Uma triagem, não um diagnóstico. No modelo as pessoas são a única fonte de umidade (quartos e sala), a cozinha e os banheiros não têm nenhuma, as paredes não armazenam umidade, não há chuva nem umidade ascendente, e a temperatura da superfície é a da parede ou forro plano mais frio, não a de cantos e pontes térmicas. Adendos da ASHRAE trocam o limite fixo de 80% por um modelo de índice de mofo porque ele é conservador (confira a edição vigente), e a OMS (2009) não dá limite numérico. O caso 'fechada' é um caso-limite (janelas fechadas o ano todo, sem ar-condicionado), não como a casa é usada; a média de 30 dias dá a volta no ano.	Baixa
Biofilia: matriz de design e índice de cura	Os 14 padrões de design biofílico (Browning, Ryan e Clancy 2014) são colocados em sete colunas (não se aplica, não incluído, só em detalhe, em poucas áreas, casa, casa + 1 edifício, todos os edifícios), uma régua tirada do vídeo da UGREEN. A coluna é escolhida pela parcela dos ambientes ocupados, fora os de serviço, que cumprem um critério forte (mais da metade = casa; até a metade = em poucas áreas); só uma forma fraca dá apenas em detalhe. Padrões que nenhum motor mede (água, conexão não visual, material, complexidade, risco) ficam não avaliados, a menos que o proprietário os declare. O Índice de Cura Biofílico de Salingaros soma dez componentes avaliados em 0, 1 ou 2 (0 a 20); só luz do sol, vida e curvas são estimados pelo modelo, os demais pedem a avaliação de um observador. Nenhum agregado da matriz é inventado. Por quê: Apenas indicativo. Os limiares são desta ferramenta; a matriz não tem nota oficial; o índice de Salingaros é uma estimativa de observador com pesos iguais e o autor chama sua ligação com a cura de conjectura, não verificada. Os padrões marcados como indicadores indiretos (estímulos não rítmicos, sistemas naturais, mistério) usam indicadores fracos e ficam limitados abaixo de 'casa'. Sem validação clínica; plantas em vasos não purificam o ar em ambientes reais.	Baixa

Referências

- pvlib python: a Python package for modeling solar energy systems (Holmgren, Hansen, Mikofski, JOSS 2018) - https://joss.theoj.org/papers/10.21105/joss.00884
- PVGIS typical meteorological year (European Commission JRC) - https://re.jrc.ec.europa.eu/pvg_tools/en/
- Climate.OneBuilding.Org: TMYx weather files - https://climate.onebuilding.org
- Embree ray-tracing kernels (Intel) - https://github.com/embree/embree
- IfcOpenShell: open-source IFC toolkit - https://ifcopenshell.org
- Numba: JIT compiler for Python - https://numba.pydata.org
- ASHRAE Standard 55: thermal environmental conditions for human occupancy (adaptive comfort model) - https://www.ashrae.org/technical-resources/standards-and-guidelines
- ABNT NBR 15575 (Residential buildings - performance) and NBR 15220 (Thermal performance of buildings) - https://www.abntcatalogo.com.br
- EN 17037: Daylight in buildings - https://standards.cencenelec.eu
- Radiance Synthetic Imaging System (Lawrence Berkeley National Laboratory) - https://www.radiance-online.org
- CIE 171:2006 Test cases to assess the accuracy of lighting computer programs - https://cie.co.at/publications/test-cases-assess-accuracy-lighting-computer-programs
- EnergyPlus (US Department of Energy, NREL) - https://energyplus.net
- ANSI/ASHRAE Standard 140: Standard method of test for the evaluation of building energy analysis computer programs - https://www.ashrae.org/technical-resources/bookstore/standard-140
- Perez et al. (1993): all-weather model for sky luminance distribution - https://doi.org/10.1016/0038-092X(93)90017-I
- EnergyPlus AirflowNetwork and surface-averaged wind pressure coefficients of Swami and Chandra (1987), EnergyPlus Engineering Reference - https://energyplus.net/documentation
- ABNT NBR 15575-1:2021 section 11.4 (thermal performance by simulation) and its public amendment draft (LabEEE, March 2021) - https://labeee.ufsc.br/sites/default/files/documents/P_ABNTNBR15575_1_2020CNGPR_PosCN_SiteLabEEE.pdf
- OpenFOAM v2312 (OpenCFD / ESI Group), computational wind engineering with RANS k-epsilon - https://www.openfoam.com
- ANSI/IES LM-83-23: sDA and ASE - https://webstore.ansi.org/standards/iesna/ansiieslm8323
- USGBC LEED v4,1 Daylight credit (Option 1: simulation) - https://leeduser.buildinggreen.com/credit/CI-v4.1/EQc7
- AIVC: air infiltration reduction by weatherstripping retrofits - https://www.aivc.org/resource/reduction-air-infiltration-due-window-and-door-retrofits-older-home
- WHO Housing and Health Guidelines (2018) - https://www.who.int/publications/i/item/9789241550376
- EN 1991-1-4: Eurocode 1, wind actions (table 7.1, pressure coefficients of vertical walls of rectangular buildings) - https://eurocodes.jrc.ec.europa.eu
- Browning, Ryan and Clancy (2014): 14 Patterns of Biophilic Design, Terrapin Bright Green - https://www.terrapinbrightgreen.com/reports/14-patterns/
- Salingaros (2019): The biophilic healing index predicts effects of the built environment on our wellbeing, Journal of Biourbanism 8 - https://www.biourbanism.org/the-biophilic-healing-index-predicts-effects-of-the-built-environment-on-our-wellbeing/
- Salingaros: Neuroscience experiments to verify the geometry of healing environments, proposing a Biophilic Healing Index (book chapter, Routledge) - https://www.routledge.com
- UGREEN: Medimos a Biofilia Dessa Mansão Antes da Obra (video; source of the seven-column rubric and the three-layer view rule) - https://www.youtube.com/watch?v=jMehPp3SbCo
- Alvarsson, Wiens and Nilsson (2010): Stress recovery during exposure to nature sound and environmental noise, Int. J. Environ. Res. Public Health 7(3) - https://doi.org/10.3390/ijerph7031036
- Lavdas and Salingaros (2022): Architectural beauty: developing a measurable and objective scale, Challenges 13(2), 56 - https://doi.org/10.3390/challe13020056
- ANSI/ASHRAE Standard 160-2009: Criteria for moisture-control design analysis in buildings (30-day running average of the surface relative humidity below 80% at 5-40 C; later addenda propose a mould index) - https://www.ashrae.org/technical-resources/standards-and-guidelines
- WHO guidelines for indoor air quality: dampness and mould (2009) - https://www.who.int/publications/i/item/WHO-EURO-2009-4256-44019-62079-eng

11. Premissas, limites e fontes

- As **dimensões** vêm do modelo 3D fornecido: as plantas aprovadas na prefeitura (casa de 2008 em 1:50, ampliação dos fundos de 2012 em 1:75, Prefeitura de Maringá); a casa construída pode diferir em detalhes e isto não é um levantamento.
- Os **materiais**: o bloco cerâmico padrão brasileiro de 8 furos com reboco (não confirmado) e telhado sobre forro de laje (as plantas indicam telha de cimento sobre forro de laje; o modelo usa os valores da telha cerâmica, termicamente parecidos). Prédios vizinhos, árvores da rua e cortinas não são modelados, a menos que estejam no modelo.
- As **portas** são supostas abertas para luz e ar. Móveis, pessoas, eletrodomésticos e calor da iluminação não estão incluídos (casa vazia).
- O modelo de conforto é um balanço térmico horário simplificado, não calibrado com medições: use-o para comparar ambientes e opções. O EnergyPlus seria o próximo nível de rigor.
- Os dados de **vento** são de terreno aberto a 10 m; dentro de um lote com muros e vizinhos as velocidades são menores. A regra de vento do motor rápido ignora isso; a ventilação por pressão da seção 6,4 inclui os muros e vizinhos pelo CFD, com alturas estimadas.
- A **luz natural** usa um céu isotrópico; céus reais parcialmente nublados são mais claros perto do sol.
- As escalas marcadas *Regra prática* são nossas; as marcadas como norma vêm dos documentos listados abaixo. Vários valores de norma foram lidos de resumos públicos e projetos de emenda: confirme-os nos textos completos da ABNT antes de usá-los em decisão legal, contratual ou de financiamento.

Fontes

- ABNT NBR 15575-1:2013 (Edificações habitacionais — Desempenho), requisitos de iluminação natural e desempenho térmico
- ABNT NBR 15575-1:2021 + emenda (desempenho térmico por simulação, comparado a uma casa de referência)
- Projeto de emenda da ABNT NBR 15575-4:2021 (mar/2021): método simplificado para paredes, ventilação e áreas transparentes
- Projeto de emenda da ABNT NBR 15575-5:2021: método simplificado para coberturas
- ABNT NBR 15220-3: zoneamento bioclimático brasileiro e diretrizes construtivas (Maringá costuma ser listada na zona 3)
- ABNT NBR 5413:1992 (cancelada em 2013, mas ainda a referência brasileira mais usada para iluminação de RESIDÊNCIAS)
- ABNT NBR ISO/CIE 8995-1:2013 (iluminação de ambientes de trabalho; leitura e escrita 300–500 lx)
- EN 17037:2018 Iluminação natural em edifícios (Anexo Nacional do Reino Unido para moradias: 100/150/200 lx; insolação 1,5/3/4 h)
- IES LM-83-12 (sDA e ASE), como usado no LEED v4,1
- ASHRAE 55, modelo de conforto adaptativo (aceitabilidade de 80% / 90%)
- ABNT NBR 16401-2 (ar-condicionado, conforto interno): verão cerca de 22,5–25,5 °C com 65% de UR e 23–26 °C com 35% de UR
- Passive House Institute, critério: demanda de aquecimento de no máximo 15 kWh por m^2 por ano
- USGBC LEED v4,1, crédito de Luz natural, Opção 1 (simulação): média de sDA300/50% de 40% / 55% / 75% = 1 / 2 / 3 pontos; ASE1000,250 acima de 10% exige estratégia contra ofuscamento (limites lidos na página do crédito v4,1 no LEEDuser)
- ANSI/IES LM-83-23 (publicada em fev/2023): autonomia espacial de luz natural (sDA) e exposição solar anual (ASE); o LEED v4,1 ainda cita a edição de 2012, com as mesmas duas métricas
- OMS, Diretrizes de Habitação e Saúde 2018 (temperatura interna de pelo menos 18 °C)
- Escala de vento Beaufort (OMM)
- Regra prática deste estudo (nenhuma norma dá um número)

Rode de novo depois de mudar o modelo

Edite o modelo 3D (house.ifc) e dê dois cliques em **run_all.bat** na pasta House3D. Ele refaz a simulação, este PDF e os dados do visualizador 3D (viewer / open_viewer.bat).